SHT	REV	DATE	DESCRIPTION	SHT	REV	DATE	DESCRIPTION
1	1	19/05/14	INDEX	41	1	19/05/14	SPARE
2	1	19/05/14	ISOLATOR & PANEL DISTRIBUTION SUPPLIES	42	1	19/05/14	WEISHAUPT BURNER CONTROLLER
3	1	19/05/14	PANEL DISTRIBUTION CIRCUITS	43	1	19/05/14	WEISHAUPT BURNER CONTROLLER
4	1	19/05/14	PANEL DISTRIBUTION CIRCUIT	44	1	19/05/14	WEISHAUPT BURNER CONTROLLER
5	1	19/05/14	SPARE	45	1	19/05/14	WEISHAUPT BURNER CONTROLLER
6	1	19/05/14	MOTOR POWER CIRCUITS	46	1	19/05/14	WEISHAUPT BURNER CONTROLLER
7	1	19/05/14	MOTOR POWER CIRCUITS	47	1	19/05/14	SPARE
8	1	19/05/14	MOTOR POWER CIRCUITS	48	1	19/05/14	110VAC ISOLATOR RELAYS
9	1	19/05/14	SPARE	49	1	19/05/14	SPARE
10	1	19/05/14	SPARE	50	1	19/05/14	PANEL INTERCONNECTION DETAILS
11	1	19/05/14	EMERGENCY STOP BUTTON	51	1	19/05/14	PANEL INTERCONNECTION DETAILS
12	1	19/05/14	SMOKE DETECTOR	52	1	19/05/14	SPARE
13	1	19/05/14	SPARE	53	1	19/05/14	SPARE
14	1	19/05/14	PLC LAYOUT	54	1	19/05/14	INTERNAL PANEL LAYOUT
15	1	19/05/14	PLC COMMS SLOT 2 – ETHERNET CARD	55	1	19/05/14	EXTERNAL PANEL LAYOUT
16	1	19/05/14	PLC COMMS SLOT 1 – ETHERNET CARD	56			
17	1	19/05/14	PLC SLOT 01 – ANALOGUE INPUT CARD	57			
18	1	19/05/14	PLC SLOT 02 – ANALOGUE INPUT CARD	58			
19	1	19/05/14	PLC SLOT 03 – ANALOGUE OUTPUT CARD	59			
20	1	19/05/14	PLC SLOT 04 – 24VDC INPUT CARD	60			
21	1	19/05/14	PLC SLOT 05 – 24VDC OUTPUT CARD	61			
22	1	19/05/14	SPARE	62			
23	1	19/05/14	SPARE	63			
24	1	19/05/14	SPARE	64			
25	1	19/05/14	SAFETY RACK 1 SLOT 01 – AI MODULE	65			
26	1	19/05/14	SAFETY RACK 1 SLOT 02 – AI MODULE	66			
27	1	19/05/14	SAFETY RACK 1 SLOT 03 – AI MODULE	67			
28	1	19/05/14	SAFETY RACK 1 SLOT 04 – DI MODULE	68			
29	1	19/05/14	SAFETY RACK 1 SLOT 05 – DI MODULE	69			
30	1	19/05/14	SAFETY RACK 1 SLOT 06 – DI MODULE	70			
31	1	19/05/14	SAFETY RACK 1 SLOT 07 – DI MODULE	71			
32	1	19/05/14	SAFETY RACK 1 SLOT 08 – DI MODULE	72			
33	1	19/05/14	SAFETY RACK 1 SLOT 09 – DI MODULE	73			
34	1	19/05/14	SAFETY RACK 1 SLOT 10 – DI MODULE	74			
35	1	19/05/14	SAFETY RACK 1 SLOT 11 – DO MODULE	75			
36	1	19/05/14	SAFETY RACK 1 SLOT 12 – DO MODULE	76			
37	1	19/05/14	SAFETY RACK 1 SLOT 13 – DO MODULE	77			
38	1	19/05/14	SPARE	78			
39	1	19/05/14	SPARE	79			
40	1	19/05/14	24VDC CONTROL	80			

WIRE COLOURS

BLACK	400/230V
L/BLUE	NEUTRAL
RED	110VAC
D/BLUE	24VDC
ORANGE	VOLT FREE
VIOLET	SENSORS

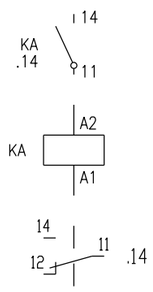

CONTACT SHOWING PIN CONECTIONS AND CROSS REF TO RELAY COIL

COIL SHOWING COIL CONECTIONS

CROSS REF SYMBOL SHOWING REF TO CONTACTS

REV	DATE	MODIFICATION	MS	DG
1	19/05/14	FOR APPROVAL		

DWN CHK

ELTEK SYSTEMS Ltd
ELTEK SYSTEMS LTD
ELTEK HOUSE,
NENE VALLEY BUSINESS PARK
OUNDLE, PETERBOROUGH.PE8 4HN
TEL 01832 277590 FAX 01832 273941
Email: info@eltek-systems.com

TITLE

G4 HEATER PANEL
PC32 LINE 4
WSF, LEICESTER

CLIENT

Flo~Mech

FLO-MECH LTD FLO-MECH HOUSE,
PAXTON ROAD, ORTON GOLDHAY
PETERBOROUGH.PE2 5YA, ENGLAND.
TEL +44(0)1733233166
FAX +44(0)1733235200
Email: enquiries@flo-mech.com
Internet: www.flo-mech.com

DATE 19/05/14
DWG NO 5620
SHEET 1 OF 55

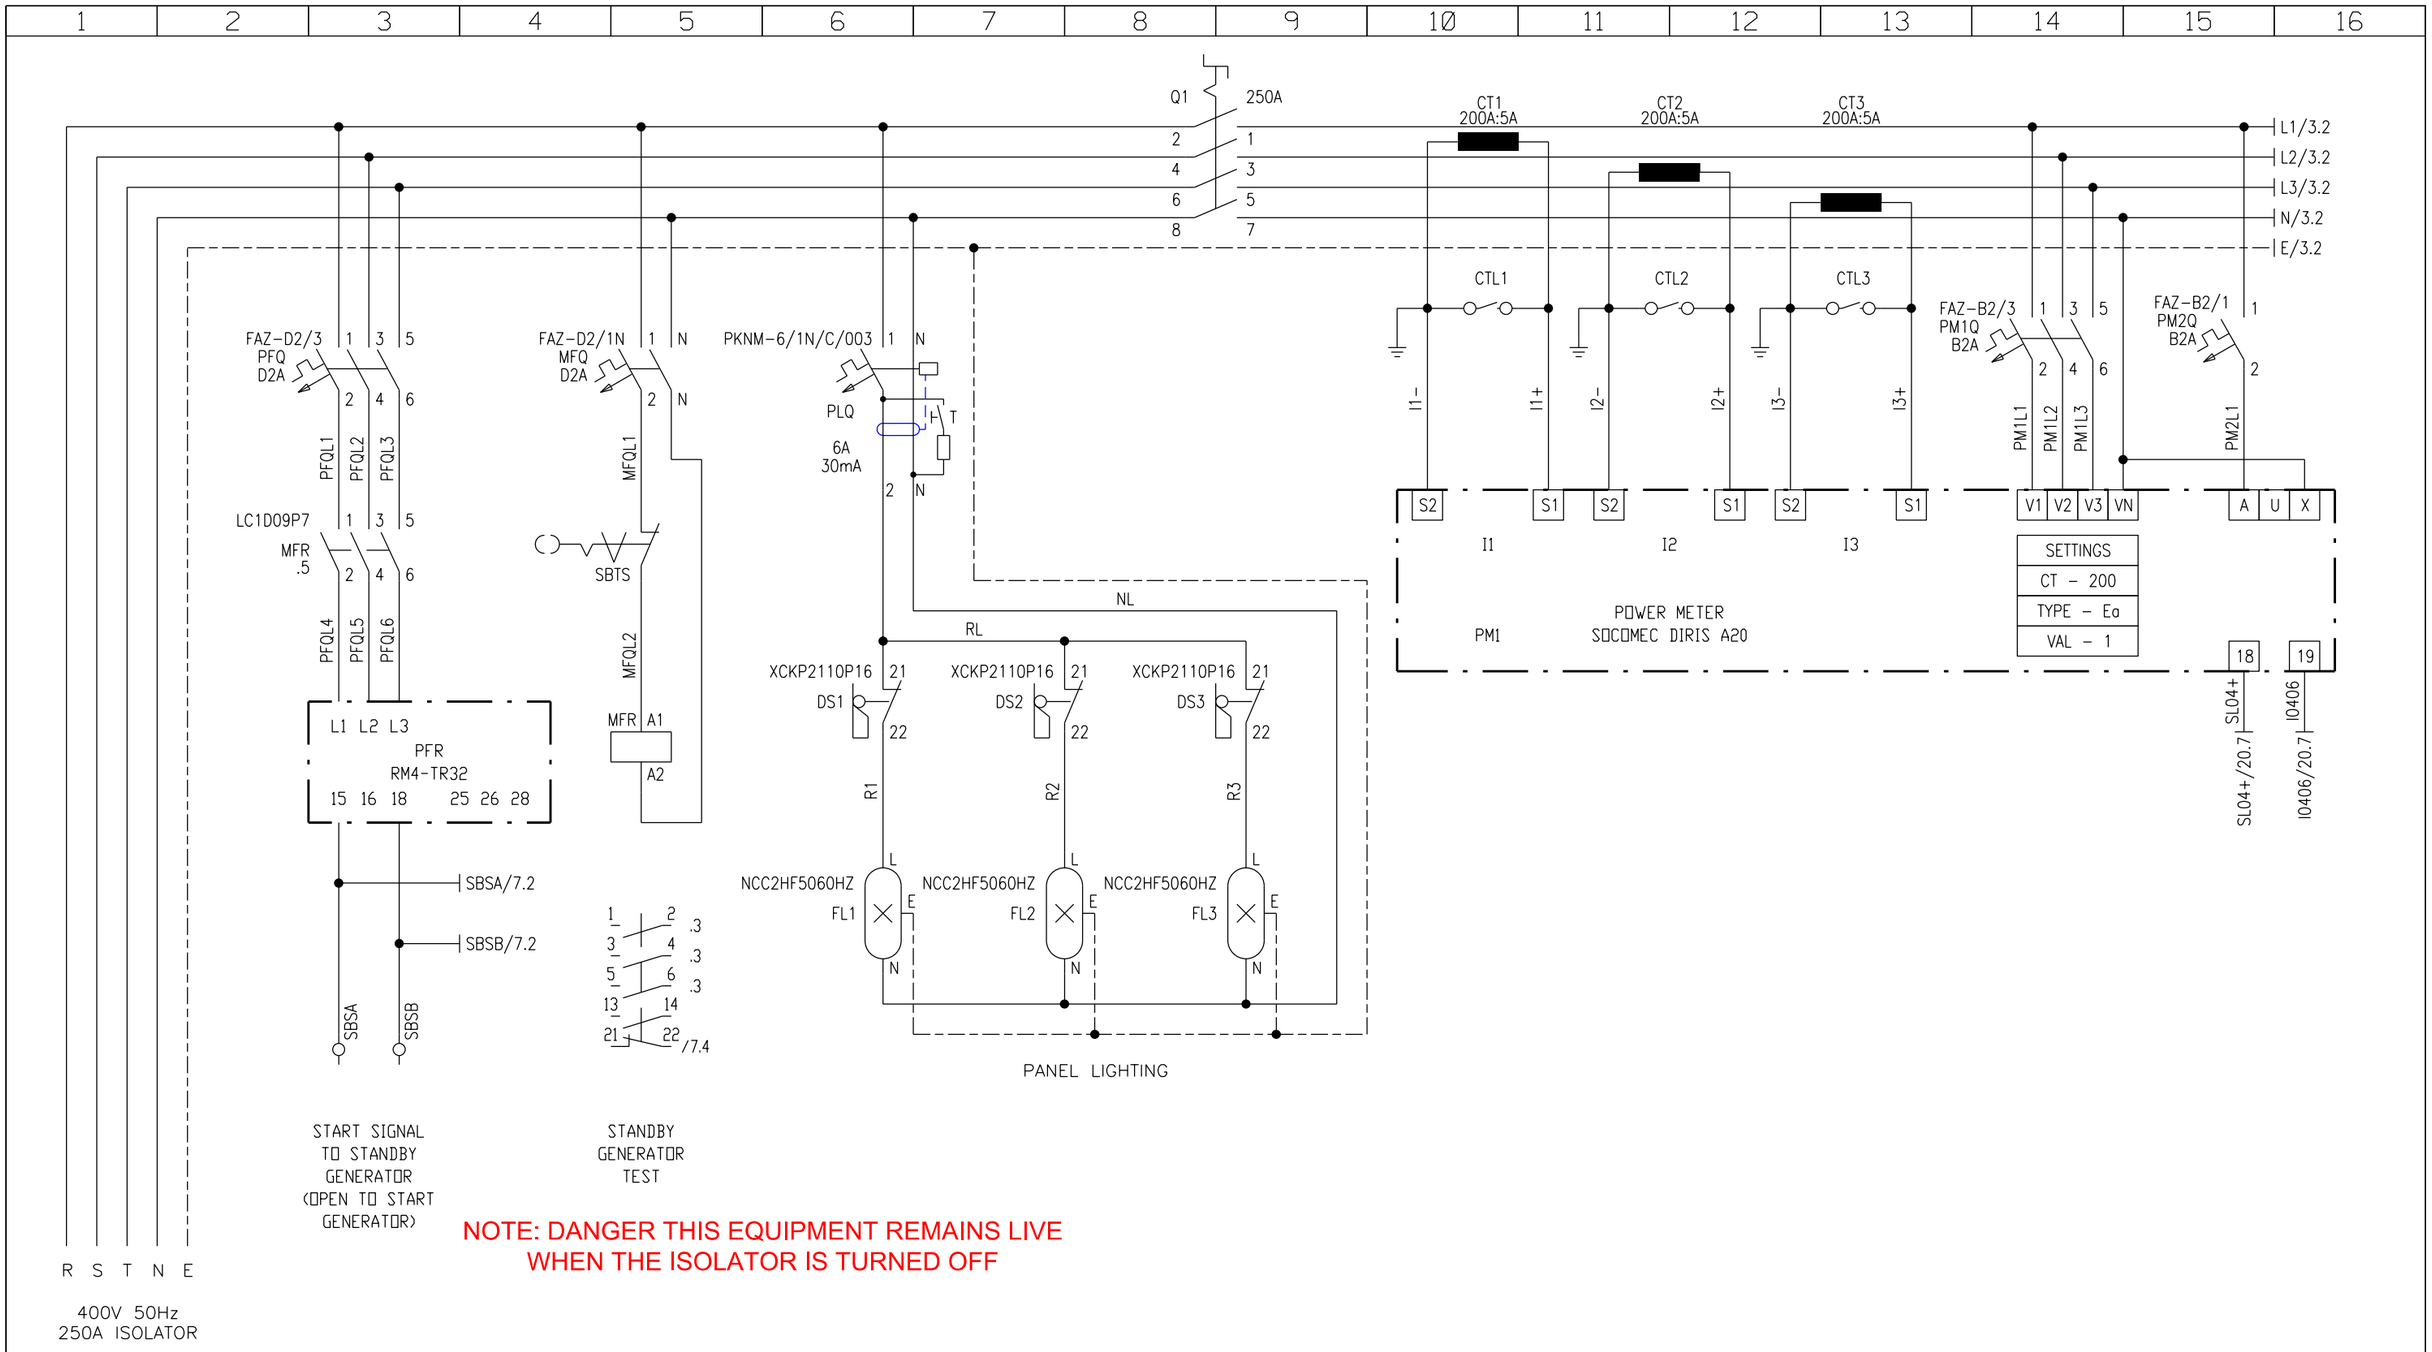

NOTE: DANGER THIS EQUIPMENT REMAINS LIVE WHEN THE ISOLATOR IS TURNED OFF

REV	DATE	MODIFICATION	DWN	CHK
1	19/05/14	FOR APPROVAL	MS	DG

ELTEK SYSTEMS LTD
ELTEK HOUSE,
NENE VALLEY BUSINESS PARK
OUNDLE, PETERBOROUGH,PE8 4HN
TEL 01832 277590 FAX 01832 273941
Email: info@eltek-systems.com

TITLE

G4 HEATER PANEL PC32 LINE 4 WSF, LEICESTER

CLIENT

FLO-MECH LTD FLO-MECH HOUSE,
PAXTON ROAD, ORTON GOLDHAY
PETERBOROUGH.PE2 5YA, ENGLAND.
TEL +44(0)1733233166
FAX +44(0)1733235200
Email: enquiries@flo-mech.com
Internet: www.flo-mech.com

DATE 19/05/14
DWG NO 5620
SHEET 2 OF 55

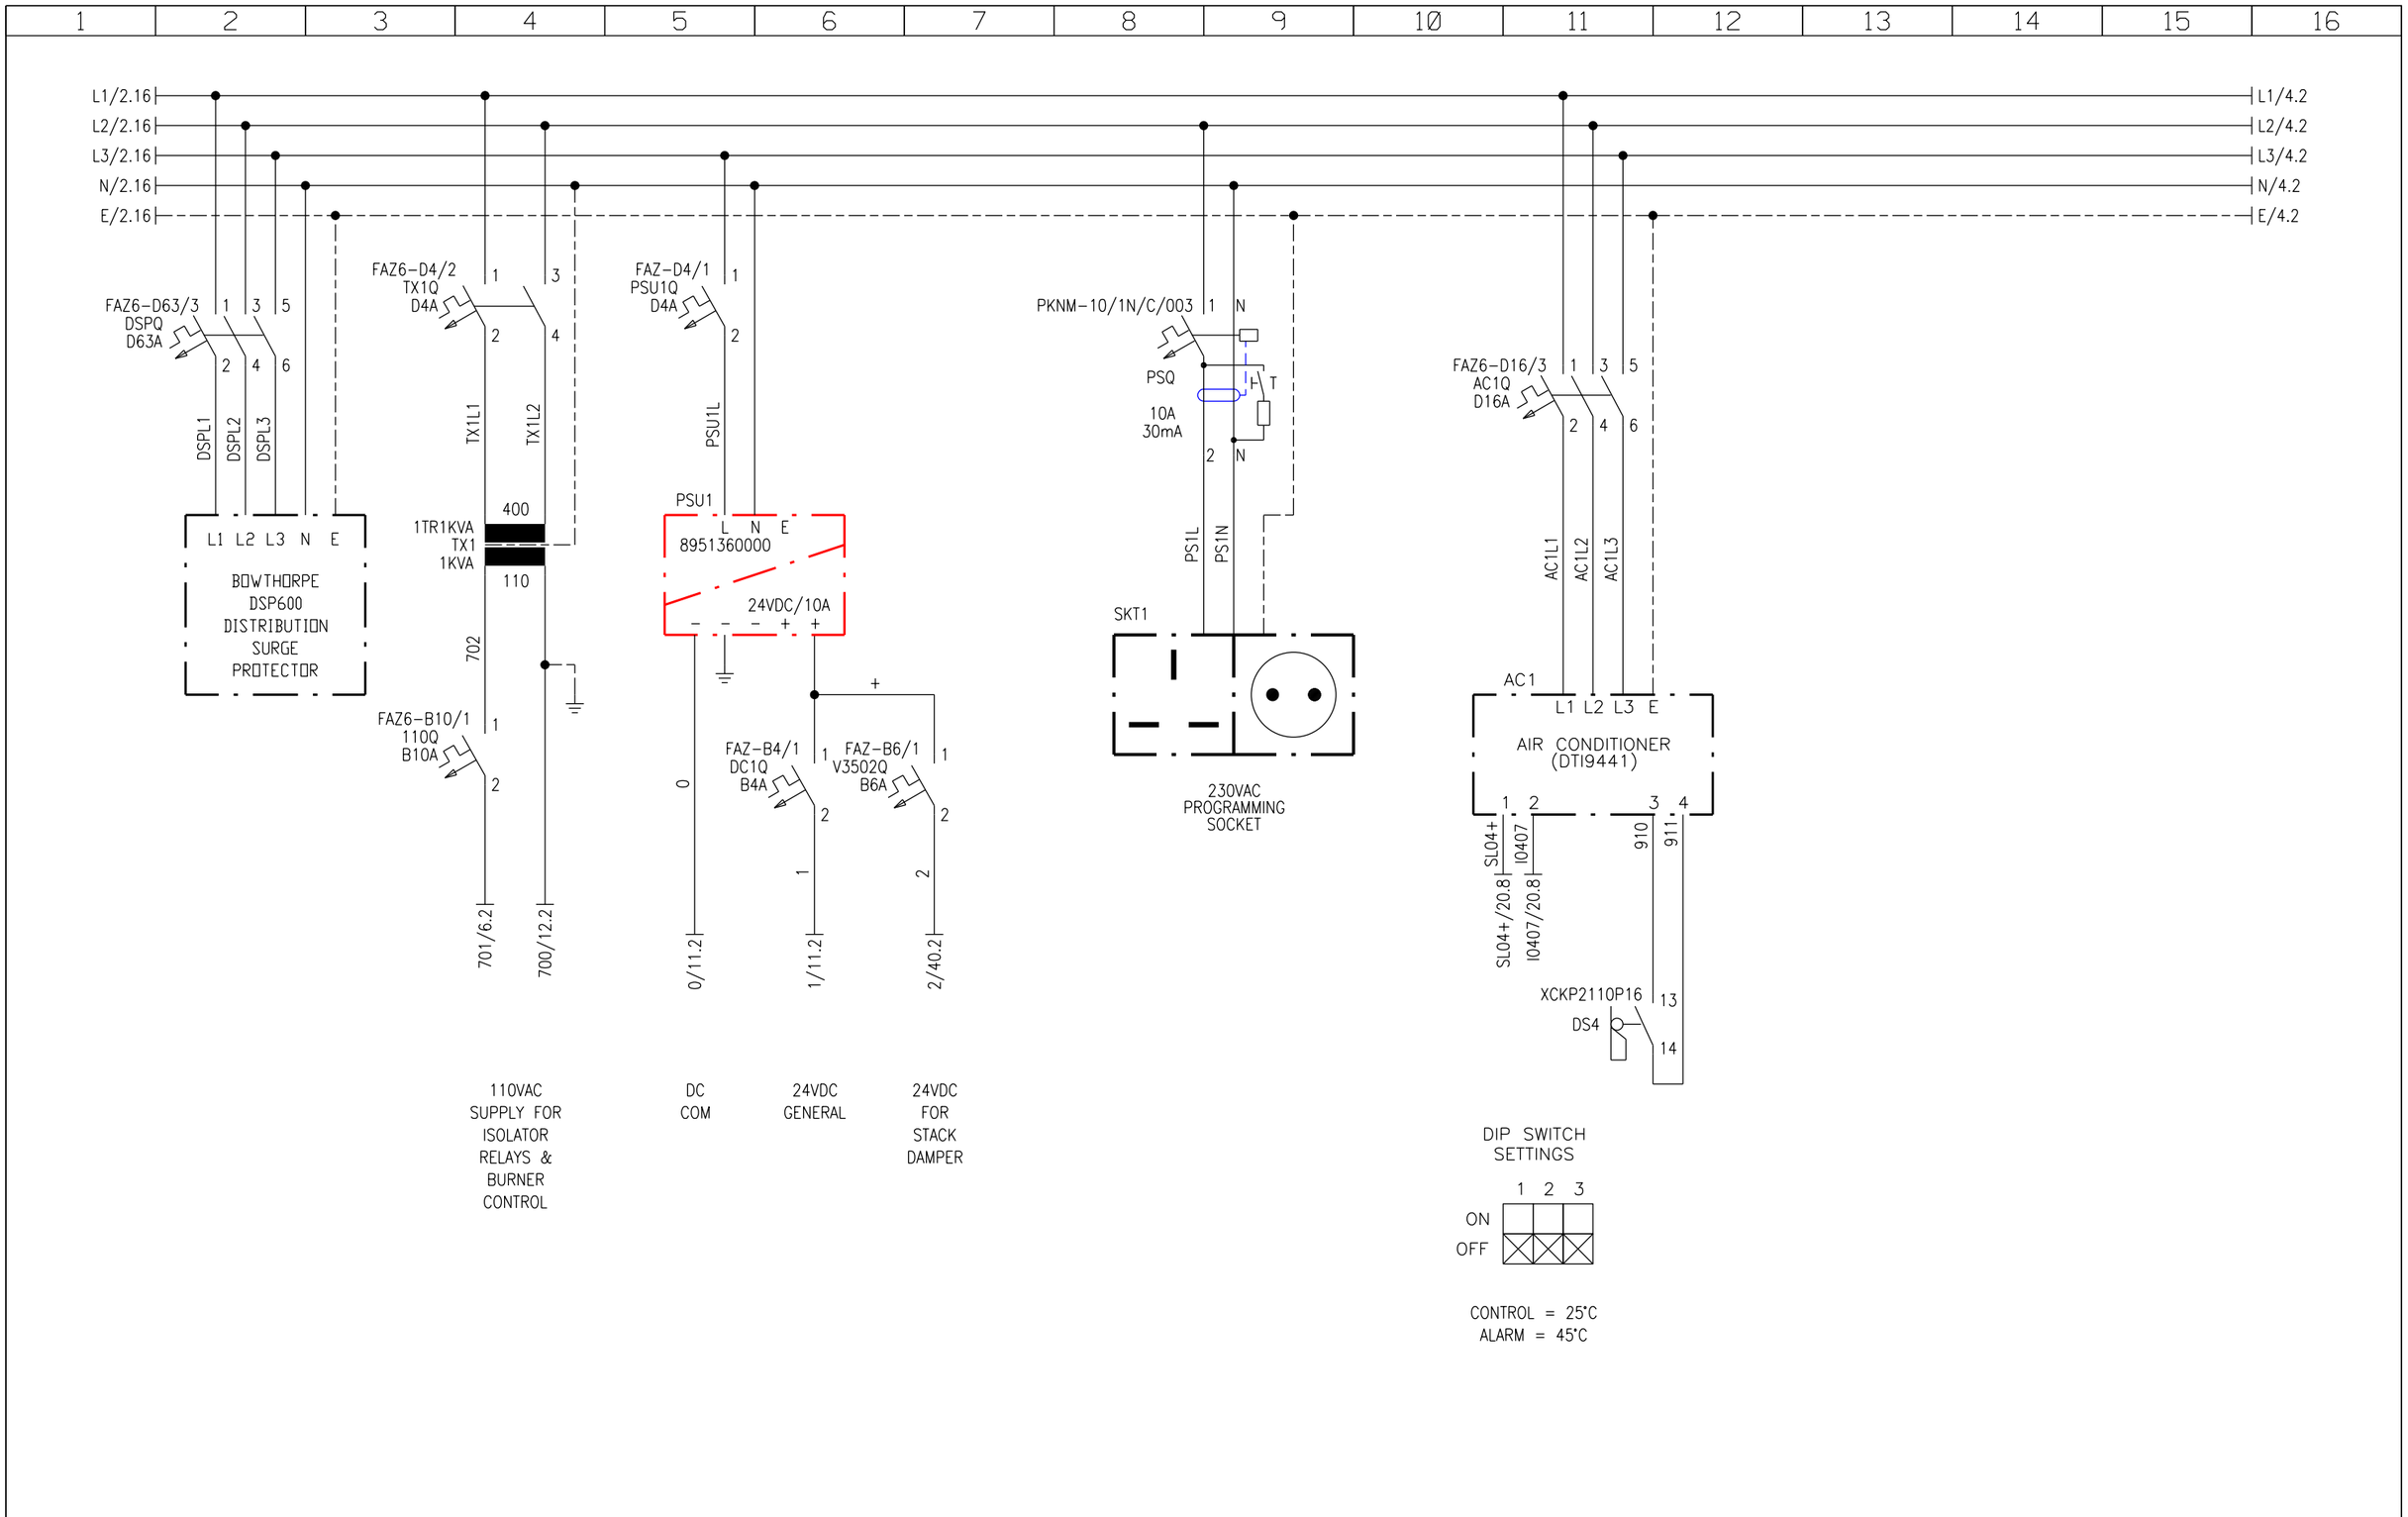

REV	DATE	MODIFICATION	DWN	CHK
1	19/05/14	FOR APPROVAL	MS	DG

ELTEK SYSTEMS Ltd

ELTEK SYSTEMS LTD
ELTEK HOUSE,
NENE VALLEY BUSINESS PARK
OUNDLE, PETERBOROUGH.PE8 4HN
TEL 01832 277590 FAX 01832 273941
Email: info@eltek-systems.com

TITLE

G4 HEATER PANEL
PC32 LINE 4
WSF, LEICESTER

CLIENT

Flo-Mech

FLO-MECH LTD FLO-MECH HOUSE,
PAXTON ROAD, ORTON GOLDHAY
PETERBOROUGH.PE2 5YA, ENGLAND.
TEL +44(0)1733233166
FAX +44(0)1733235200
Email: enquiries@flo-mech.com
Internet: www.flo-mech.com

DATE 19/05/14
DWG NO 5620
SHEET 3 OF 55

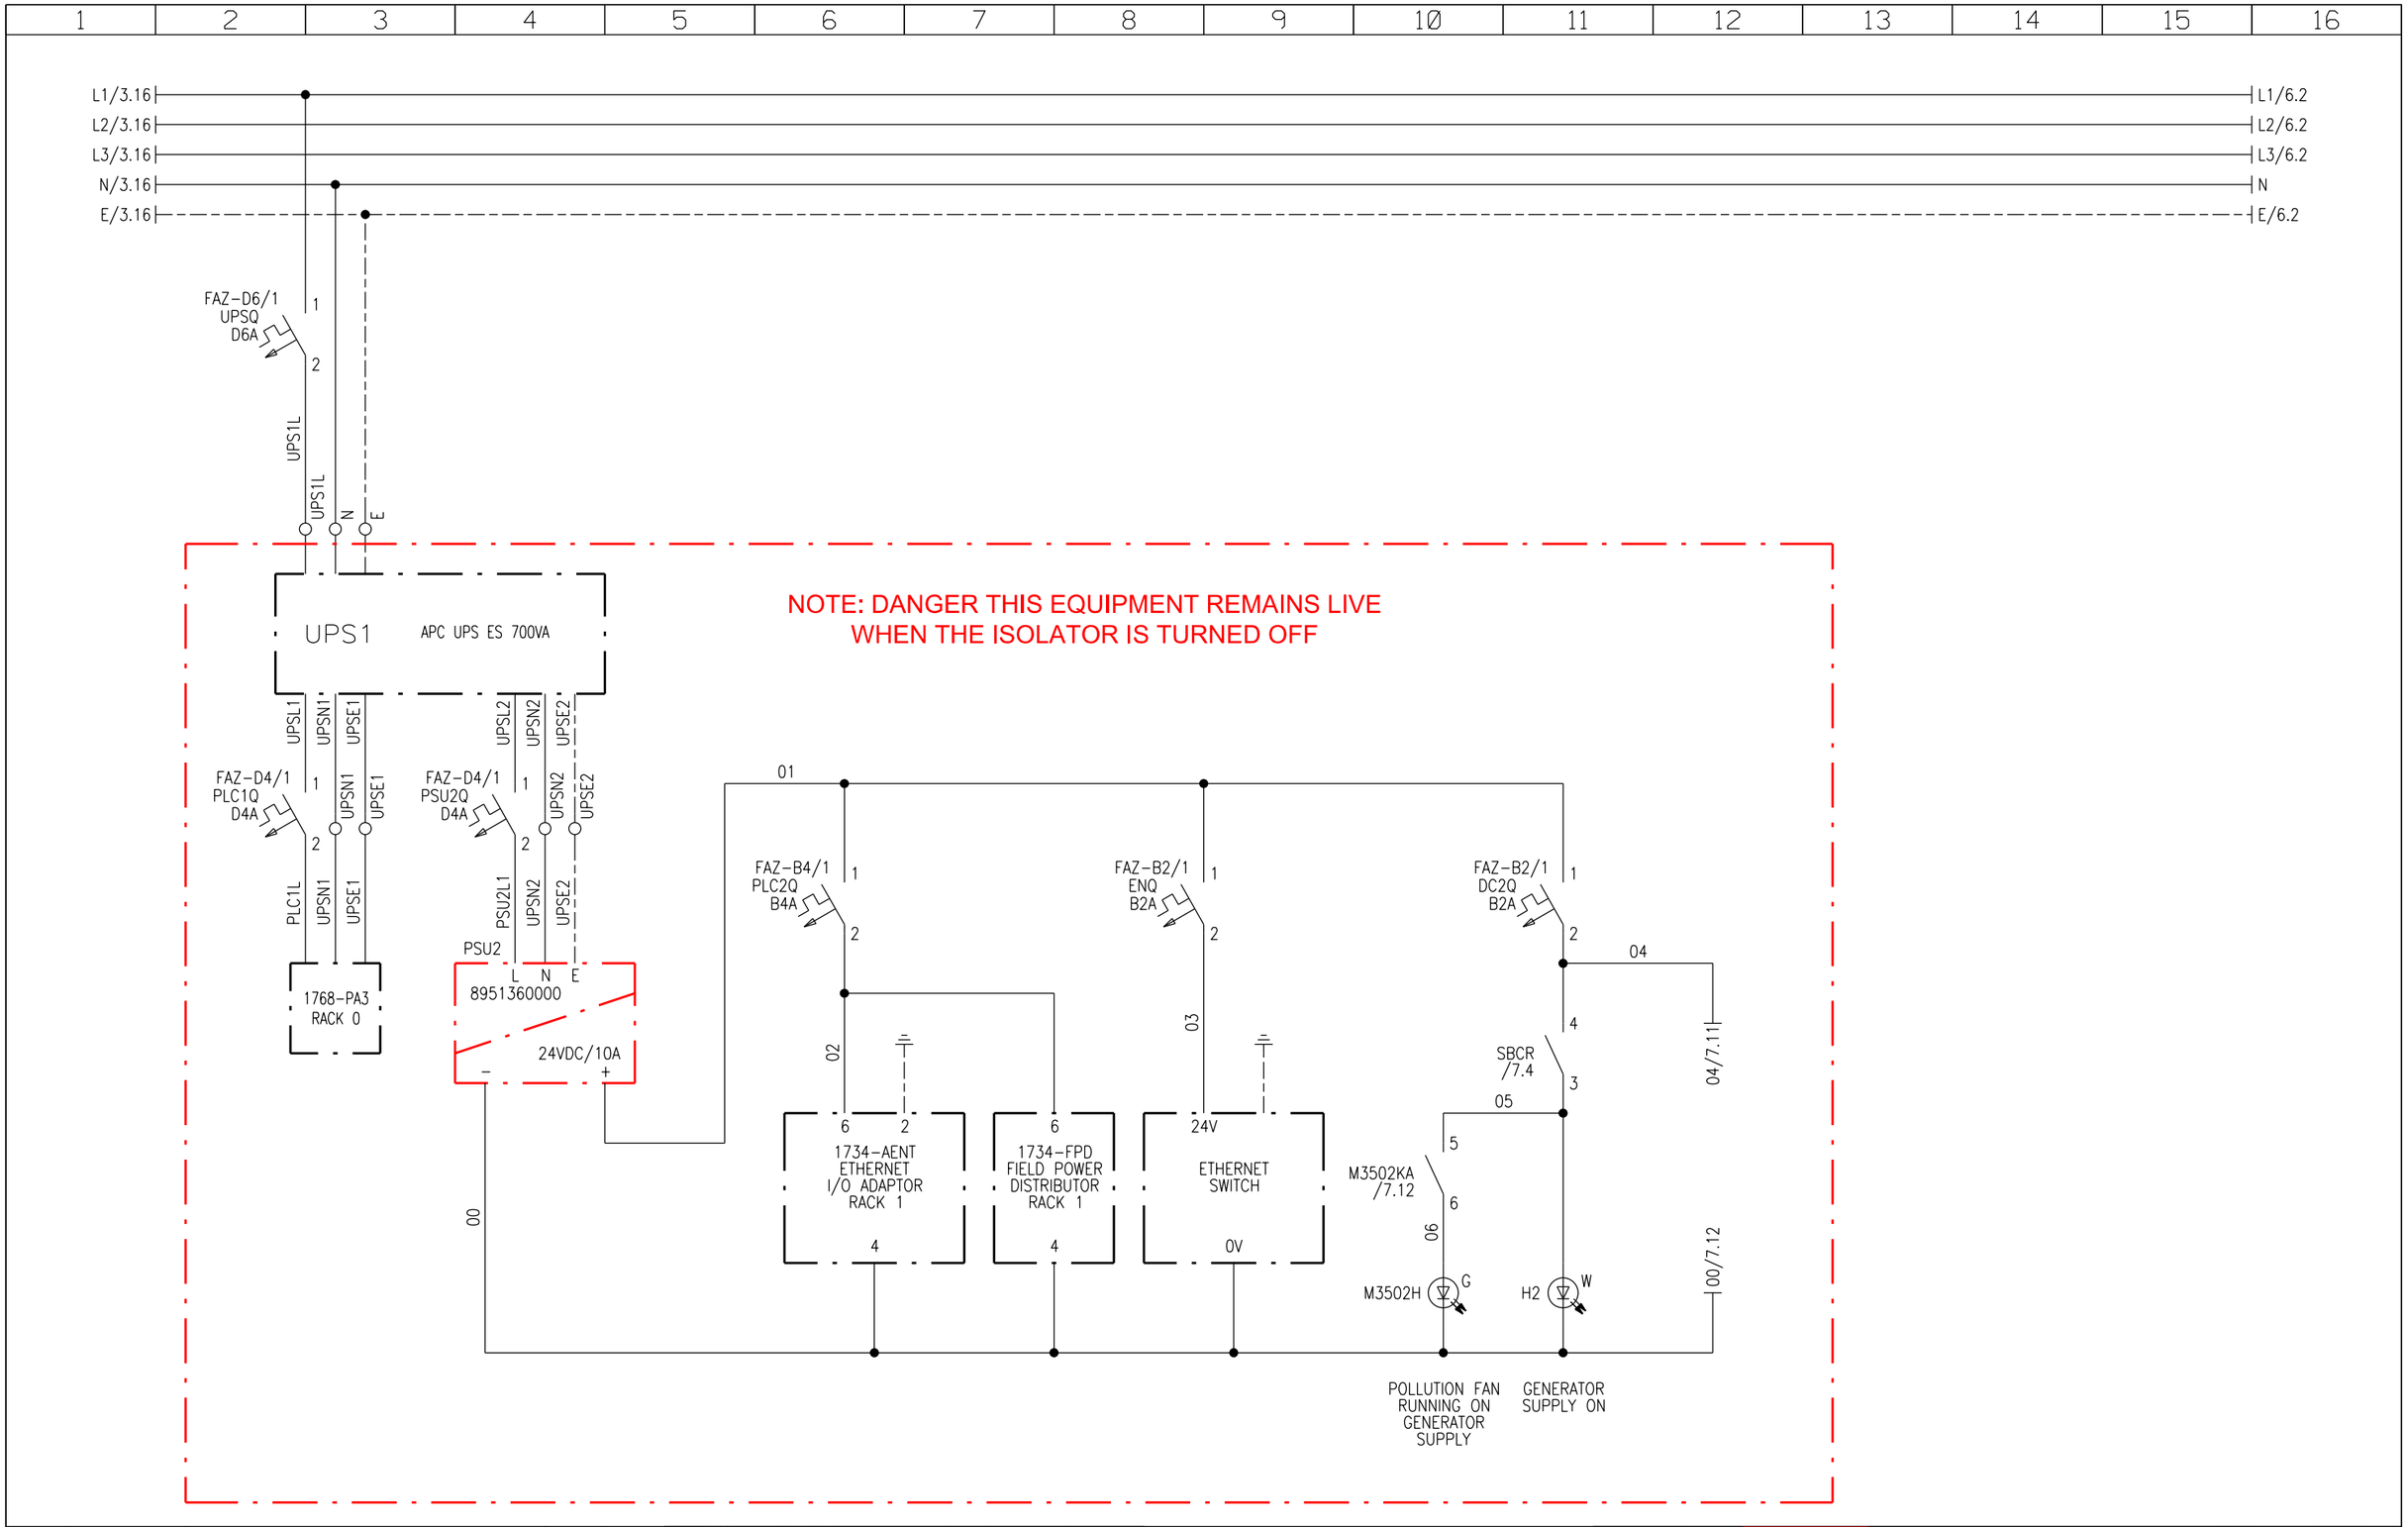

REV	DATE	MODIFICATION	DWN	CHK
1	19/05/14	FOR APPROVAL	MS	DG

ELTEK SYSTEMS LTD
ELTEK HOUSE,
NENE VALLEY BUSINESS PARK
OUNDLE, PETERBOROUGH.PE8 4HN
TEL 01832 277590 FAX 01832 273941
Email: info@eltek-systems.com

TITLE

G4 HEATER PANEL
PC32 LINE 4
WSF, LEICESTER

CLIENT

FLO-MECH LTD FLO-MECH HOUSE,
PAXTON ROAD, ORTON GOLDHAY
PETERBOROUGH.PE2 5YA, ENGLAND.
TEL +44(0)1733233166
FAX +44(0)1733235200
Email: enquiries@flo-mech.com
Internet: www.flo-mech.com

DATE 19/05/14
DWG NO 5620
SHEET 4 OF 55

1	2	3	4	5	6	7	8	9	10	11	12	13	14	15	16

THIS SHEET IS LEFT BLANK INTENTIONALLY

REV	DATE	MODIFICATION	DWN	CHK
1	19/05/14	FOR APPROVAL	MS	DG

ELTEK SYSTEMS Ltd

ELTEK SYSTEMS LTD
ELTEK HOUSE,
NENE VALLEY BUSINESS PARK
OUNDLE, PETERBOROUGH.PE8 4HN
TEL 01832 277590 FAX 01832 273941
Email: info@eltek-systems.com

TITLE

G4 HEATER PANEL
PC32 LINE 4
WSF, LEICESTER

CLIENT

Flo~Mech

FLO-MECH LTD FLO-MECH HOUSE,
PAXTON ROAD, ORTON GOLDHAY
PETERBOROUGH.PE2 5YA, ENGLAND.
TEL +44(0)1733233166
FAX +44(0)1733235200
Email: enquiries@flo-mech.com
Internet: www.flo-mech.com

DATE 19/05/14
DWG NO 5620
SHEET 5 OF 55

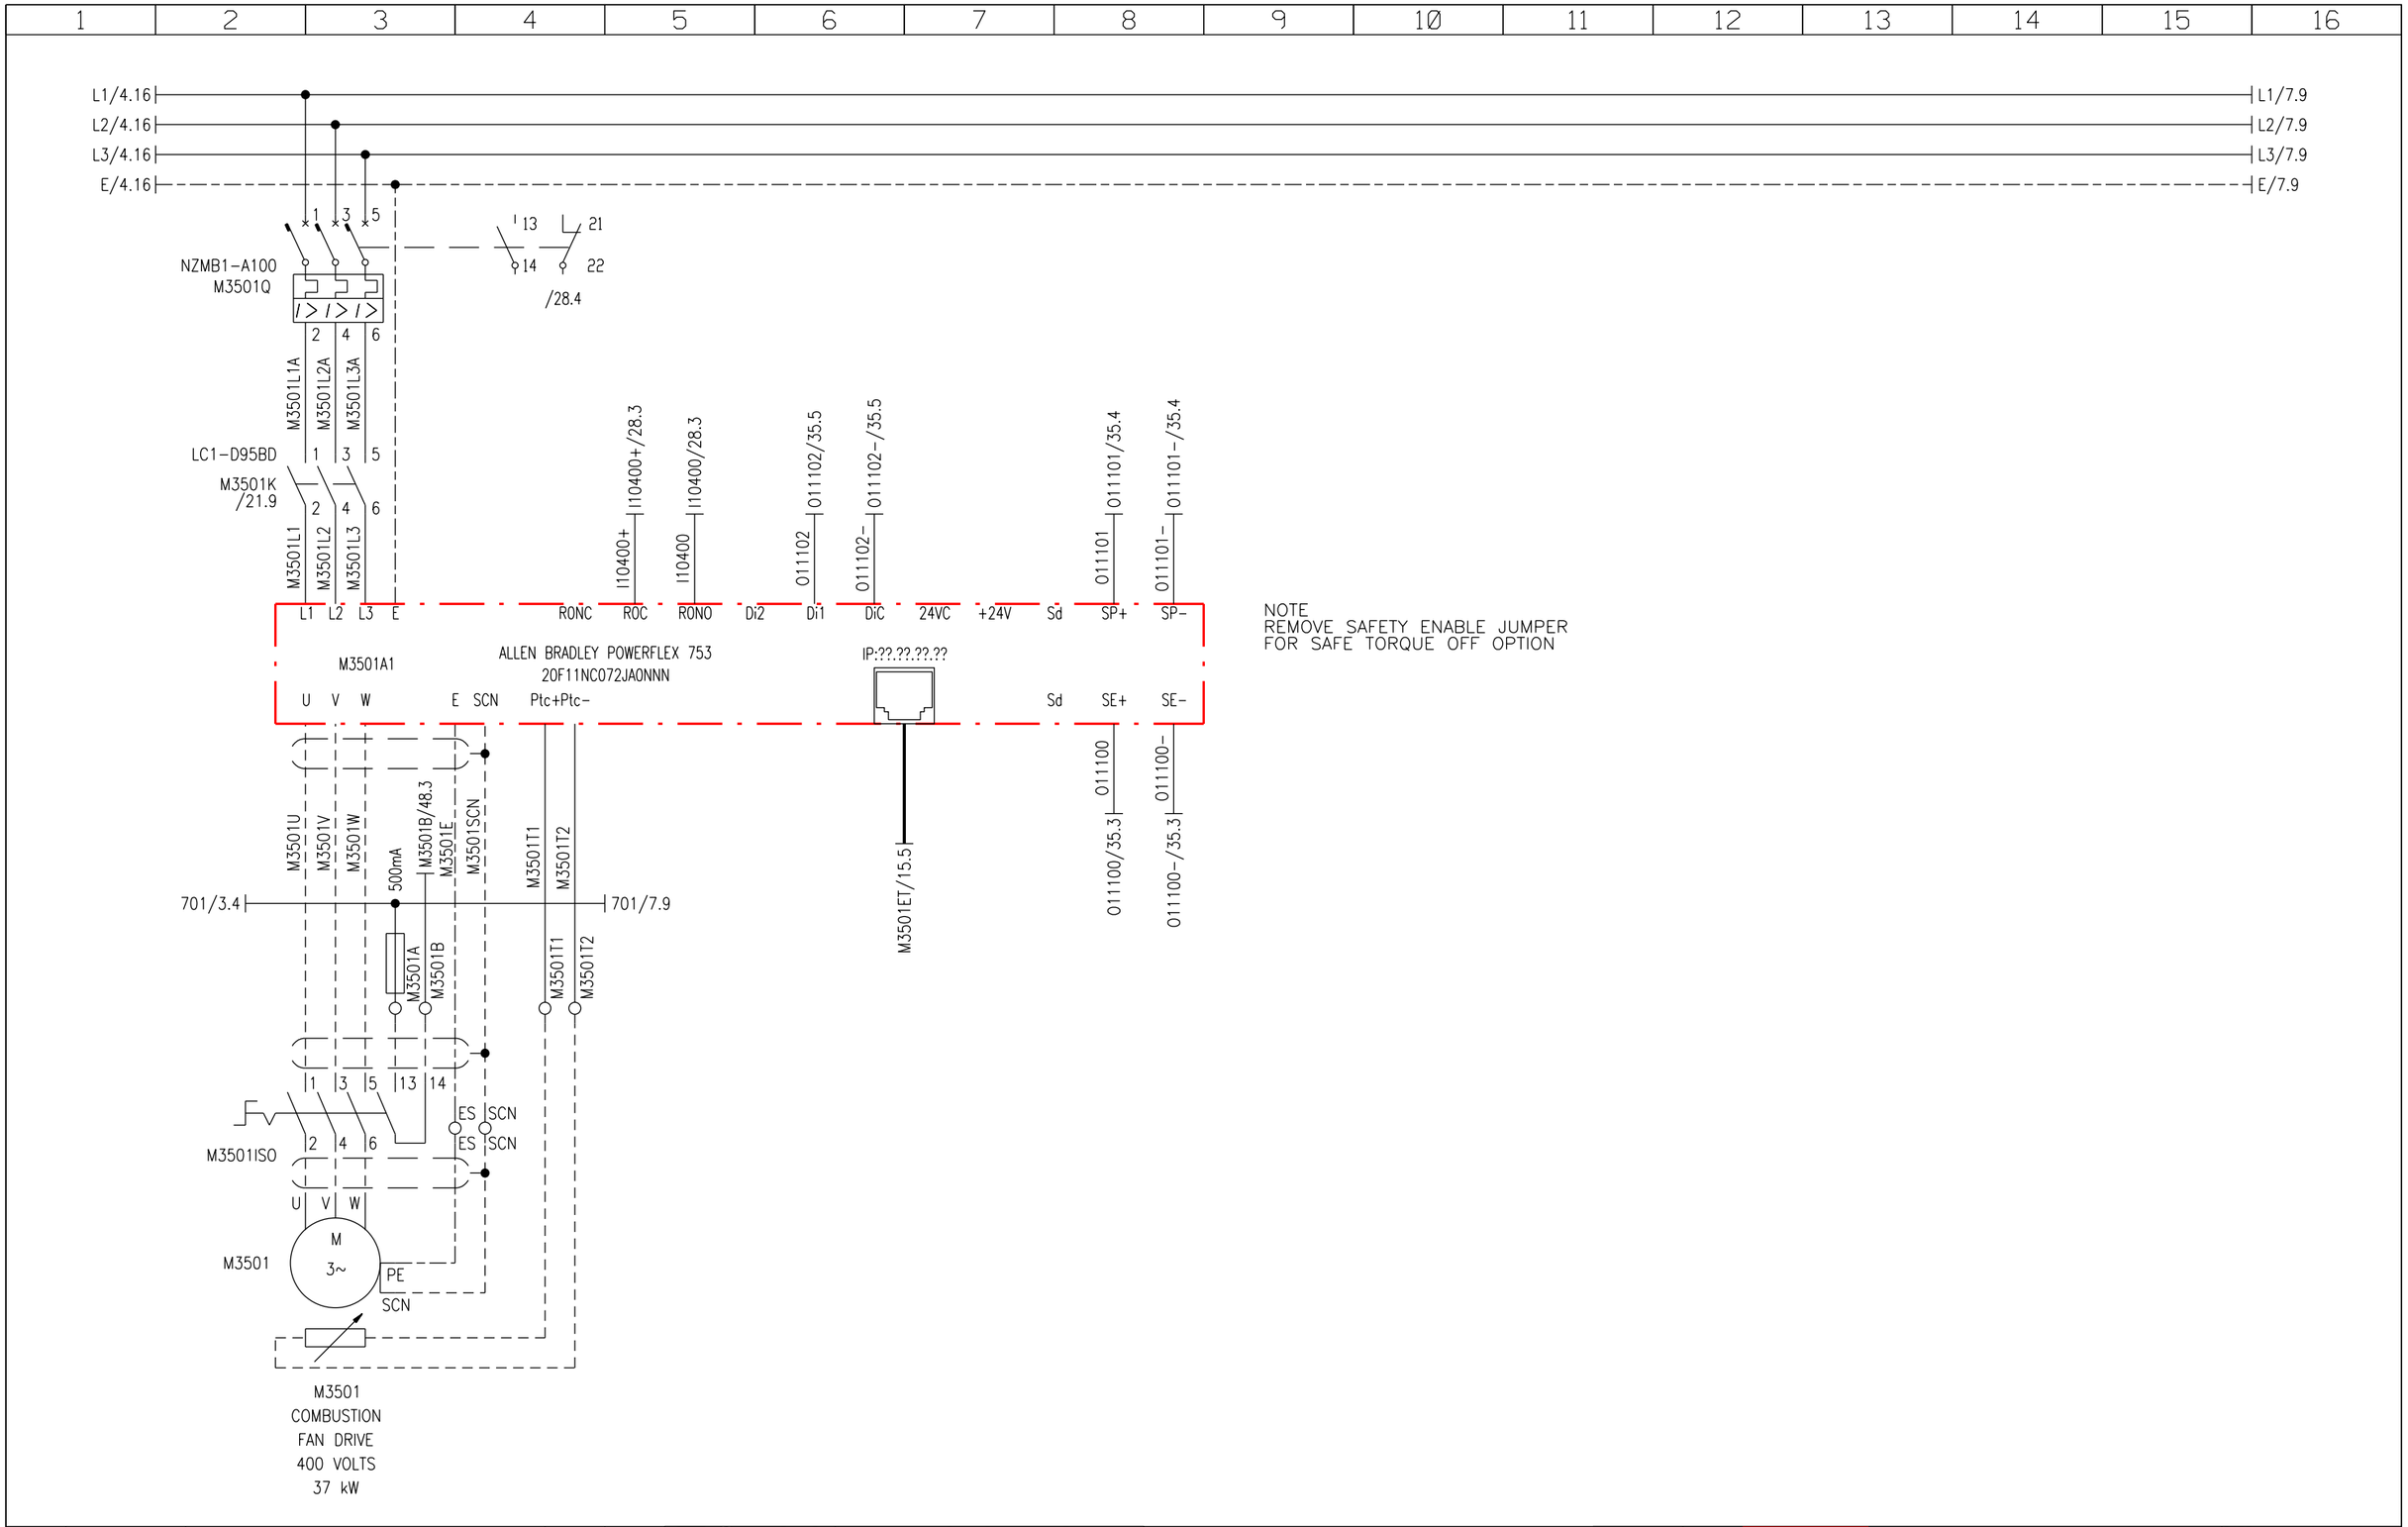

NOTE
REMOVE SAFETY ENABLE JUMPER
FOR SAFE TORQUE OFF OPTION

REV	DATE	MODIFICATION	DWN	CHK
1	19/05/14	FOR APPROVAL	MS	DG

ELTEK SYSTEMS Ltd

ELTEK SYSTEMS LTD
ELTEK HOUSE,
NENE VALLEY BUSINESS PARK
OUNDLE, PETERBOROUGH.PE8 4HN
TEL 01832 277590 FAX 01832 273941
Email: info@eltek-systems.com

TITLE

G4 HEATER PANEL
PC32 LINE 4
WSF, LEICESTER

CLIENT

Flo~Mech

FLO-MECH LTD FLO-MECH HOUSE,
PAXTON ROAD, ORTON GOLDHAY
PETERBOROUGH.PE2 5YA, ENGLAND.
TEL +44(0)1733233166
FAX +44(0)1733235200
Email: enquiries@flo-mech.com
Internet: www.flo-mech.com

DATE 19/05/14
DWG NO 5620
SHEET 6 OF 55

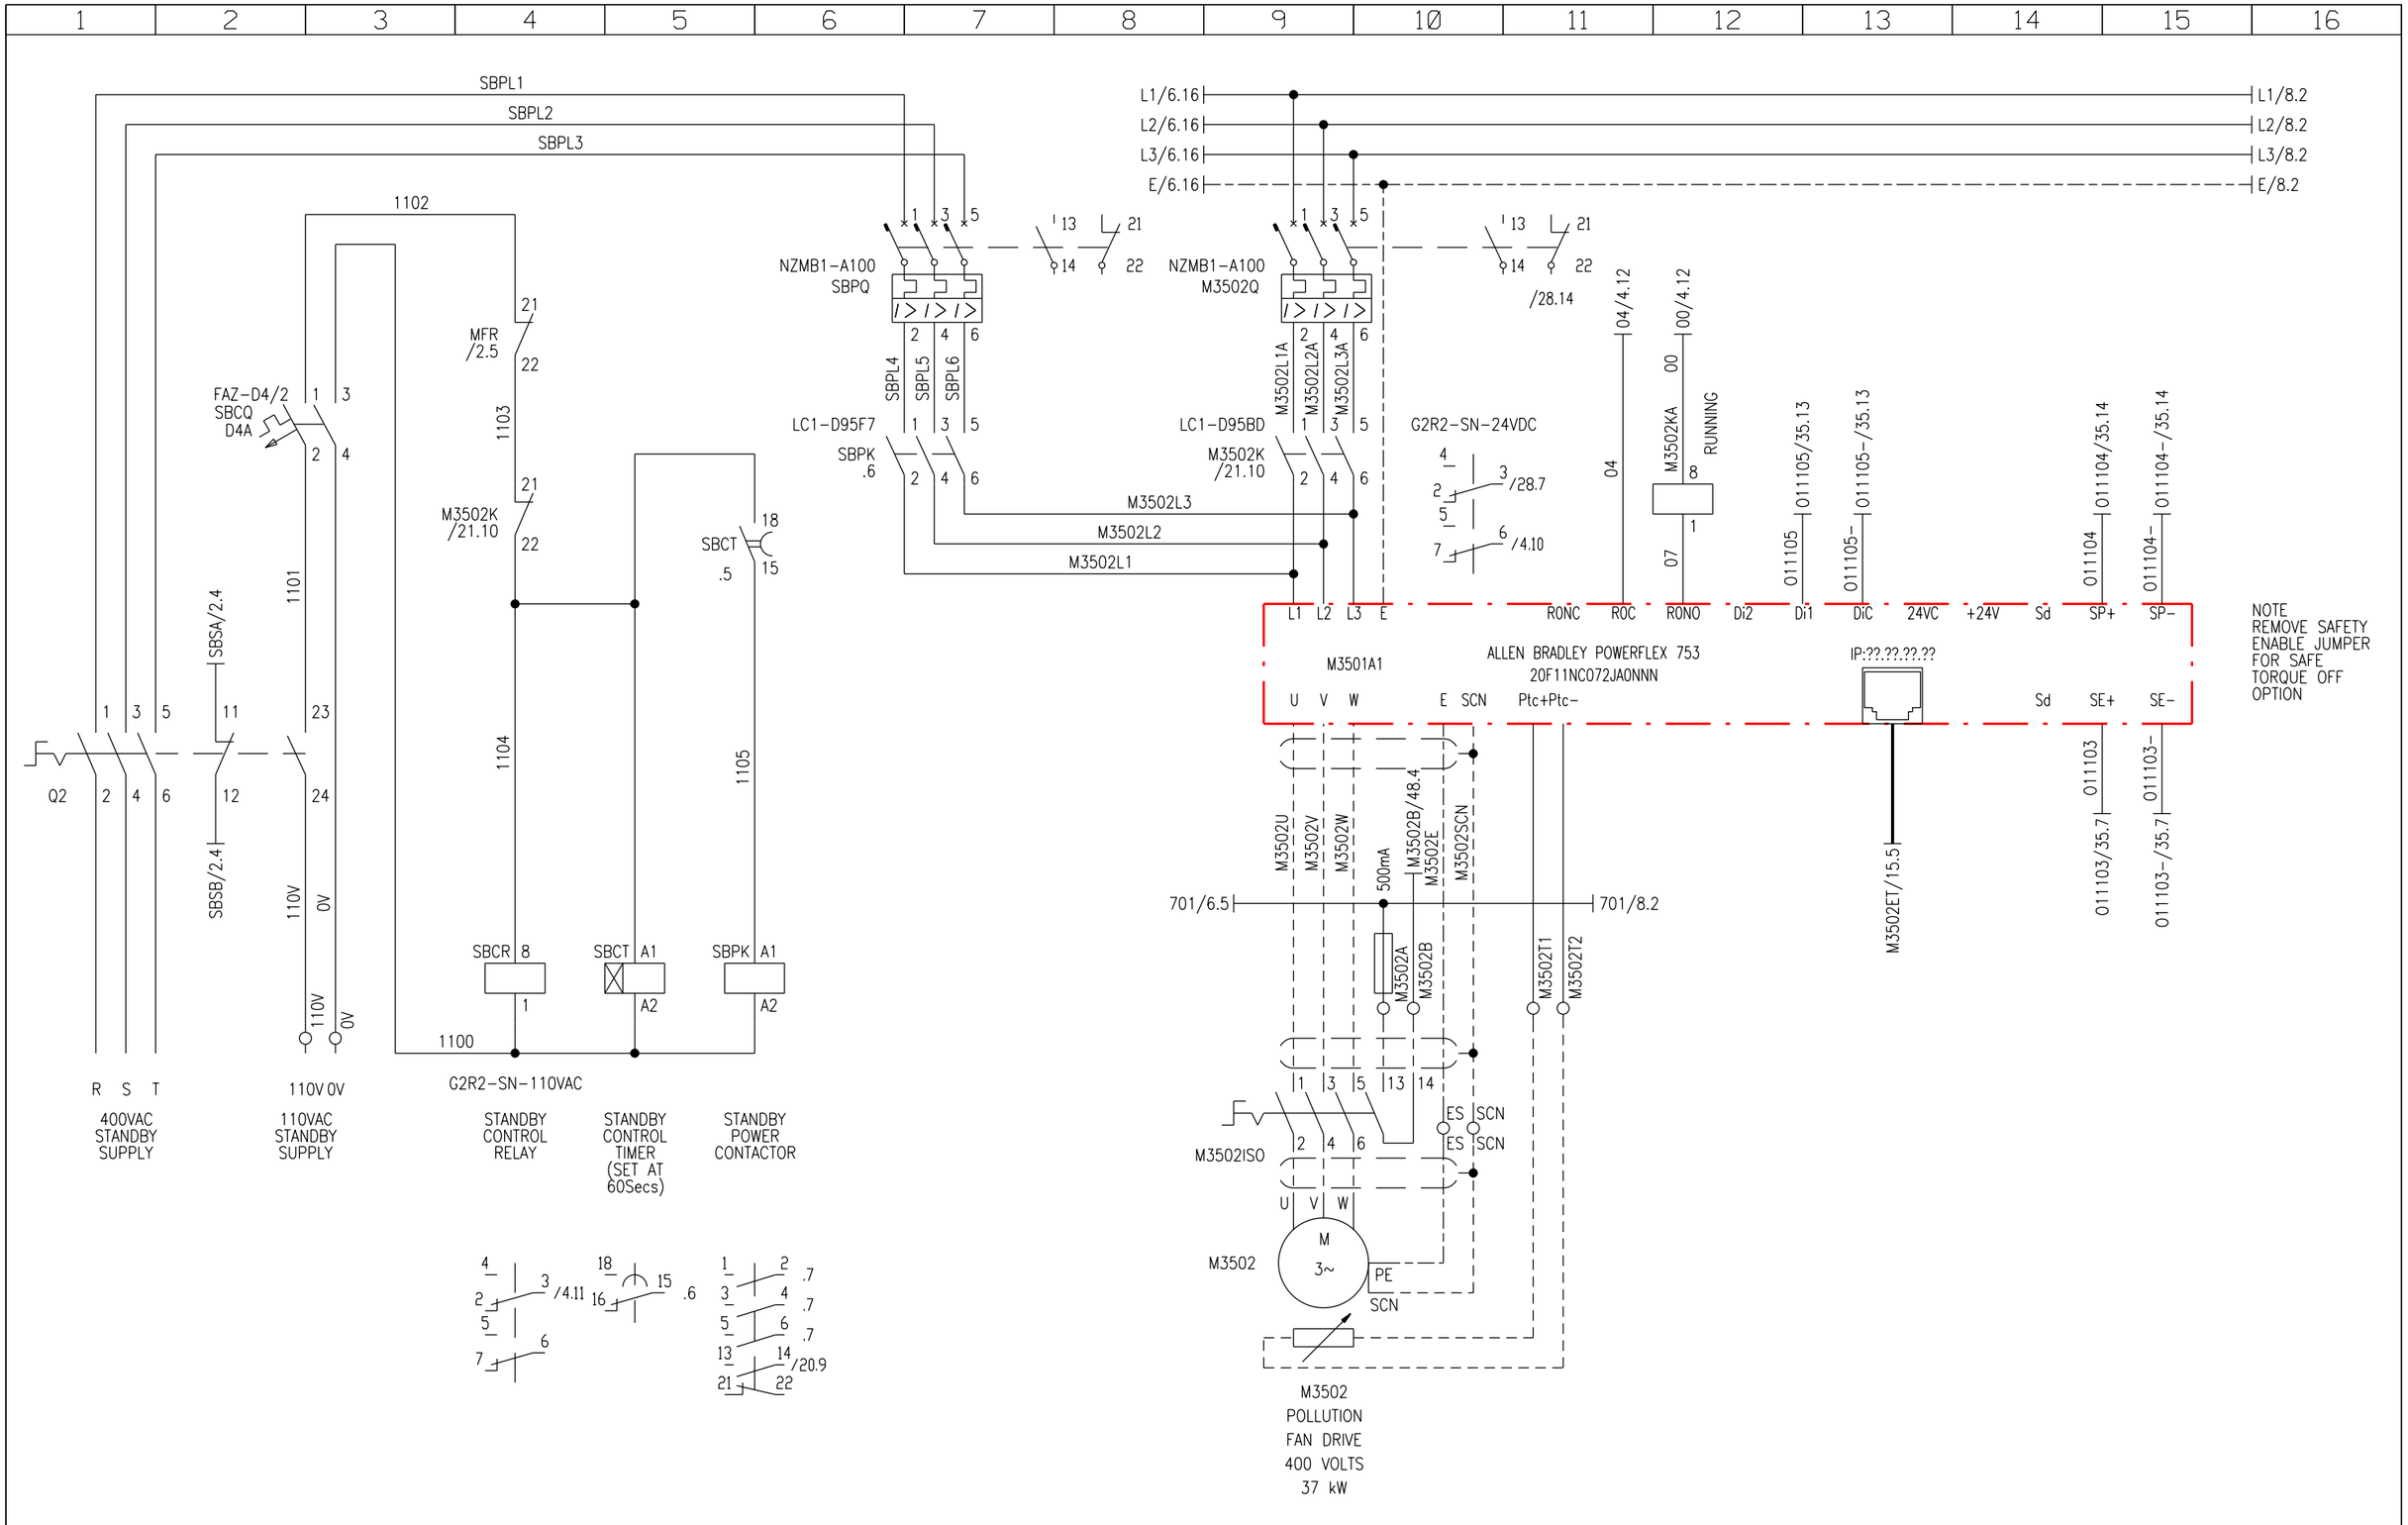

REV	DATE	MODIFICATION	DWN	CHK
1	19/05/14	FOR APPROVAL	MS	DG

ELTEK SYSTEMS LTD
ELTEK HOUSE,
NENE VALLEY BUSINESS PARK
OUNDLE, PETERBOROUGH.PE8 4HN
TEL 01832 277590 FAX 01832 273941
Email: info@eltek-systems.com

TITLE

G4 HEATER PANEL
PC32 LINE 4
WSF, LEICESTER

CLIENT

Flo~Mech

FLO-MECH LTD FLO-MECH HOUSE,
PAXTON ROAD, ORTON GOLDHAY
PETERBOROUGH.PE2 5YA, ENGLAND.
TEL +44(0)1733233166
FAX +44(0)1733235200
Email: enquiries@flo-mech.com
Internet: www.flo-mech.com

DATE 19/05/14
DWG NO 5620
SHEET 7 OF 55

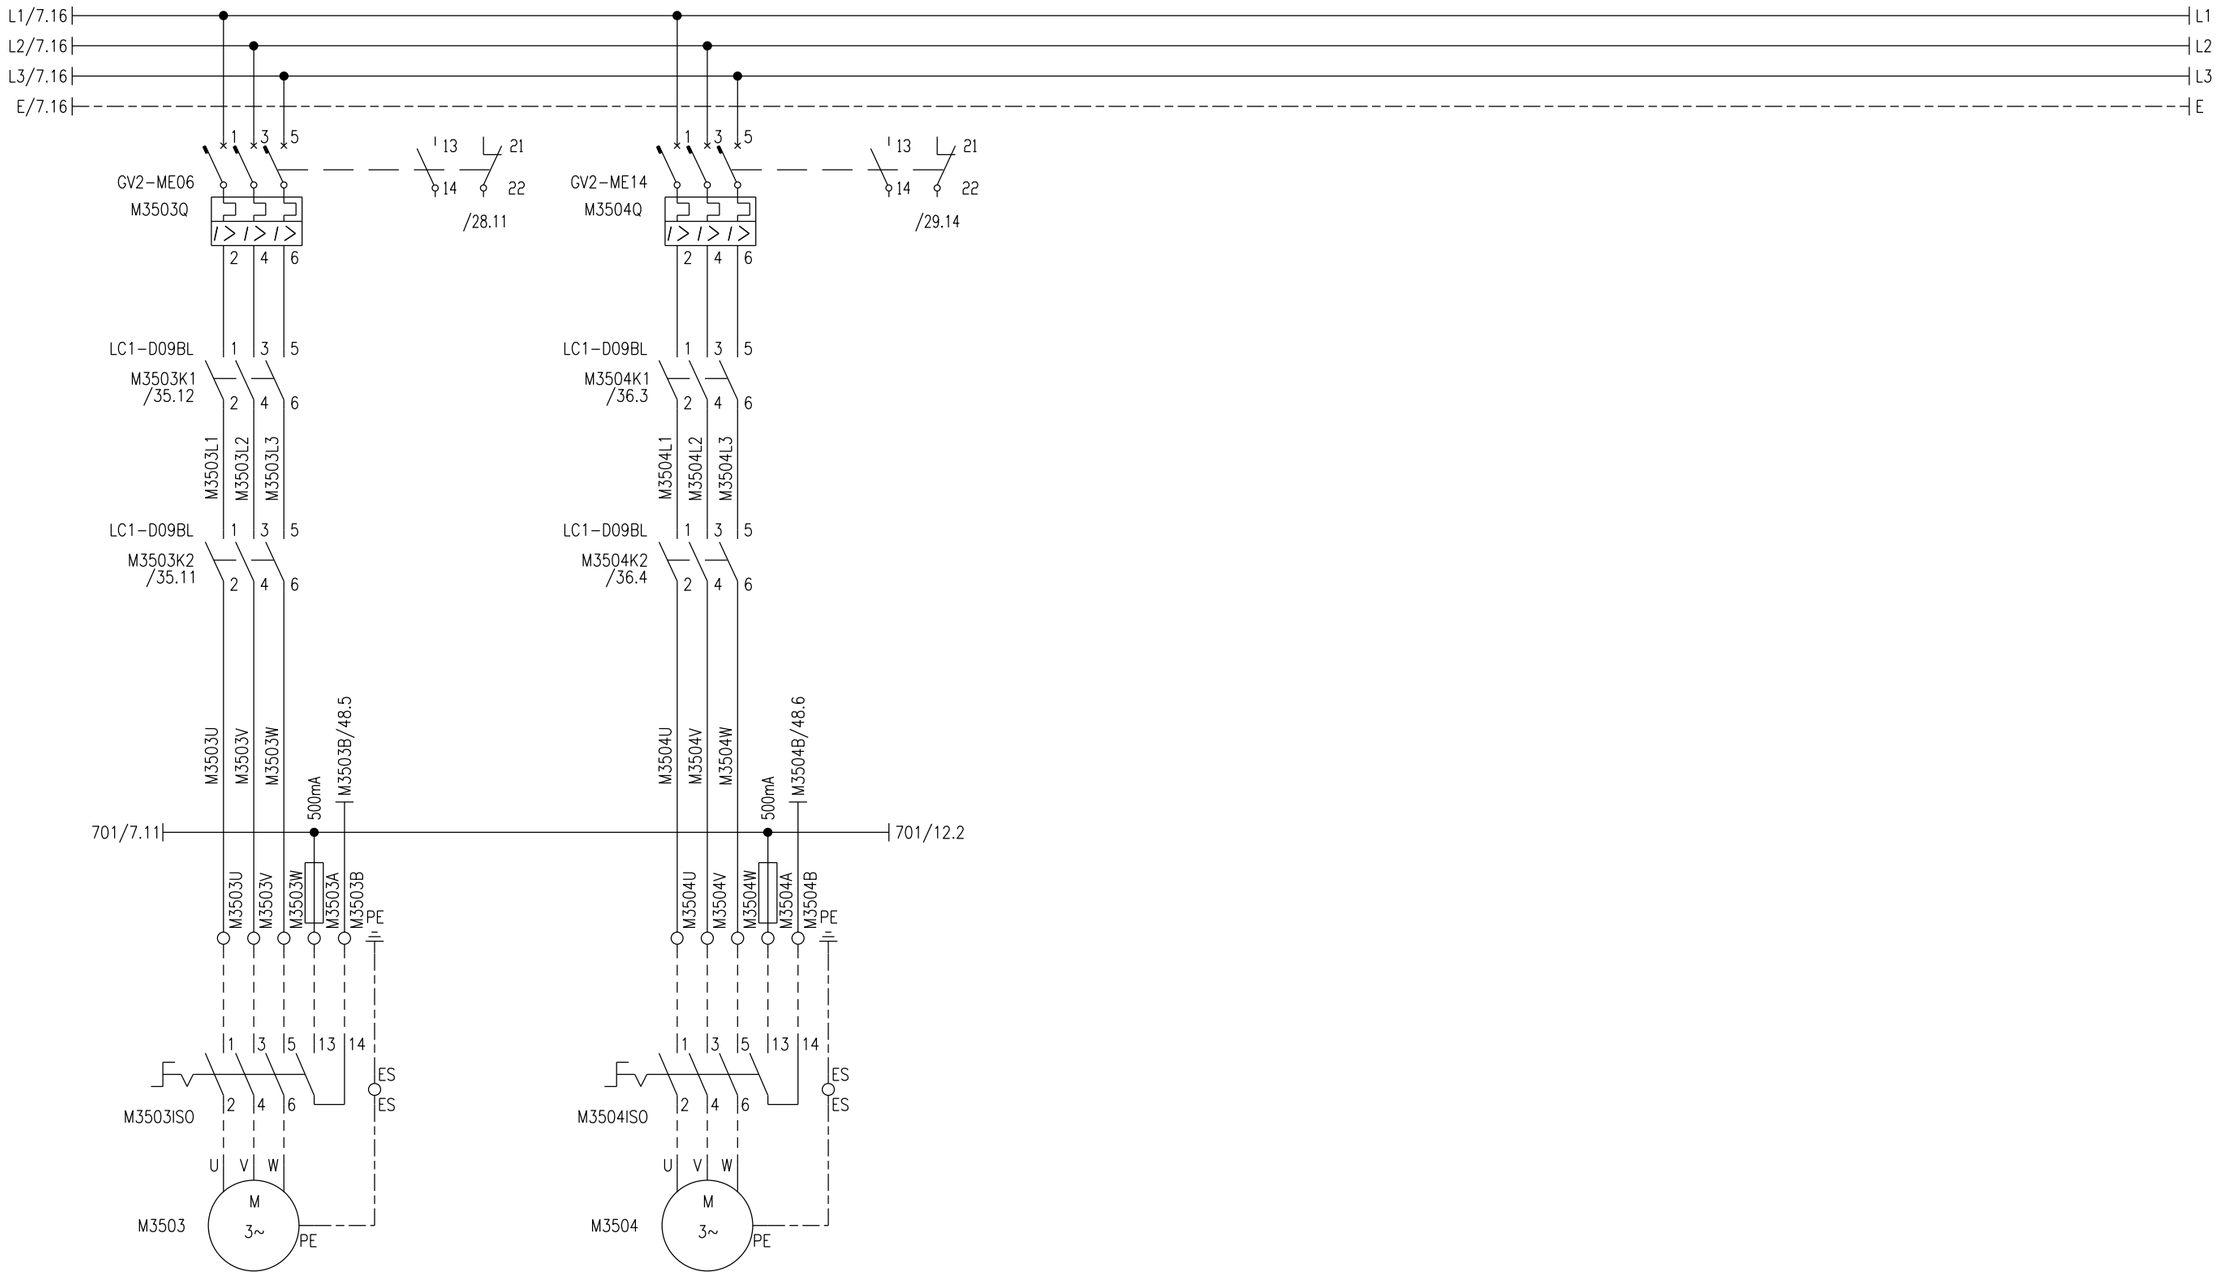

M3503
FLAME SENSOR
COOLING FAN
400 VOLTS
0.37 kW
1A FLC

M3504
DIESEL
FUEL PUMP
400 VOLTS
2.2 kW
4.49A FLC

REV	DATE	MODIFICATION	DWN	CHK
1	19/05/14	FOR APPROVAL	MS	DG

ELTEK SYSTEMS Ltd

ELTEK SYSTEMS LTD
ELTEK HOUSE,
NENE VALLEY BUSINESS PARK
OUNDLE, PETERBOROUGH.PE8 4HN
TEL 01832 277590 FAX 01832 273941
Email: info@eltek-systems.com

TITLE

G4 HEATER PANEL
PC32 LINE 4
WSF, LEICESTER

CLIENT

Flo~Mech

FLO-MECH LTD FLO-MECH HOUSE,
PAXTON ROAD, ORTON GOLDHAY
PETERBOROUGH.PE2 5YA, ENGLAND.
TEL +44(0)1733233166
FAX +44(0)1733235200
Email: enquiries@flo-mech.com
Internet: www.flo-mech.com

DATE 19/05/14
DWG NO 5620
SHEET 8 OF 55

1	2	3	4	5	6	7	8	9	10	11	12	13	14	15	16

THIS SHEET IS LEFT BLANK INTENTIONALLY

REV	DATE	MODIFICATION	DWN	CHK
1	19/05/14	FOR APPROVAL	MS	DG

ELTEK SYSTEMS Ltd

ELTEK SYSTEMS LTD
ELTEK HOUSE,
NENE VALLEY BUSINESS PARK
OUNDLE, PETERBOROUGH.PE8 4HN
TEL 01832 277590 FAX 01832 273941
Email: info@eltek-systems.com

TITLE

G4 HEATER PANEL
PC32 LINE 4
WSF, LEICESTER

CLIENT

Flo~Mech

FLO-MECH LTD FLO-MECH HOUSE,
PAXTON ROAD, ORTON GOLDHAY
PETERBOROUGH.PE2 5YA, ENGLAND.
TEL +44(0)1733233166
FAX +44(0)1733235200
Email: enquiries@flo-mech.com
Internet: www.flo-mech.com

DATE 19/05/14
DWG NO 5620
SHEET 9 OF 55

1	2	3	4	5	6	7	8	9	10	11	12	13	14	15	16

THIS SHEET IS LEFT BLANK INTENTIONALLY

REV	DATE	MODIFICATION	DWN	CHK
1	19/05/14	FOR APPROVAL	MS	DG

ELTEK SYSTEMS Ltd

ELTEK SYSTEMS LTD
ELTEK HOUSE,
NENE VALLEY BUSINESS PARK
OUNDLE, PETERBOROUGH.PE8 4HN
TEL 01832 277590 FAX 01832 273941
Email: info@eltek-systems.com

TITLE

G4 HEATER PANEL
PC32 LINE 4
WSF, LEICESTER

CLIENT

Flo~Mech

FLO-MECH LTD FLO-MECH HOUSE,
PAXTON ROAD, ORTON GOLDHAY
PETERBOROUGH.PE2 5YA, ENGLAND.
TEL +44(0)1733233166
FAX +44(0)1733235200
Email: enquiries@flo-mech.com
Internet: www.flo-mech.com

DATE 19/05/14
DWG NO 5620
SHEET 10 OF 55

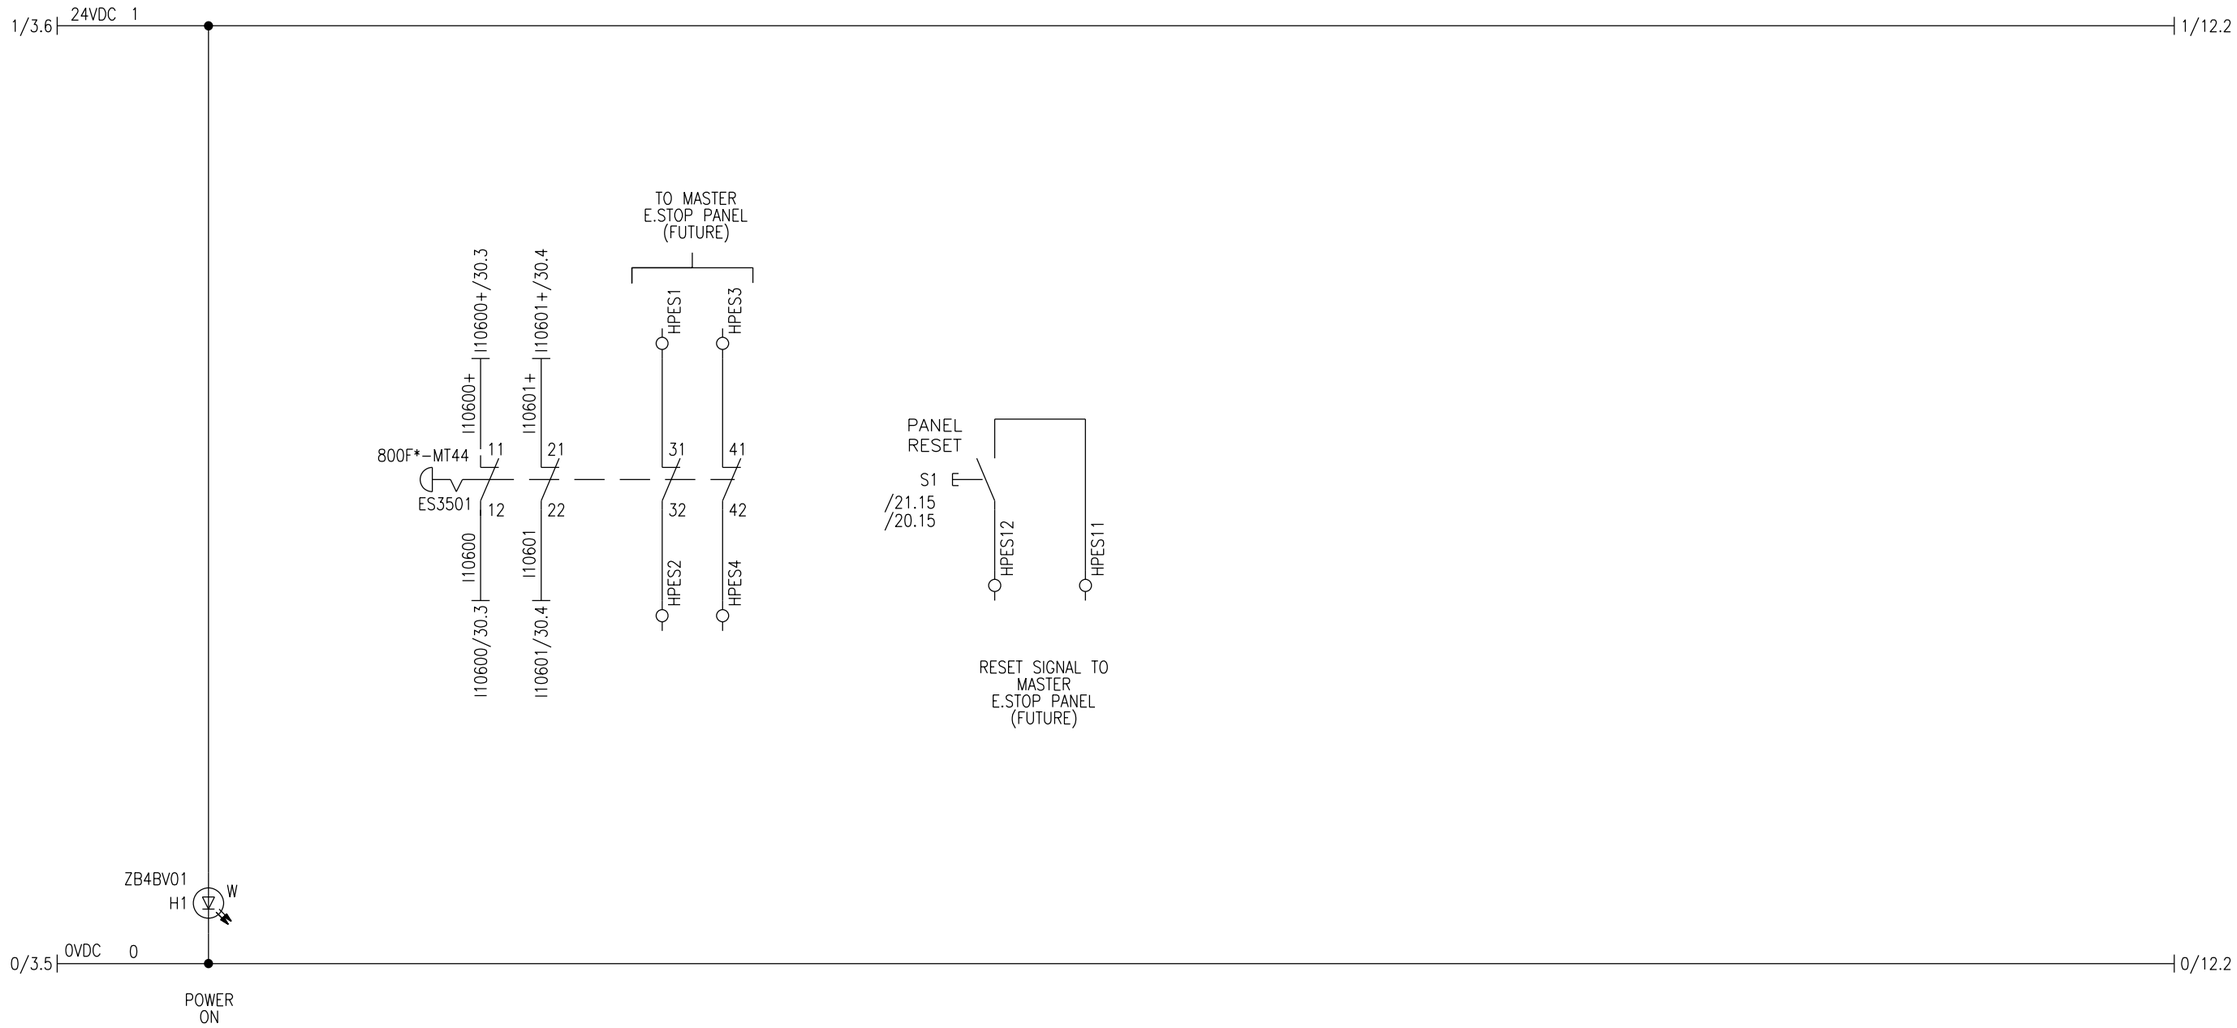

REV	DATE	MODIFICATION	DWN	CHK
1	19/05/14	FOR APPROVAL	MS	DG

ELTEK SYSTEMS Ltd
ELTEK SYSTEMS LTD
ELTEK HOUSE,
NENE VALLEY BUSINESS PARK
OUNDLE, PETERBOROUGH.PE8 4HN
TEL 01832 277590 FAX 01832 273941
Email: info@eltek-systems.com

TITLE

G4 HEATER PANEL
PC32 LINE 4
WSF, LEICESTER

CLIENT

Flo~Mech

FLO-MECH LTD FLO-MECH HOUSE,
PAXTON ROAD, ORTON GOLDHAY
PETERBOROUGH.PE2 5YA, ENGLAND.
TEL +44(0)1733233166
FAX +44(0)1733235200
Email: enquiries@flo-mech.com
Internet: www.flo-mech.com

DATE 19/05/14
DWG NO 5620
SHEET 11 OF 55

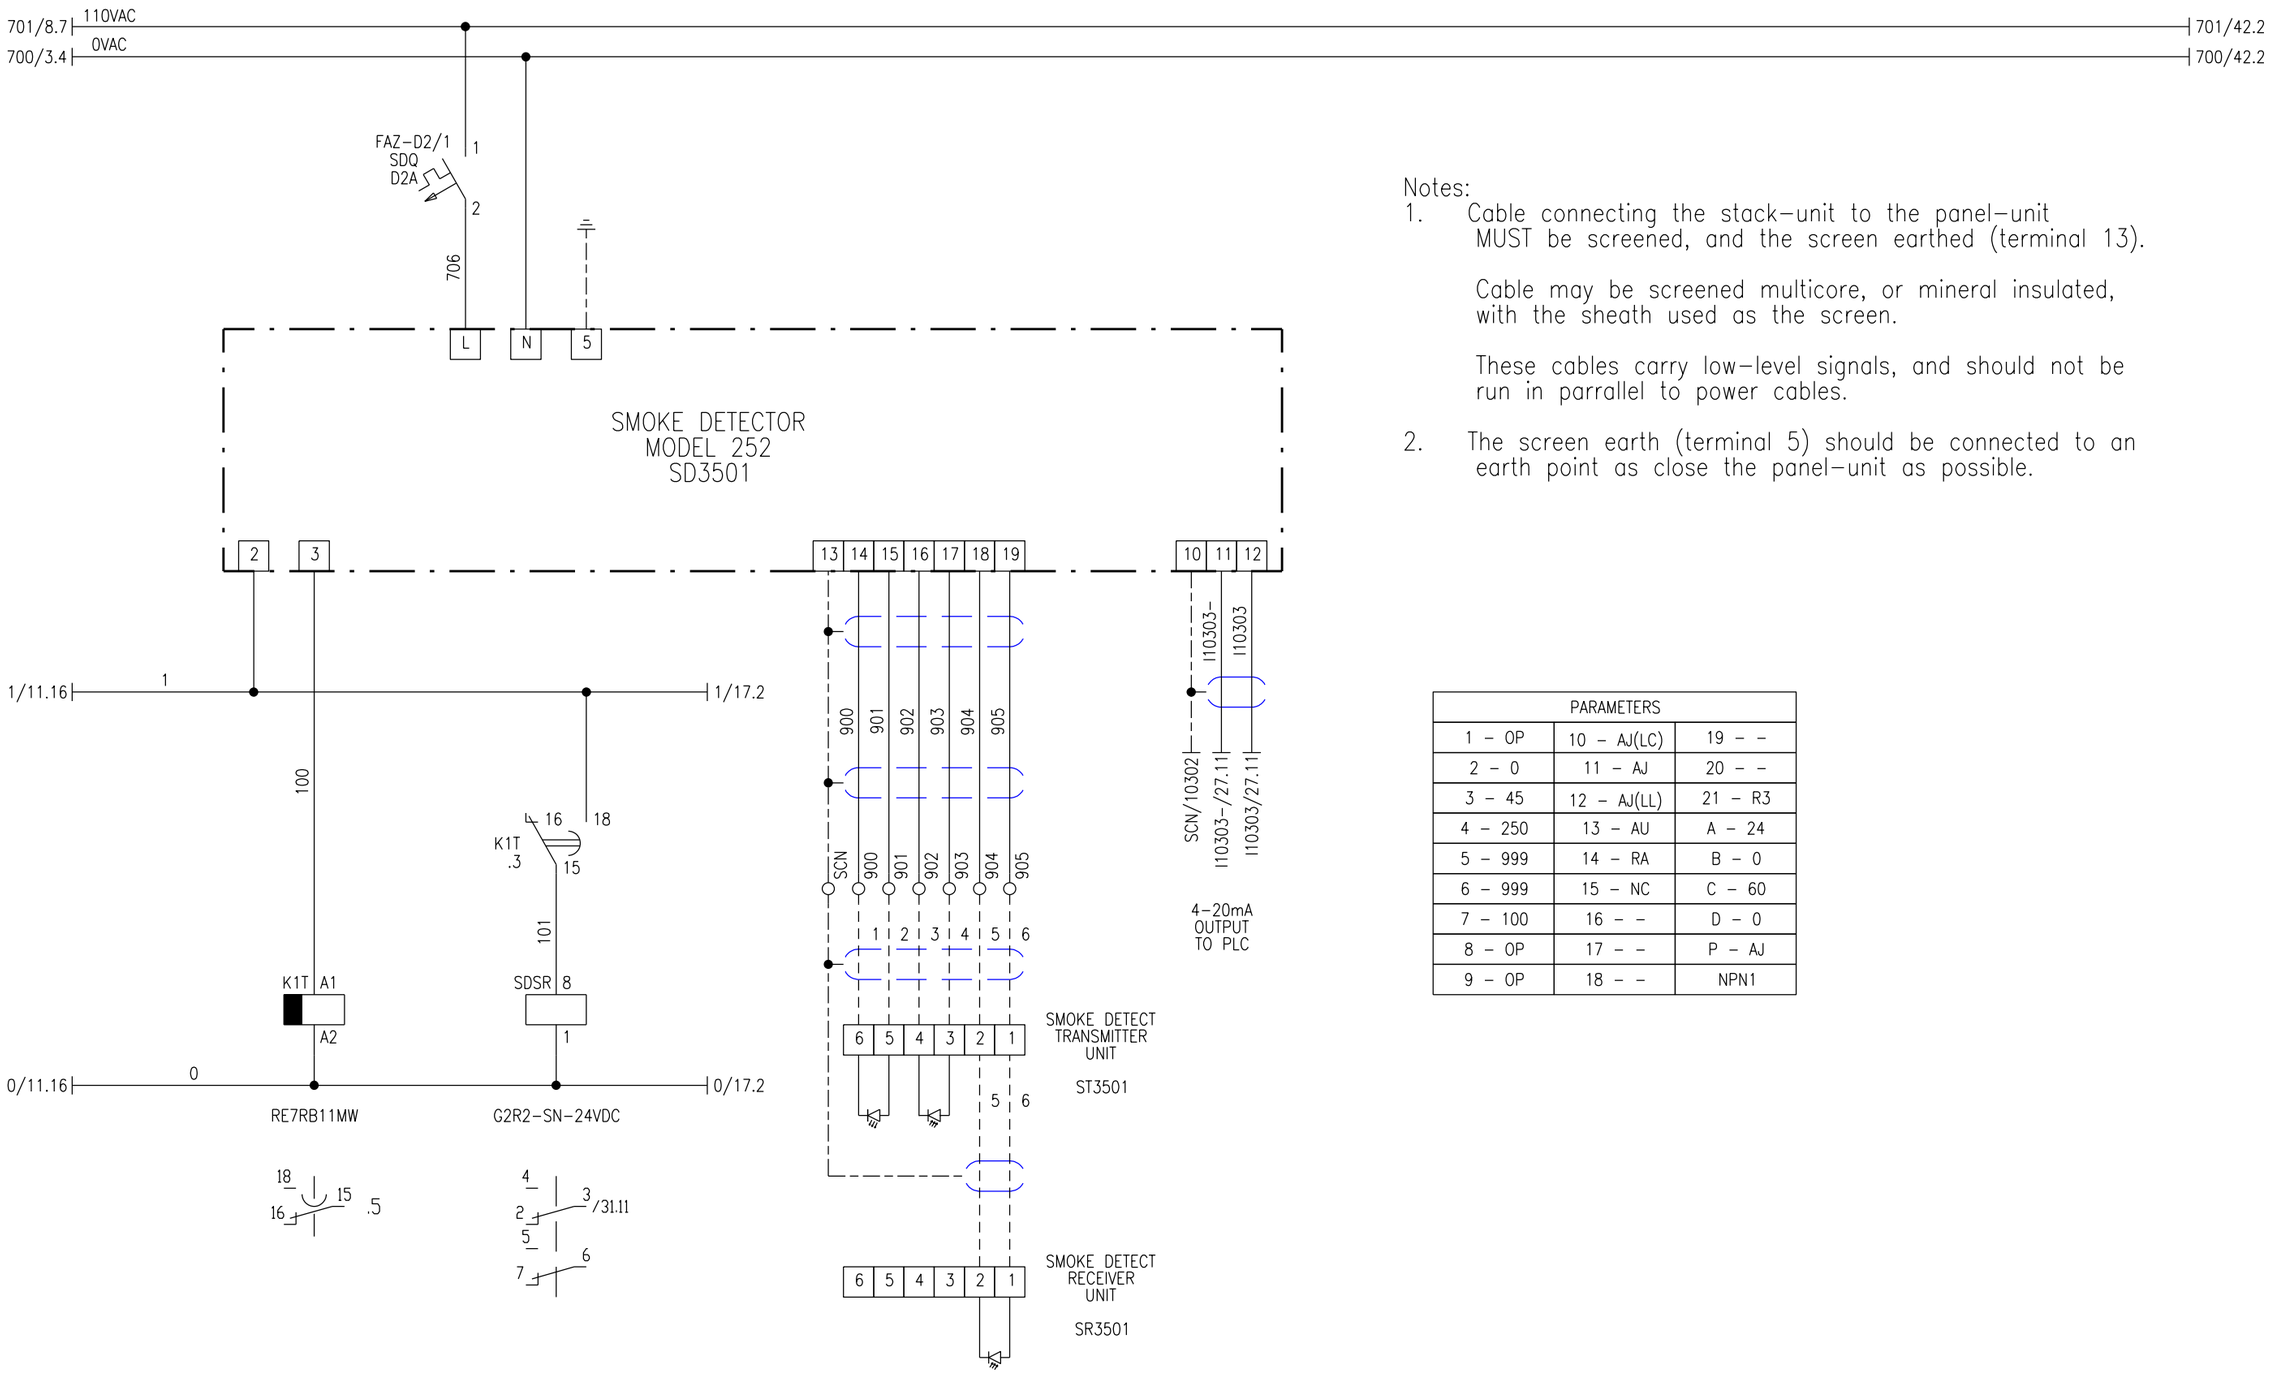

Notes:

1. Cable connecting the stack-unit to the panel-unit MUST be screened, and the screen earthed (terminal 13).

   Cable may be screened multicore, or mineral insulated, with the sheath used as the screen.

   These cables carry low-level signals, and should not be run in parrallel to power cables.

2. The screen earth (terminal 5) should be connected to an earth point as close the panel-unit as possible.

PARAMETERS		
1 - OP	10 - AJ(LC)	19 - -
2 - 0	11 - AJ	20 - -
3 - 45	12 - AJ(LL)	21 - R3
4 - 250	13 - AU	A - 24
5 - 999	14 - RA	B - 0
6 - 999	15 - NC	C - 60
7 - 100	16 - -	D - 0
8 - OP	17 - -	P - AJ
9 - OP	18 - -	NPN1

REV	DATE	MODIFICATION	DWN	CHK
1	19/05/14	FOR APPROVAL	MS	DG

ELTEK SYSTEMS Ltd
ELTEK SYSTEMS LTD
ELTEK HOUSE,
NENE VALLEY BUSINESS PARK
OUNDLE, PETERBOROUGH.PE8 4HN
TEL 01832 277590 FAX 01832 273941
Email: info@eltek-systems.com

TITLE

G4 HEATER PANEL
PC32 LINE 4
WSF, LEICESTER

CLIENT

Flo-Mech
FLO-MECH LTD FLO-MECH HOUSE,
PAXTON ROAD, ORTON GOLDHAY
PETERBOROUGH.PE2 5YA, ENGLAND.
TEL +44(0)1733233166
FAX +44(0)1733235200
Email: enquiries@flo-mech.com
Internet: www.flo-mech.com

DATE 19/05/14
DWG NO 5620
SHEET 12 OF 55

1	2	3	4	5	6	7	8	9	10	11	12	13	14	15	16

THIS SHEET IS LEFT BLANK INTENTIONALLY

REV	DATE	MODIFICATION	DWN	CHK
1	19/05/14	FOR APPROVAL	MS	DG

ELTEK SYSTEMS Ltd

ELTEK SYSTEMS LTD
ELTEK HOUSE,
NENE VALLEY BUSINESS PARK
OUNDLE, PETERBOROUGH.PE8 4HN
TEL 01832 277590 FAX 01832 273941
Email: info@eltek-systems.com

TITLE

G4 HEATER PANEL
PC32 LINE 4
WSF, LEICESTER

CLIENT

Flo~Mech

FLO-MECH LTD FLO-MECH HOUSE,
PAXTON ROAD, ORTON GOLDHAY
PETERBOROUGH.PE2 5YA, ENGLAND.
TEL +44(0)1733233166
FAX +44(0)1733235200
Email: enquiries@flo-mech.com
Internet: www.flo-mech.com

DATE 19/05/14
DWG NO 5620
SHEET 13 OF 55

PLC LAYOUT

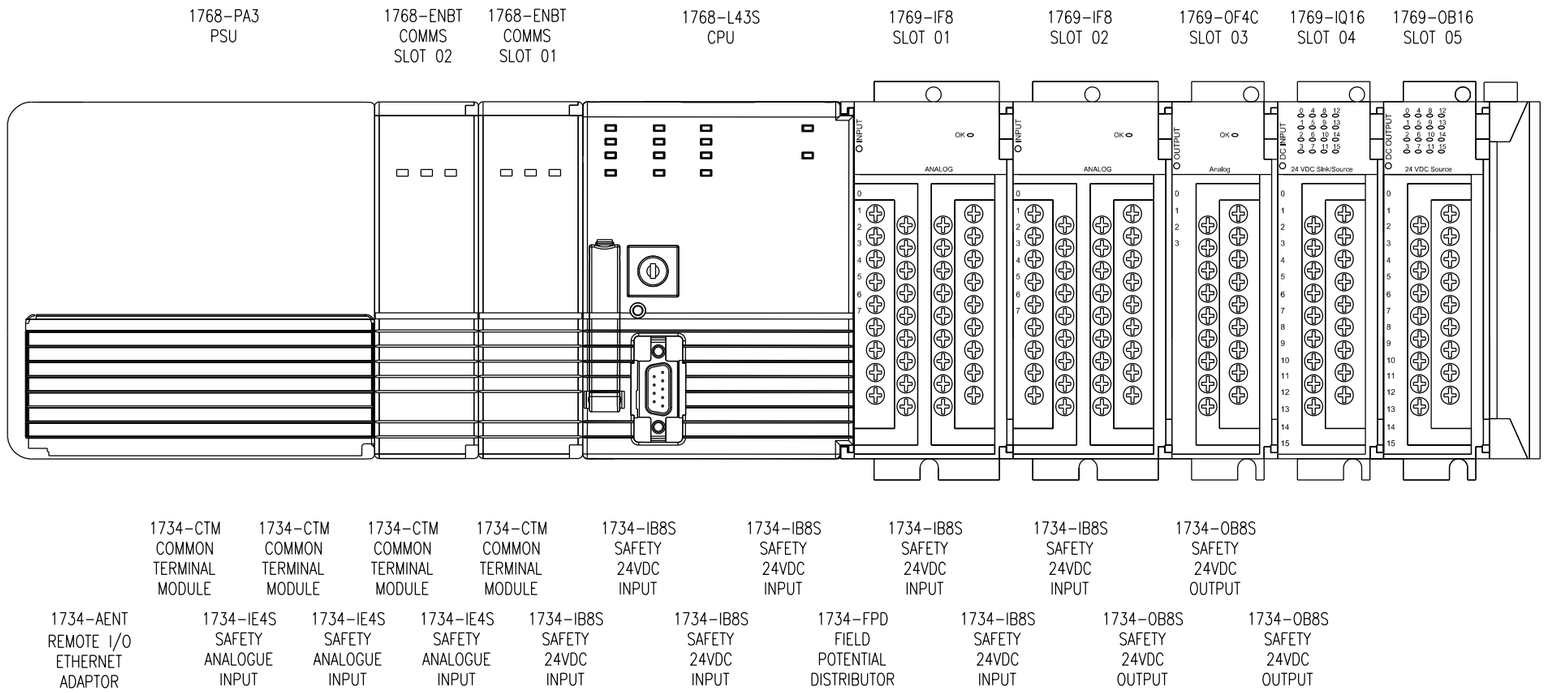

REV	DATE	MODIFICATION	DWN	CHK
1	19/05/14	FOR APPROVAL	MS	DG

ELTEK SYSTEMS Ltd

ELTEK SYSTEMS LTD
ELTEK HOUSE,
NENE VALLEY BUSINESS PARK
OUNDLE, PETEROBOROUGH.PE8 4HN
TEL 01832 277590 FAX 01832 273941
Email: info@eltek-systems.com

TITLE

G4 HEATER PANEL
PC32 LINE 4
WSF, LEICESTER

CLIENT

Flo~Mech

FLO-MECH LTD FLO-MECH HOUSE,
PAXTON ROAD, ORTON GOLDHAY
PETERBOROUGH.PE2 5YA, ENGLAND.
TEL +44(0)1733233166
FAX +44(0)1733235200
Email: enquiries@flo-mech.com
Internet: www.flo-mech.com

DATE 19/05/14
DWG NO 5620
SHEET 14 OF 55

PLC COMMS SLOT 02

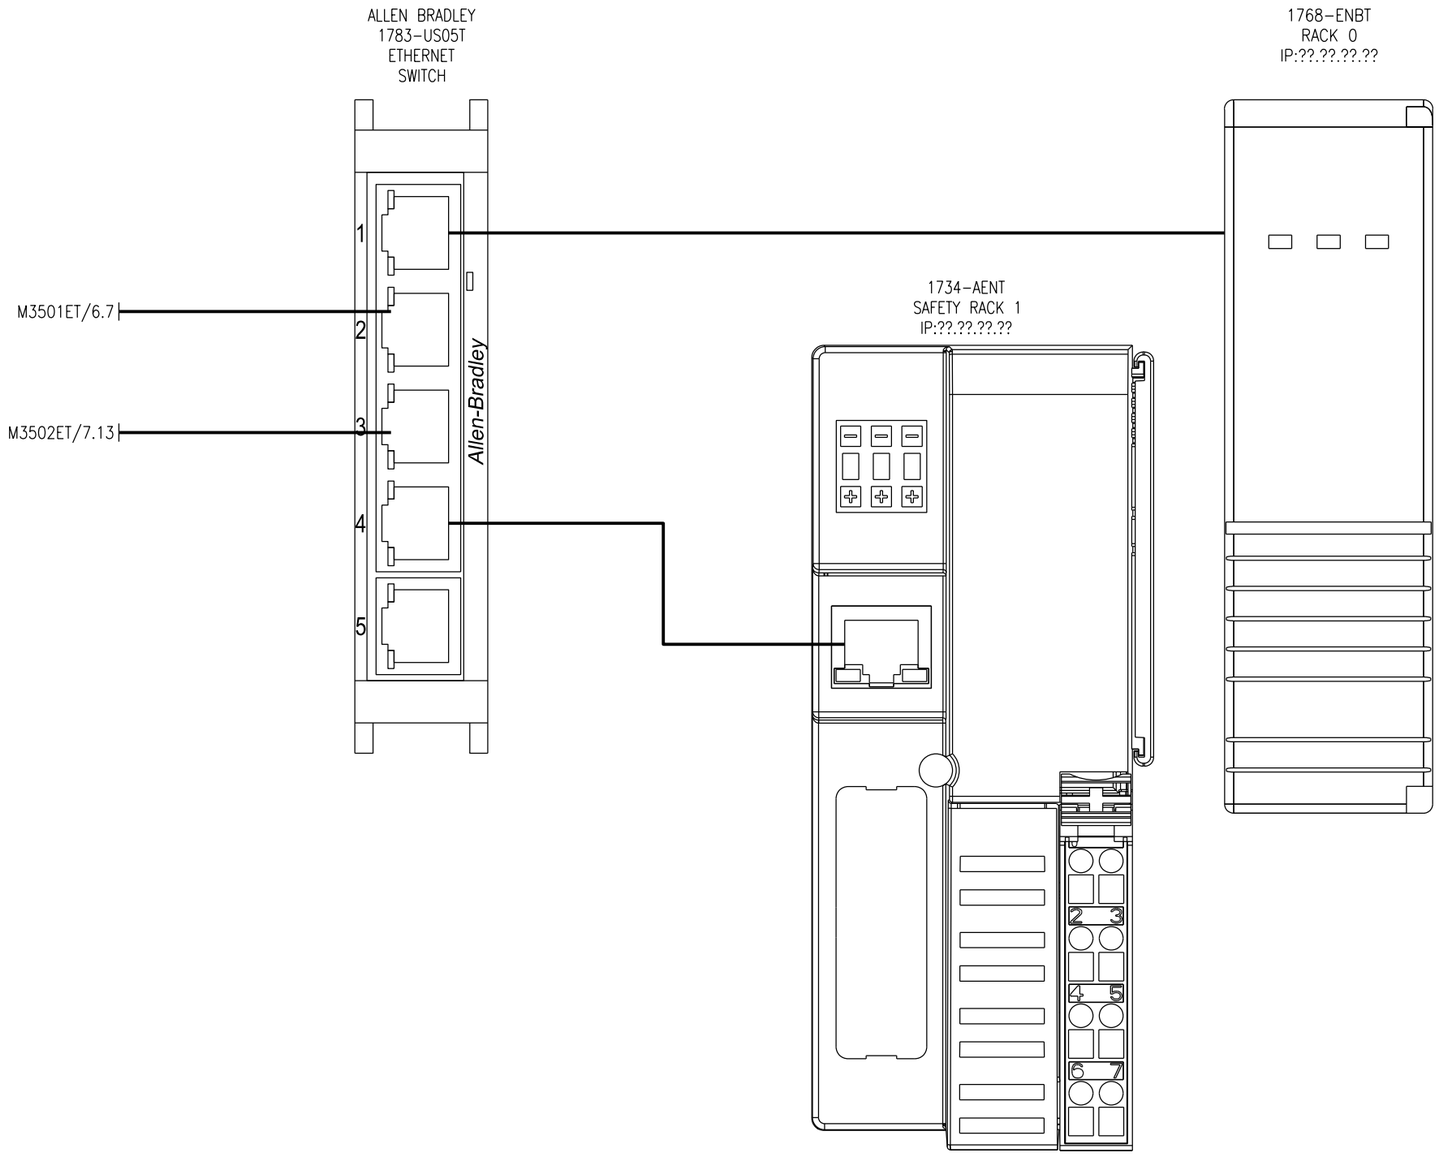

REV	DATE	MODIFICATION	DWN	CHK
1	19/05/14	FOR APPROVAL	MS	DG

ELTEK SYSTEMS LTD
ELTEK HOUSE,
NENE VALLEY BUSINESS PARK
OUNDLE, PETERBOROUGH.PE8 4HN
TEL 01832 277590 FAX 01832 273941
Email: info@eltek-systems.com
ELTEK SYSTEMS Ltd

TITLE

G4 HEATER PANEL
PC32 LINE 4
WSF, LEICESTER

CLIENT

FLO-MECH LTD FLO-MECH HOUSE,
PAXTON ROAD, ORTON GOLDHAY
PETERBOROUGH.PE2 5YA, ENGLAND.
TEL +44(0)1733233166
FAX +44(0)1733235200
Email: enquiries@flo-mech.com
Internet: www.flo-mech.com

DATE 19/05/14
DWG NO 5620
SHEET 15 OF 55

PLC COMMS SLOT 01

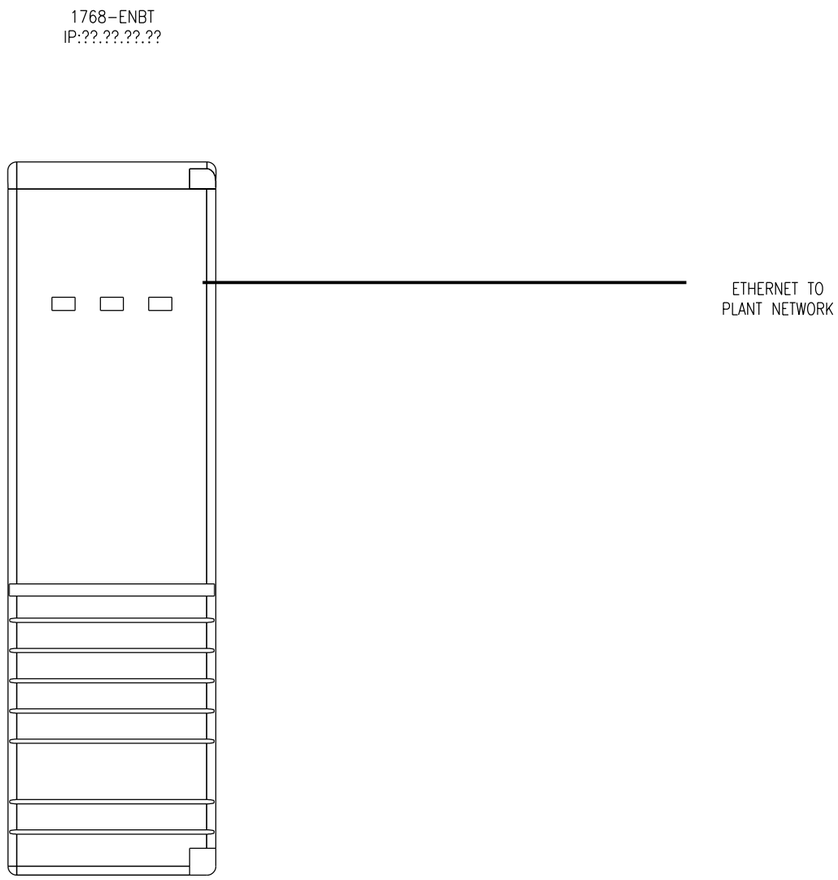

REV	DATE	MODIFICATION	DWN	CHK
1	19/05/14	FOR APPROVAL	MS	DG

ELTEK SYSTEMS LTD
ELTEK HOUSE,
NENE VALLEY BUSINESS PARK
OUNDLE, PETERBOROUGH.PE8 4HN
TEL 01832 277590 FAX 01832 273941
Email: info@eltek-systems.com

TITLE

G4 HEATER PANEL
PC32 LINE 4
WSF, LEICESTER

CLIENT

FLO-MECH LTD FLO-MECH HOUSE,
PAXTON ROAD, ORTON GOLDHAY
PETERBOROUGH.PE2 5YA, ENGLAND.
TEL +44(0)1733233166
FAX +44(0)1733235200
Email: enquiries@flo-mech.com
Internet: www.flo-mech.com

DATE 19/05/14
DWG NO 5620
SHEET 16 OF 55

PLC SLOT 01

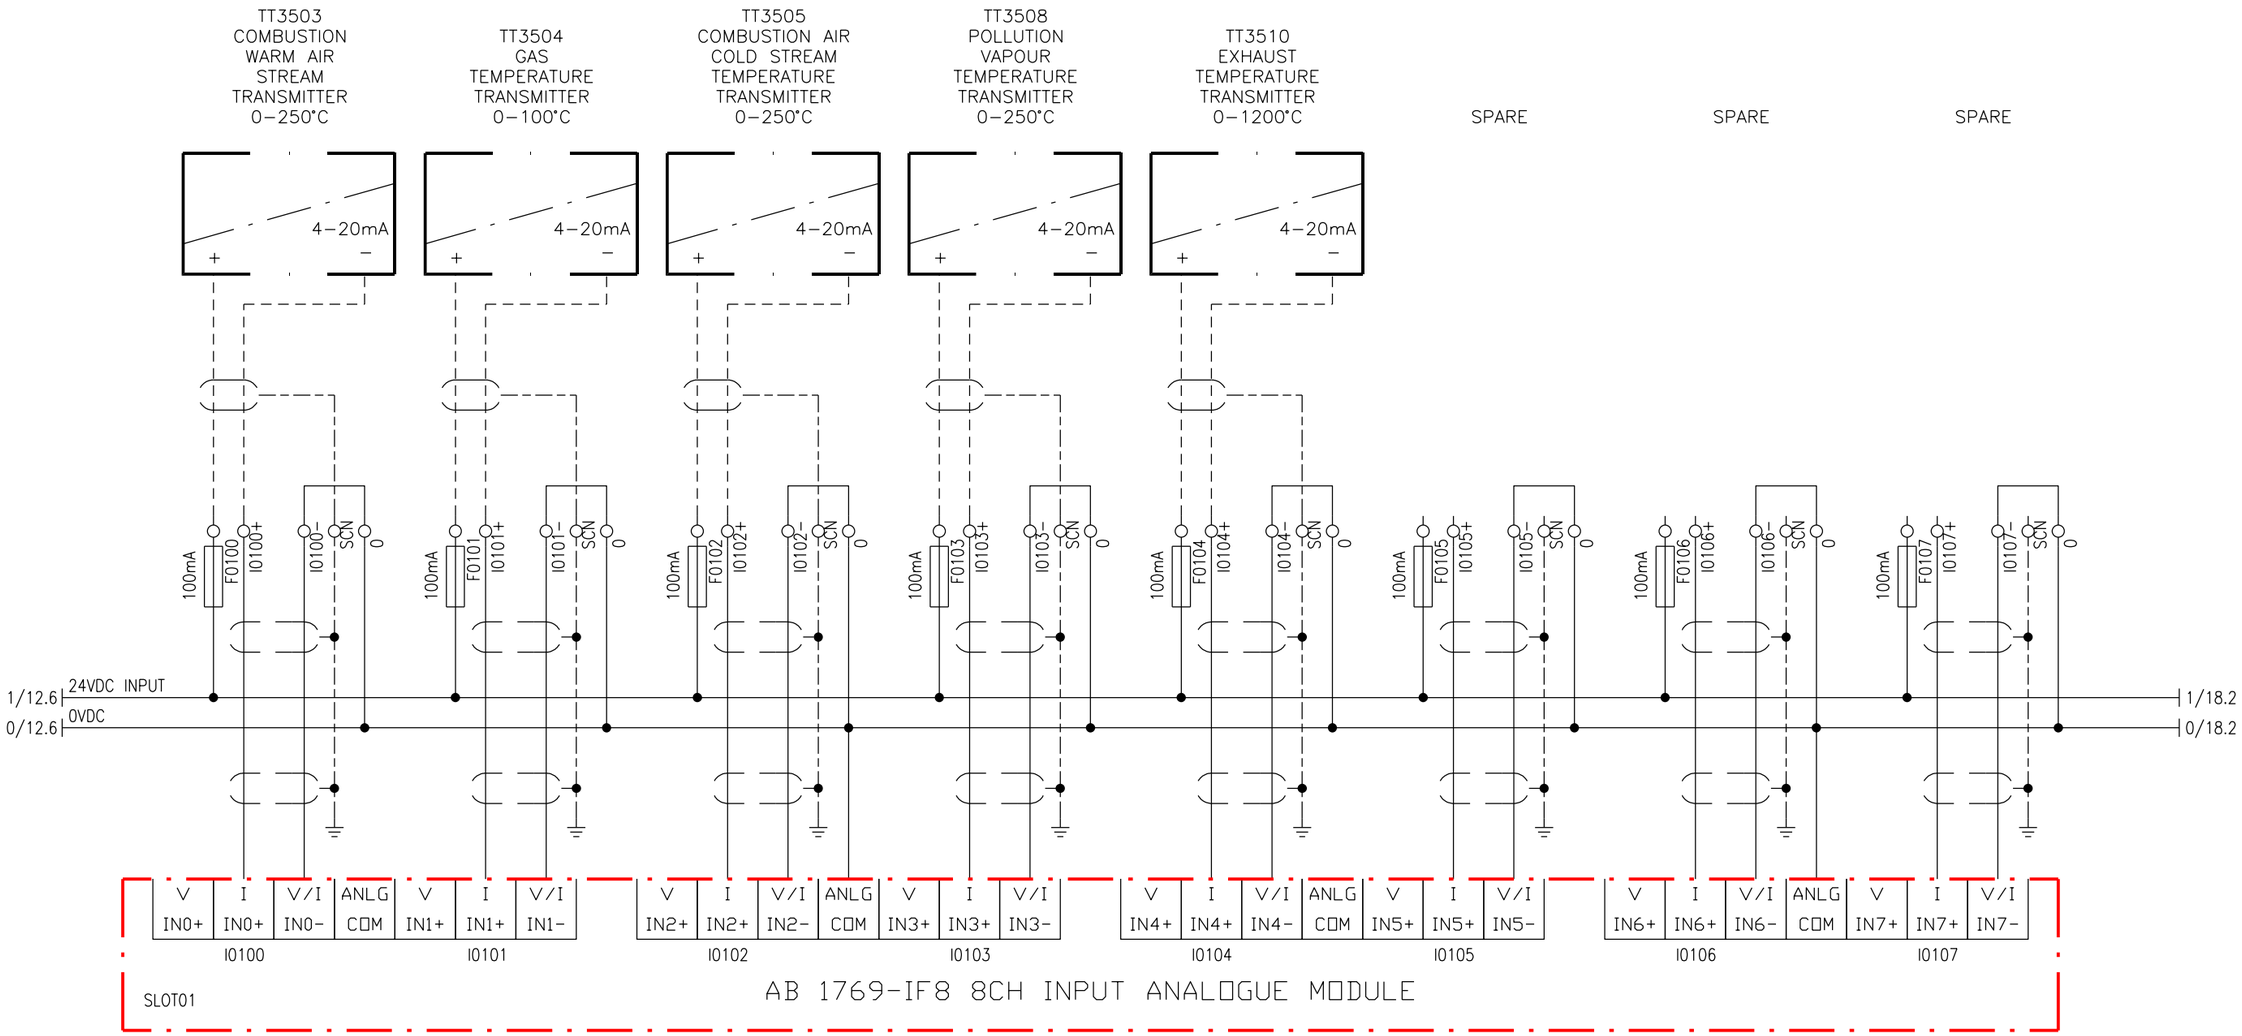

REV	DATE	MODIFICATION	DWN	CHK
1	19/05/14	FOR APPROVAL	MS	DG

ELTEK SYSTEMS LTD
ELTEK HOUSE,
NENE VALLEY BUSINESS PARK
OUNDLE, PETERBOROUGH.PE8 4HN
TEL 01832 277590 FAX 01832 273941
Email: info@eltek-systems.com
ELTEK SYSTEMS Ltd

TITLE

G4 HEATER PANEL
PC32 LINE 4
WSF, LEICESTER

CLIENT

Flo~Mech
FLO-MECH LTD FLO-MECH HOUSE,
PAXTON ROAD, ORTON GOLDHAY
PETERBOROUGH.PE2 5YA, ENGLAND.
TEL +44(0)1733233166
FAX +44(0)1733235200
Email: enquiries@flo-mech.com
Internet: www.flo-mech.com

DATE 19/05/14
DWG NO 5620
SHEET 17 OF 55

PLC SLOT 02

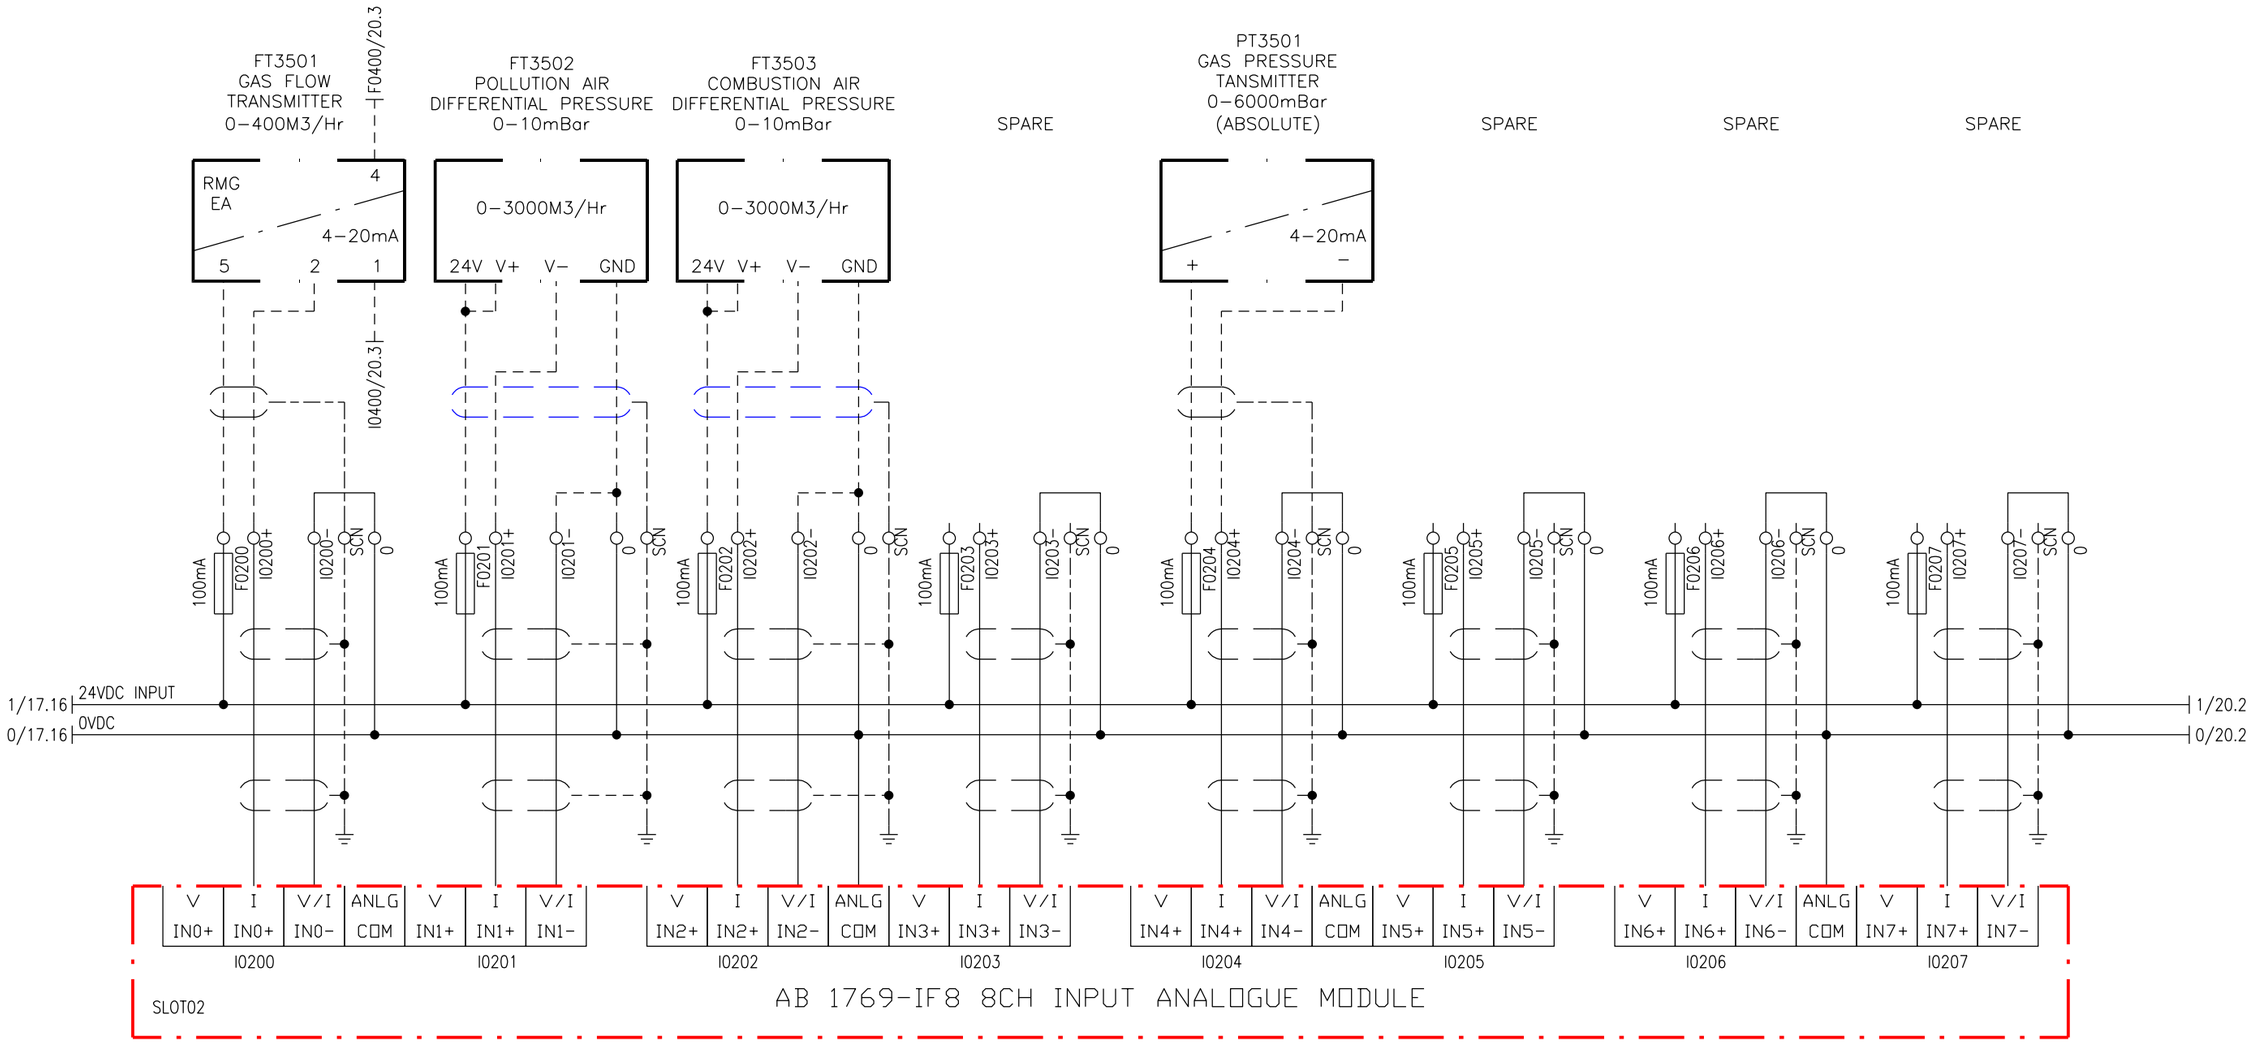

REV	DATE	MODIFICATION	DWN	CHK
1	19/05/14	FOR APPROVAL	MS	DG

ELTEK SYSTEMS LTD
ELTEK HOUSE,
NENE VALLEY BUSINESS PARK
OUNDLE, PETERBOROUGH.PE8 4HN
TEL 01832 277590 FAX 01832 273941
Email: info@eltek-systems.com

TITLE

G4 HEATER PANEL
PC32 LINE 4
WSF, LEICESTER

CLIENT

FLO-MECH LTD FLO-MECH HOUSE,
PAXTON ROAD, ORTON GOLDHAY
PETERBOROUGH.PE2 5YA, ENGLAND.
TEL +44(0)1733233166
FAX +44(0)1733235200
Email: enquiries@flo-mech.com
Internet: www.flo-mech.com

DATE 19/05/14
DWG NO 5620
SHEET 18 OF 55

PLC SLOT 03

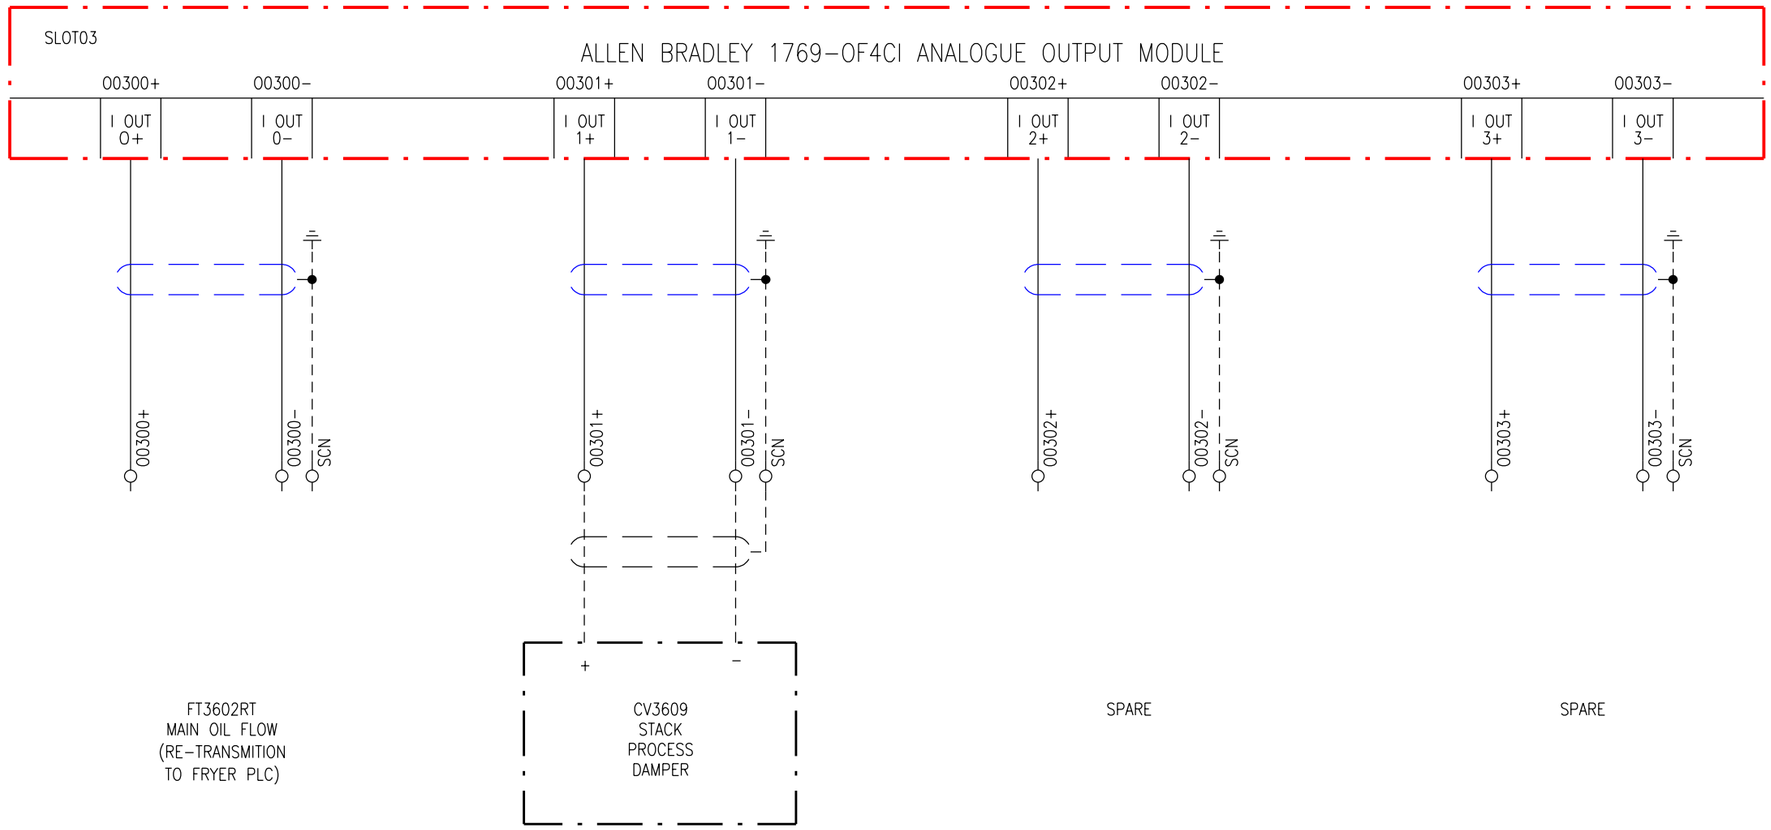

REV	DATE	MODIFICATION	DWN	CHK
1	19/05/14	FOR APPROVAL	MS	DG

ELTEK SYSTEMS Ltd
ELTEK SYSTEMS LTD
ELTEK HOUSE,
NENE VALLEY BUSINESS PARK
OUNDLE, PETERBOROUGH,PE8 4HN
TEL 01832 277590 FAX 01832 273941
Email: info@eltek-systems.com

TITLE

G4 HEATER PANEL
PC32 LINE 4
WSF, LEICESTER

CLIENT

Flo-Mech

FLO-MECH LTD FLO-MECH HOUSE,
PAXTON ROAD, ORTON GOLDHAY
PETERBOROUGH.PE2 5YA, ENGLAND.
TEL +44(0)1733233166
FAX +44(0)1733235200
Email: enquiries@flo-mech.com
Internet: www.flo-mech.com

DATE 19/05/14
DWG NO 5620
SHEET 19 OF 55

PLC SLOT 04

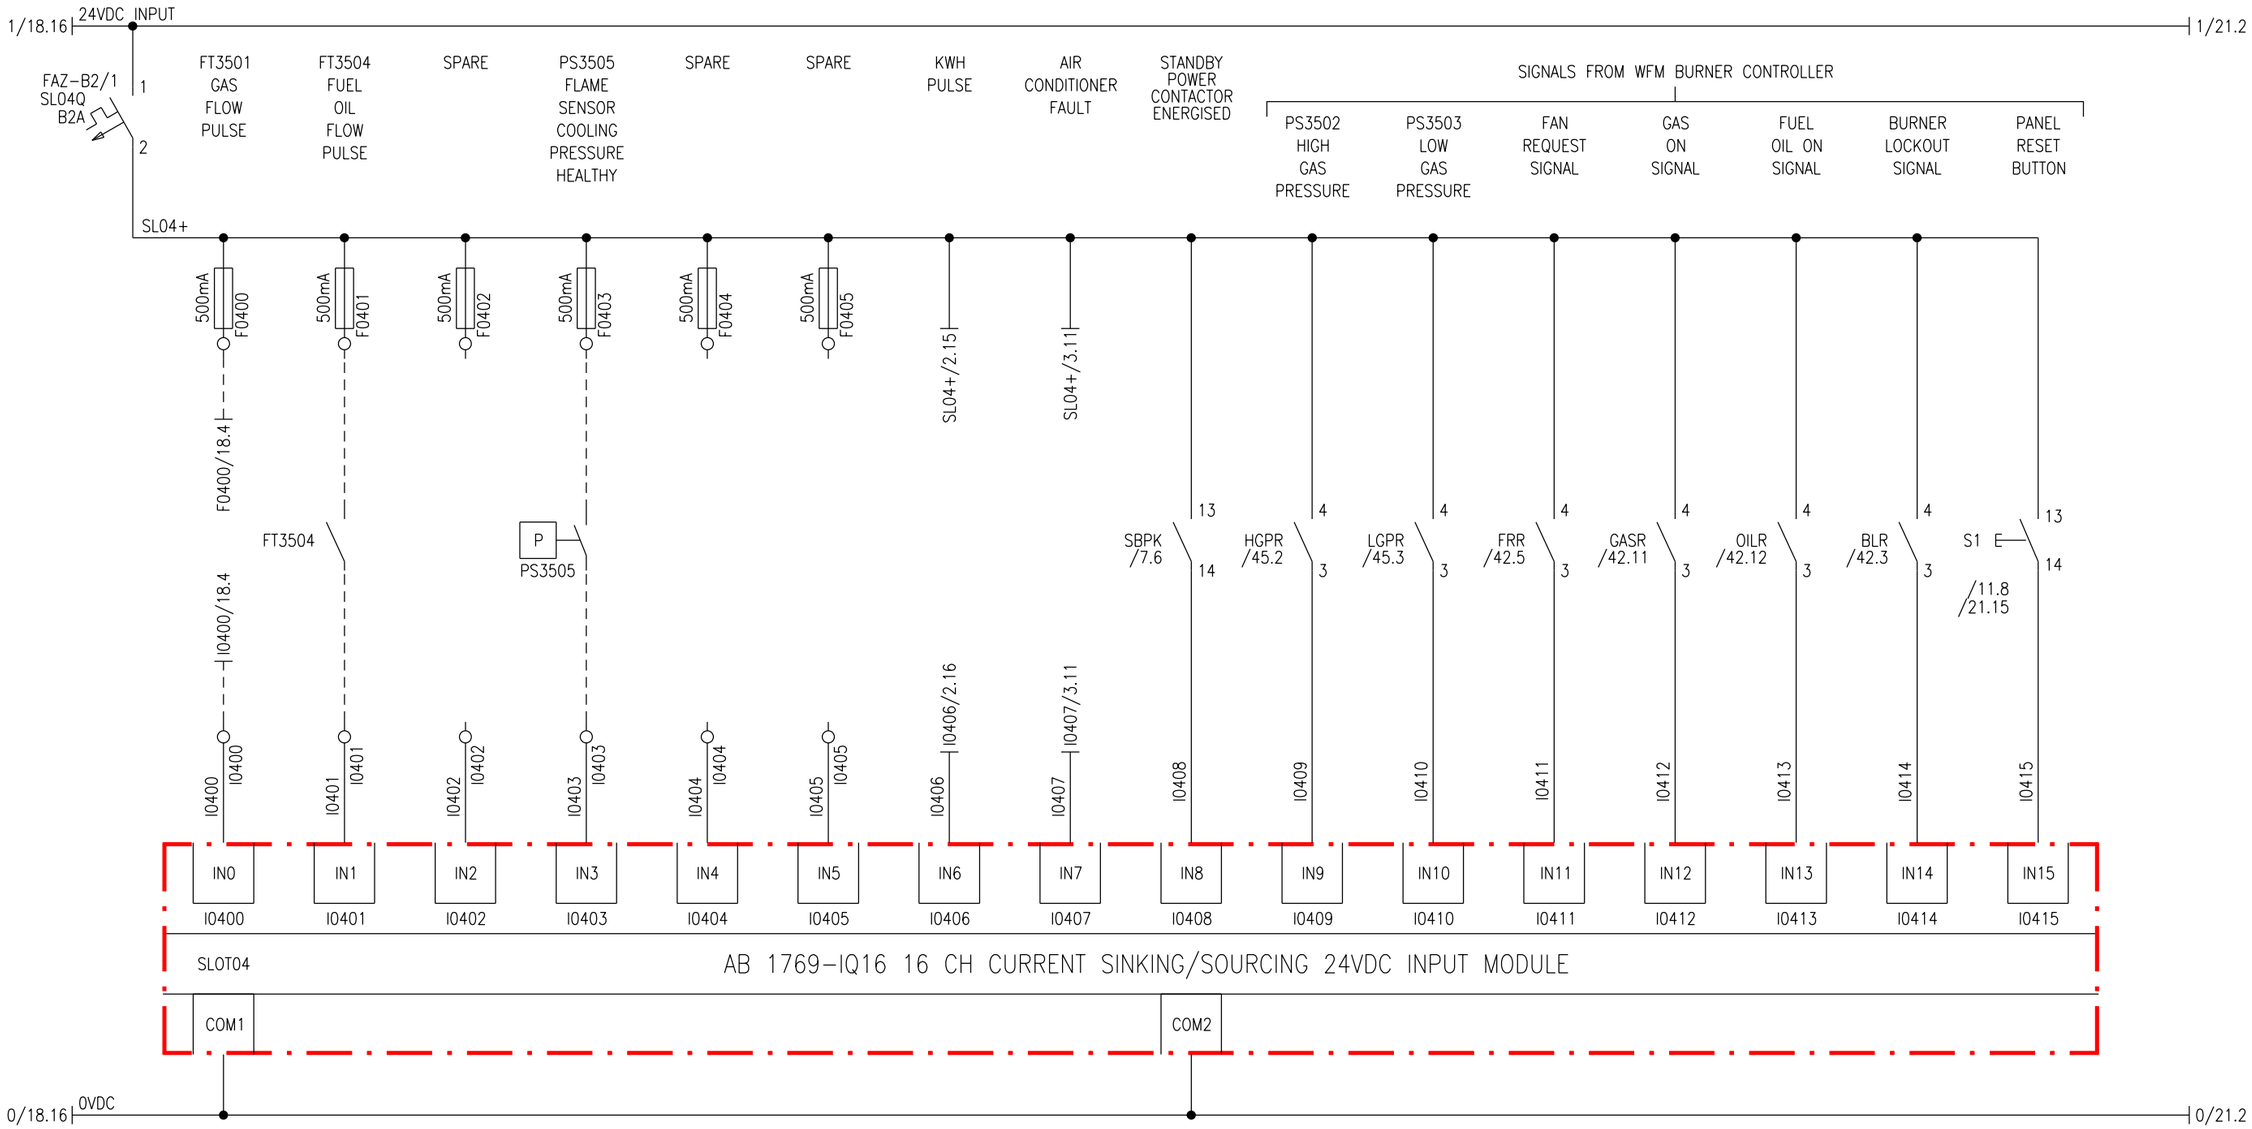

REV	DATE	MODIFICATION	DWN	CHK
1	19/05/14	FOR APPROVAL	MS	DG

ELTEK SYSTEMS LTD
ELTEK HOUSE,
NENE VALLEY BUSINESS PARK
OUNDLE, PETERBOROUGH.PE8 4HN
TEL 01832 277590 FAX 01832 273941
Email: info@eltek-systems.com

TITLE

G4 HEATER PANEL
PC32 LINE 4
WSF, LEICESTER

CLIENT

FLO-MECH LTD FLO-MECH HOUSE,
PAXTON ROAD, ORTON GOLDHAY
PETERBOROUGH.PE2 5YA, ENGLAND.
TEL +44(0)1733233166
FAX +44(0)1733235200
Email: enquiries@flo-mech.com
Internet: www.flo-mech.com

DATE 19/05/14
DWG NO 5620
SHEET 20 OF 55

PLC SLOT 05

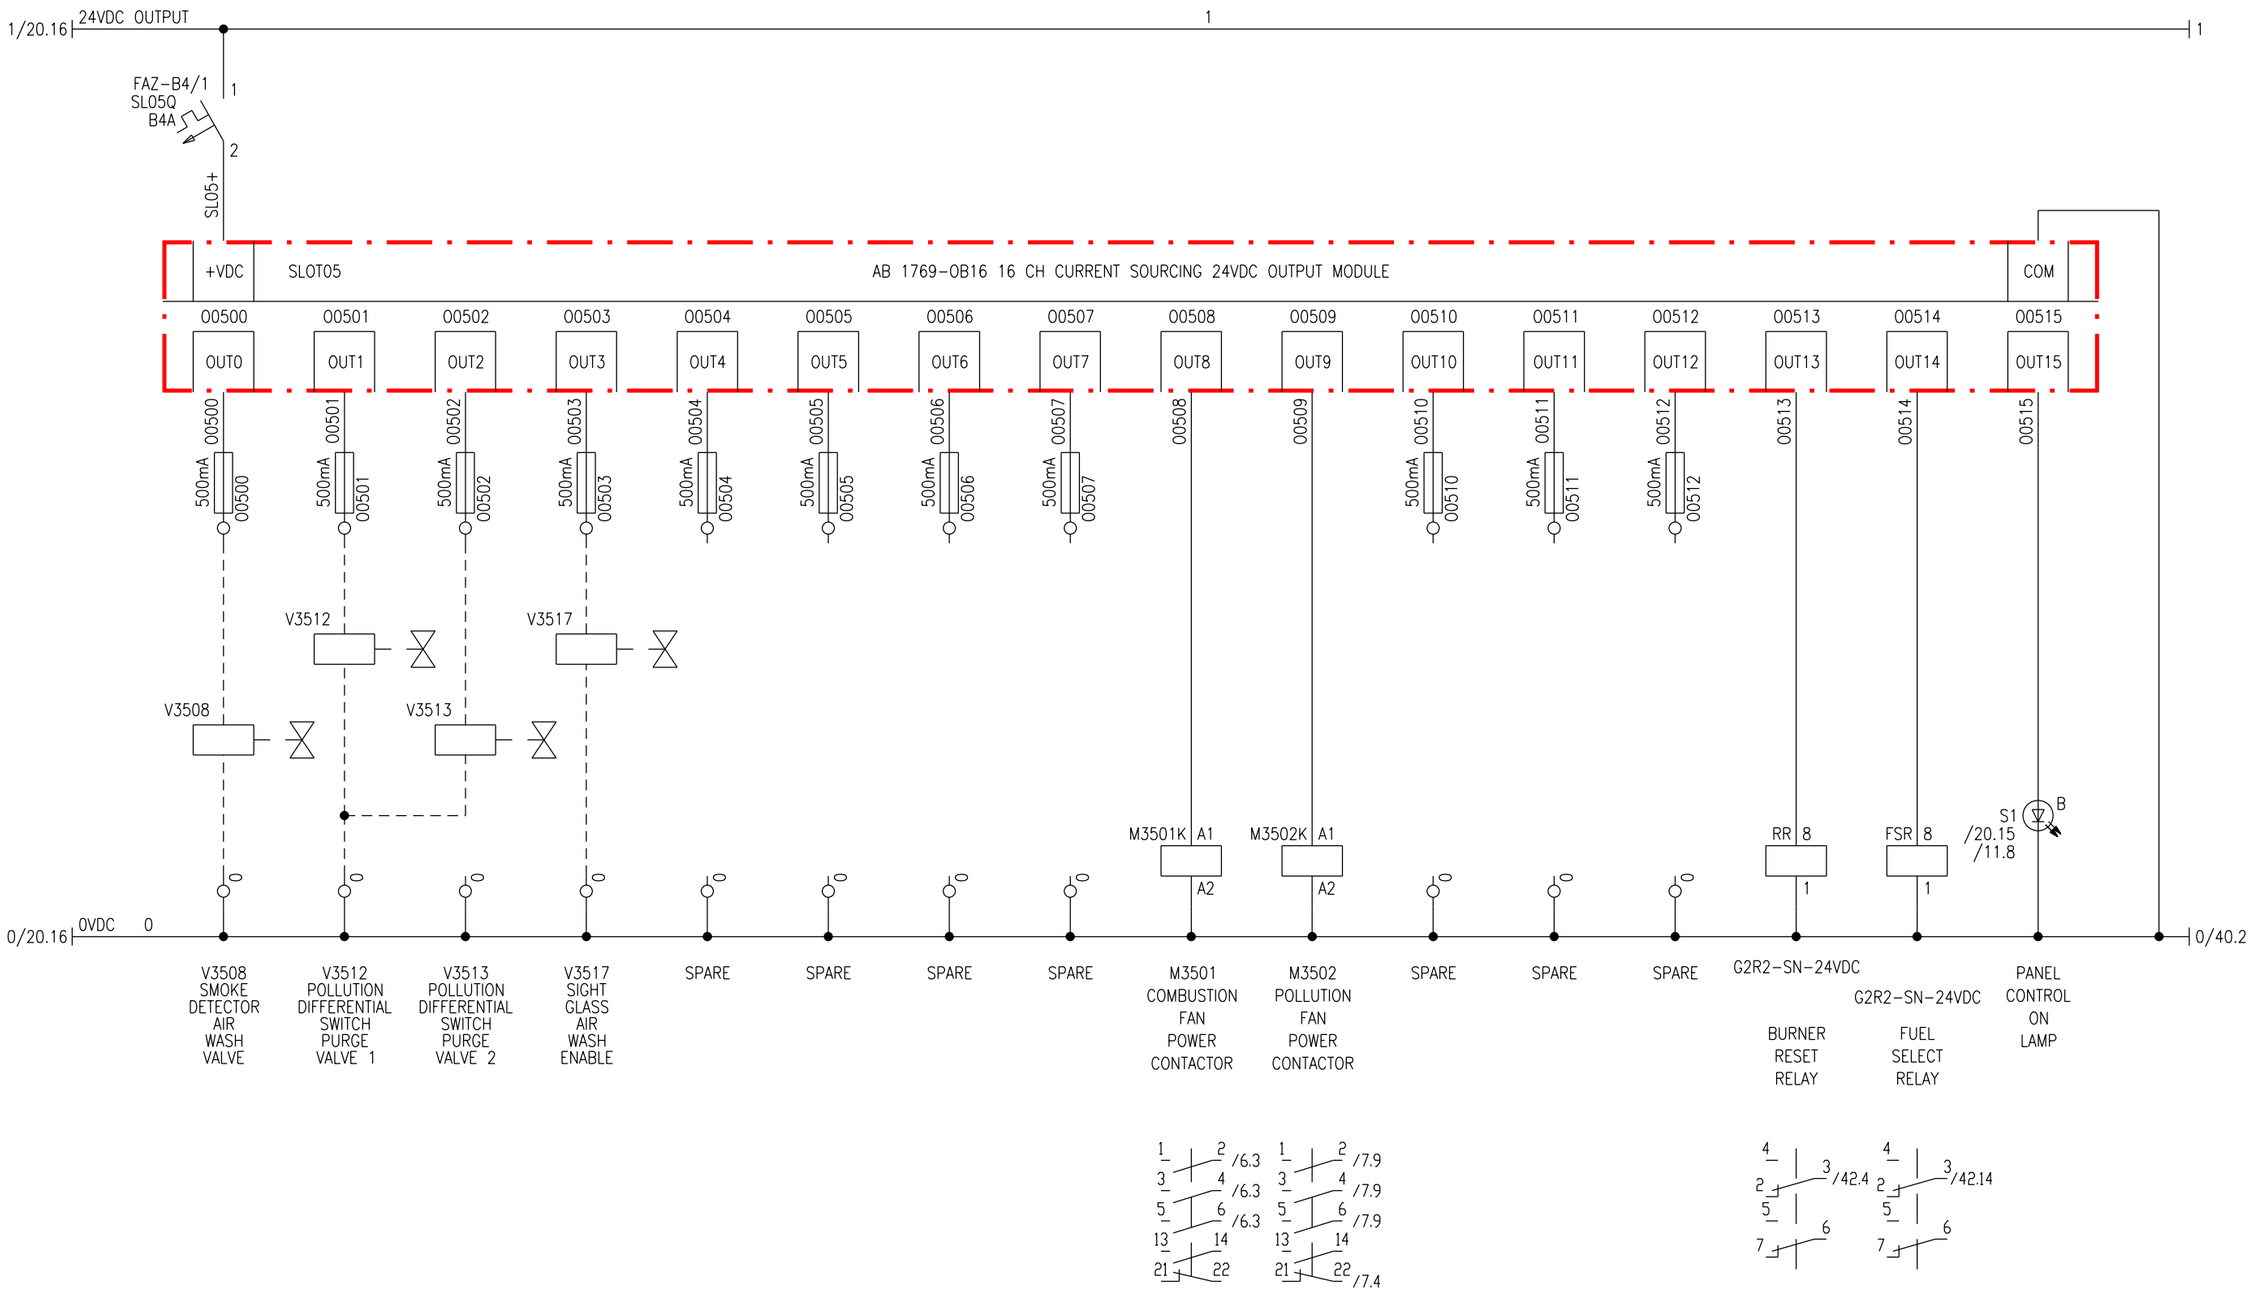

REV	DATE	MODIFICATION	DWN	CHK
1	19/05/14	FOR APPROVAL	MS	DG

ELTEK SYSTEMS Ltd

ELTEK SYSTEMS LTD
ELTEK HOUSE,
NENE VALLEY BUSINESS PARK
OUNDLE, PETERBOROUGH.PE8 4HN
TEL 01832 277590 FAX 01832 273941
Email: info@eltek-systems.com

TITLE

G4 HEATER PANEL
PC32 LINE 4
WSF, LEICESTER

CLIENT

Flo~Mech

FLO-MECH LTD FLO-MECH HOUSE,
PAXTON ROAD, ORTON GOLDHAY
PETERBOROUGH.PE2 5YA, ENGLAND.
TEL +44(0)1733233166
FAX +44(0)1733235200
Email: enquiries@flo-mech.com
Internet: www.flo-mech.com

DATE 19/05/14
DWG NO 5620
SHEET 21 OF 55

1	2	3	4	5	6	7	8	9	10	11	12	13	14	15	16

THIS SHEET IS LEFT BLANK INTENTIONALLY

REV	DATE	MODIFICATION	DWN	CHK
1	19/05/14	FOR APPROVAL	MS	DG

ELTEK SYSTEMS Ltd

ELTEK SYSTEMS LTD
ELTEK HOUSE,
NENE VALLEY BUSINESS PARK
OUNDLE, PETERBOROUGH.PE8 4HN
TEL 01832 277590 FAX 01832 273941
Email: info@eltek-systems.com

TITLE

G4 HEATER PANEL
PC32 LINE 4
WSF, LEICESTER

CLIENT

Flo~Mech

FLO-MECH LTD FLO-MECH HOUSE,
PAXTON ROAD, ORTON GOLDHAY
PETERBOROUGH.PE2 5YA, ENGLAND.
TEL +44(0)1733233166
FAX +44(0)1733235200
Email: enquiries@flo-mech.com
Internet: www.flo-mech.com

DATE 19/05/14
DWG NO 5620
SHEET 22 OF 55

1	2	3	4	5	6	7	8	9	10	11	12	13	14	15	16

THIS SHEET IS LEFT BLANK INTENTIONALLY

REV	DATE	MODIFICATION	DWN	CHK
1	19/05/14	FOR APPROVAL	MS	DG

ELTEK SYSTEMS Ltd

ELTEK SYSTEMS LTD
ELTEK HOUSE,
NENE VALLEY BUSINESS PARK
OUNDLE, PETERBOROUGH.PE8 4HN
TEL 01832 277590 FAX 01832 273941
Email: info@eltek-systems.com

TITLE

G4 HEATER PANEL
PC32 LINE 4
WSF, LEICESTER

CLIENT

Flo~Mech

FLO-MECH LTD FLO-MECH HOUSE,
PAXTON ROAD, ORTON GOLDHAY
PETERBOROUGH.PE2 5YA, ENGLAND.
TEL +44(0)1733233166
FAX +44(0)1733235200
Email: enquiries@flo-mech.com
Internet: www.flo-mech.com

DATE 19/05/14
DWG NO 5620
SHEET 23 OF 55

1	2	3	4	5	6	7	8	9	10	11	12	13	14	15	16

THIS SHEET IS LEFT BLANK INTENTIONALLY

REV	DATE	MODIFICATION	DWN	CHK
1	19/05/14	FOR APPROVAL	MS	DG

ELTEK SYSTEMS Ltd

ELTEK SYSTEMS LTD
ELTEK HOUSE,
NENE VALLEY BUSINESS PARK
OUNDLE, PETERBOROUGH.PE8 4HN
TEL 01832 277590 FAX 01832 273941
Email: info@eltek-systems.com

TITLE

G4 HEATER PANEL
PC32 LINE 4
WSF, LEICESTER

CLIENT

Flo~Mech

FLO-MECH LTD FLO-MECH HOUSE,
PAXTON ROAD, ORTON GOLDHAY
PETERBOROUGH.PE2 5YA, ENGLAND.
TEL +44(0)1733233166
FAX +44(0)1733235200
Email: enquiries@flo-mech.com
Internet: www.flo-mech.com

DATE 19/05/14
DWG NO 5620
SHEET 24 OF 55

SAFETY RACK 1 SLOT 01

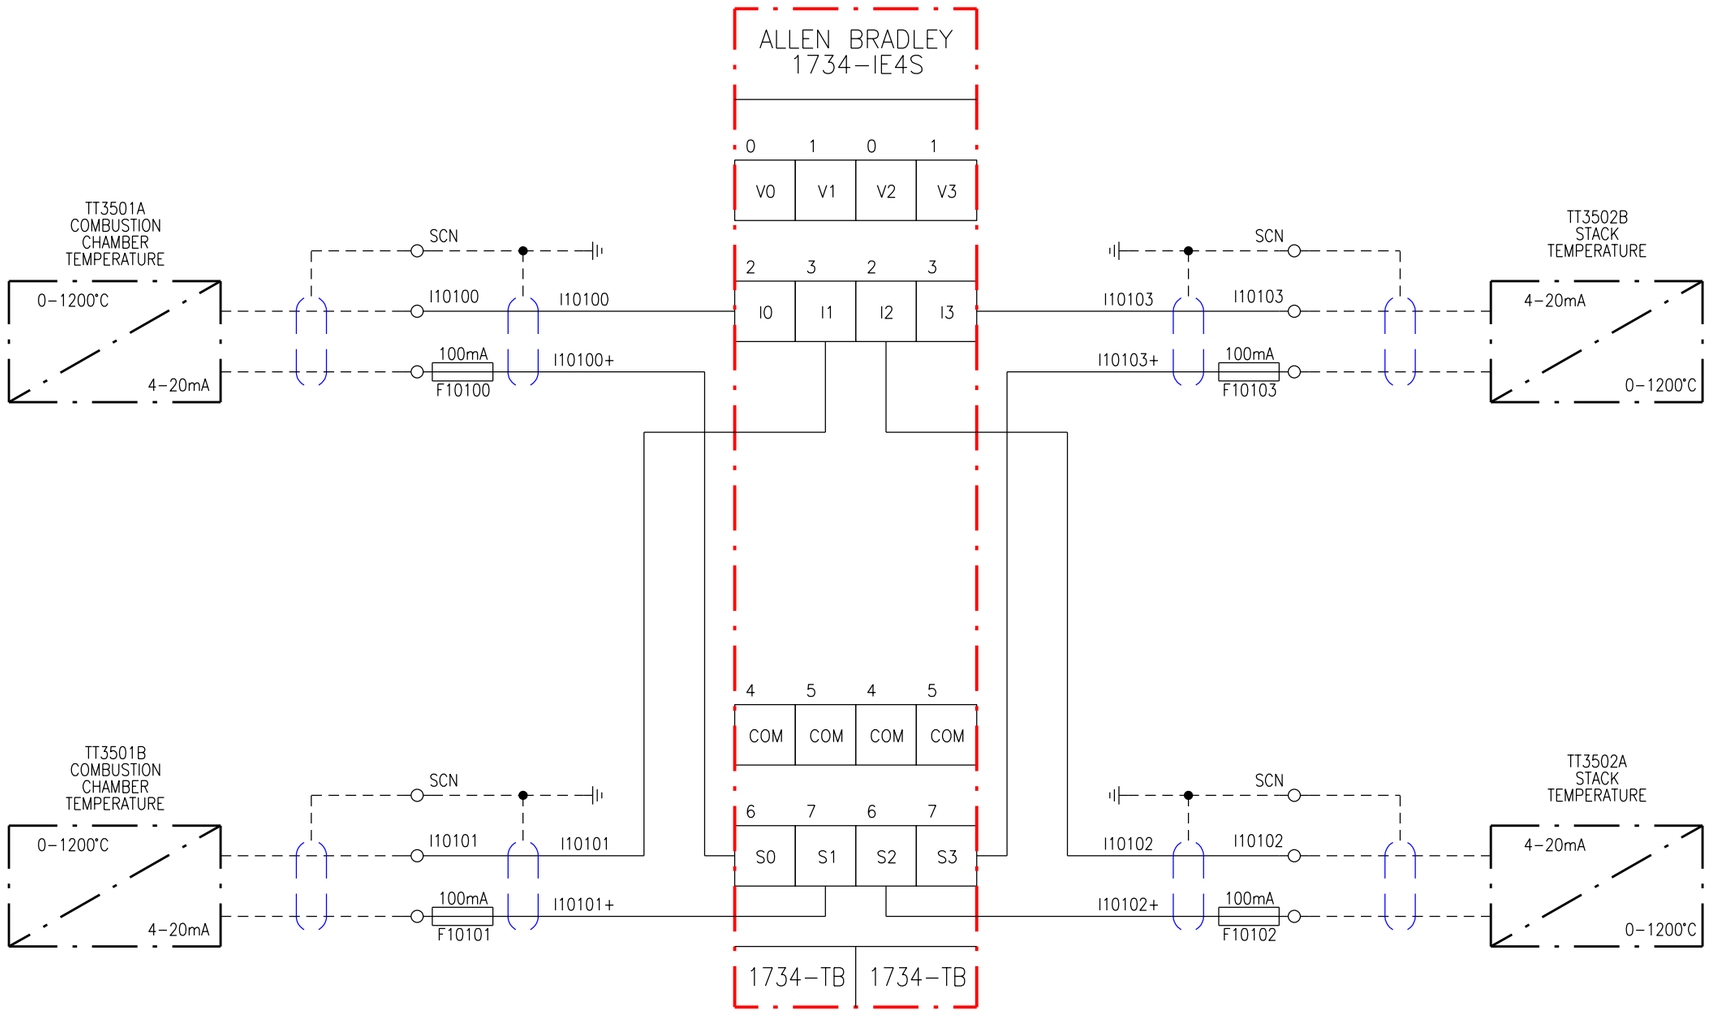

REV	DATE	MODIFICATION	DWN	CHK
1	19/05/14	FOR APPROVAL	MS	DG

ELTEK SYSTEMS Ltd

ELTEK SYSTEMS LTD
ELTEK HOUSE,
NENE VALLEY BUSINESS PARK
OUNDLE, PETERBOROUGH.PE8 4HN
TEL 01832 277590 FAX 01832 273941
Email: info@eltek-systems.com

TITLE

G4 HEATER PANEL
PC32 LINE 4
WSF, LEICESTER

CLIENT

Flo~Mech

FLO-MECH LTD FLO-MECH HOUSE,
PAXTON ROAD, ORTON GOLDHAY
PETERBOROUGH.PE2 5YA, ENGLAND.
TEL +44(0)1733233166
FAX +44(0)1733235200
Email: enquiries@flo-mech.com
Internet: www.flo-mech.com

DATE 19/05/14
DWG NO 5620
SHEET 25 OF 55

SAFETY RACK 1 SLOT 02

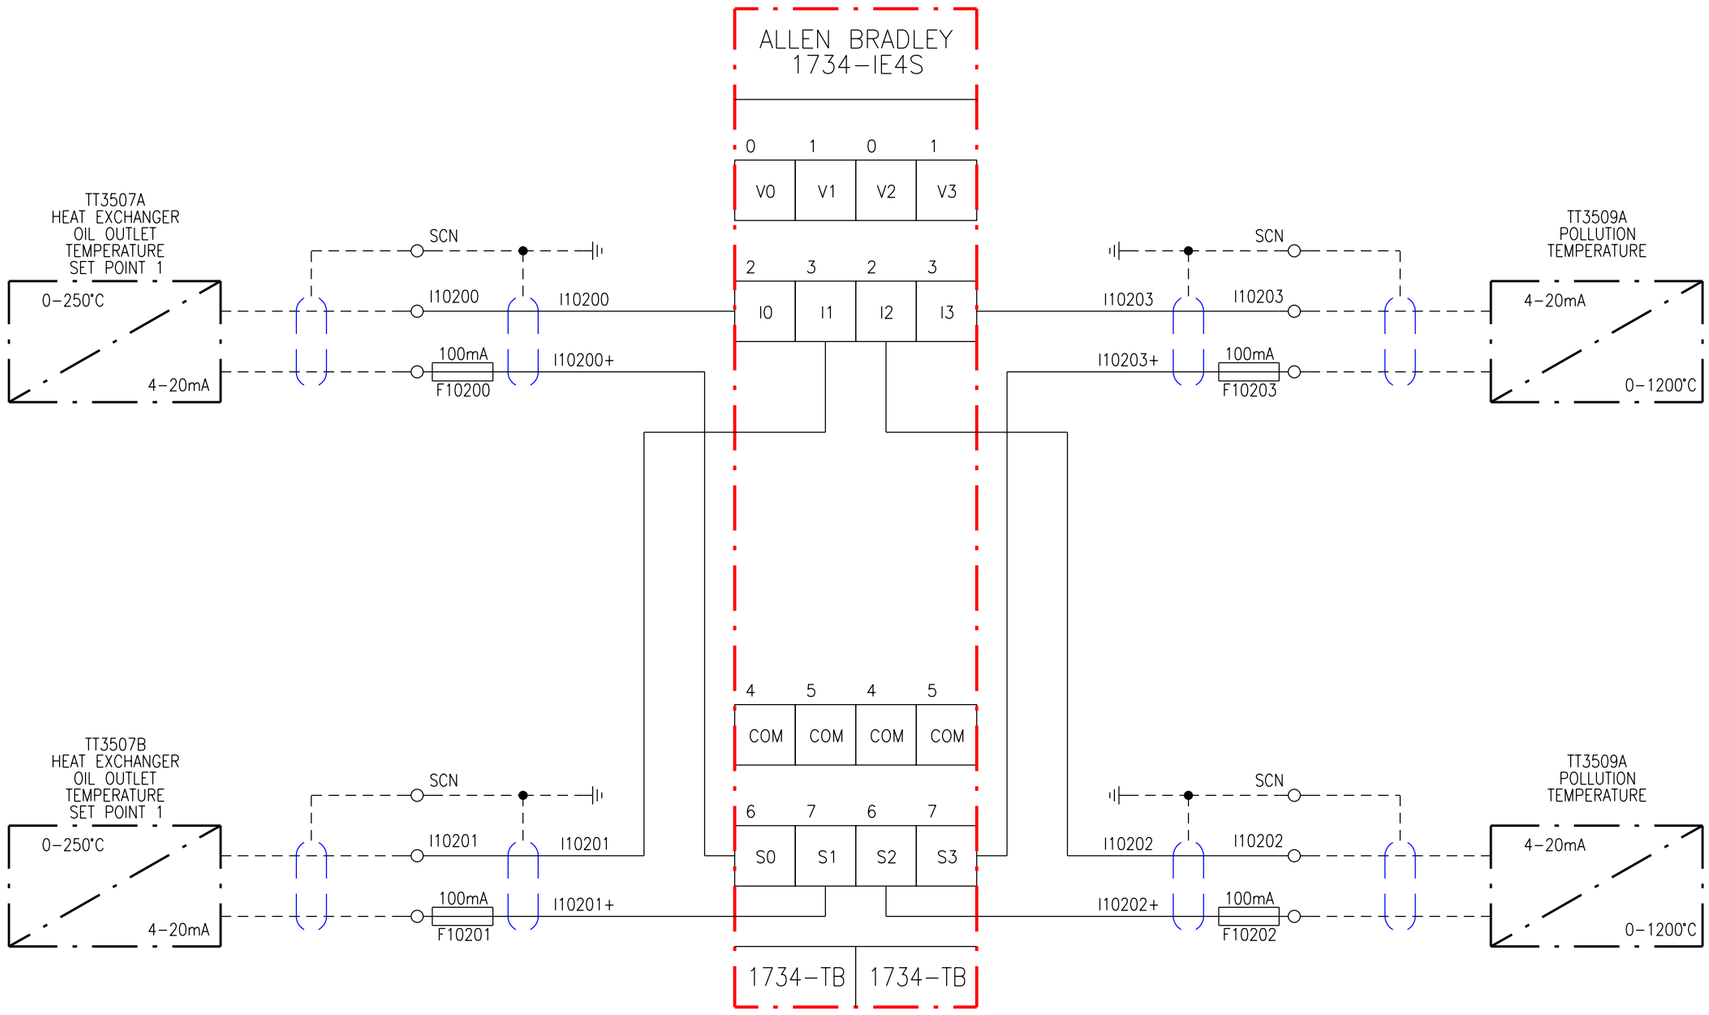

REV	DATE	MODIFICATION	DWN	CHK
1	19/05/14	FOR APPROVAL	MS	DG

ELTEK SYSTEMS Ltd

ELTEK SYSTEMS LTD
ELTEK HOUSE,
NENE VALLEY BUSINESS PARK
OUNDLE, PETERBOROUGH.PE8 4HN
TEL 01832 277590 FAX 01832 273941
Email: info@eltek-systems.com

TITLE

G4 HEATER PANEL
PC32 LINE 4
WSF, LEICESTER

CLIENT

Flo~Mech

FLO-MECH LTD FLO-MECH HOUSE,
PAXTON ROAD, ORTON GOLDHAY
PETERBOROUGH.PE2 5YA, ENGLAND.
TEL +44(0)1733233166
FAX +44(0)1733235200
Email: enquiries@flo-mech.com
Internet: www.flo-mech.com

DATE 19/05/14
DWG NO 5620
SHEET 26 OF 55

SAFETY RACK 1 SLOT 03

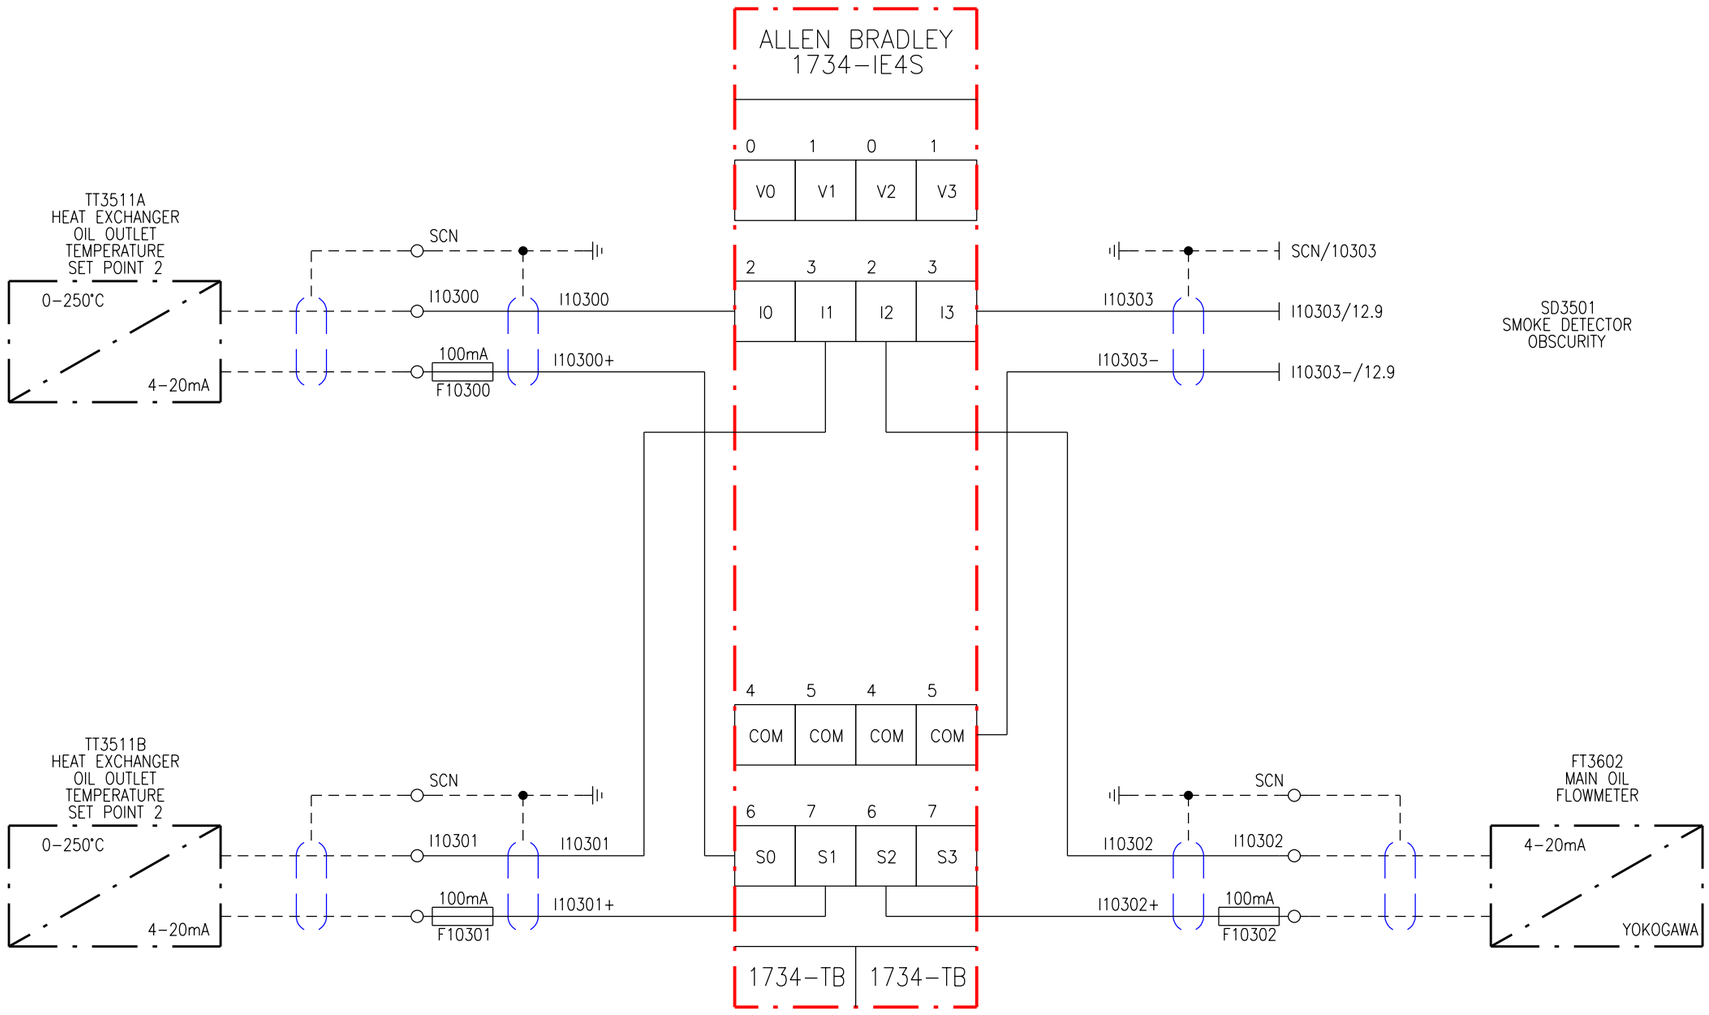

REV	DATE	MODIFICATION	DWN	CHK
1	19/05/14	FOR APPROVAL	MS	DG

ELTEK SYSTEMS Ltd

ELTEK SYSTEMS LTD
ELTEK HOUSE,
NENE VALLEY BUSINESS PARK
OUNDLE, PETERBOROUGH.PE8 4HN
TEL 01832 277590 FAX 01832 273941
Email: info@eltek-systems.com

TITLE

G4 HEATER PANEL
PC32 LINE 4
WSF, LEICESTER

CLIENT

Flo~Mech

FLO-MECH LTD FLO-MECH HOUSE,
PAXTON ROAD, ORTON GOLDHAY
PETERBOROUGH.PE2 5YA, ENGLAND.
TEL +44(0)1733233166
FAX +44(0)1733235200
Email: enquiries@flo-mech.com
Internet: www.flo-mech.com

DATE 19/05/14
DWG NO 5620
SHEET 27 OF 55

SAFETY RACK 1 SLOT 04

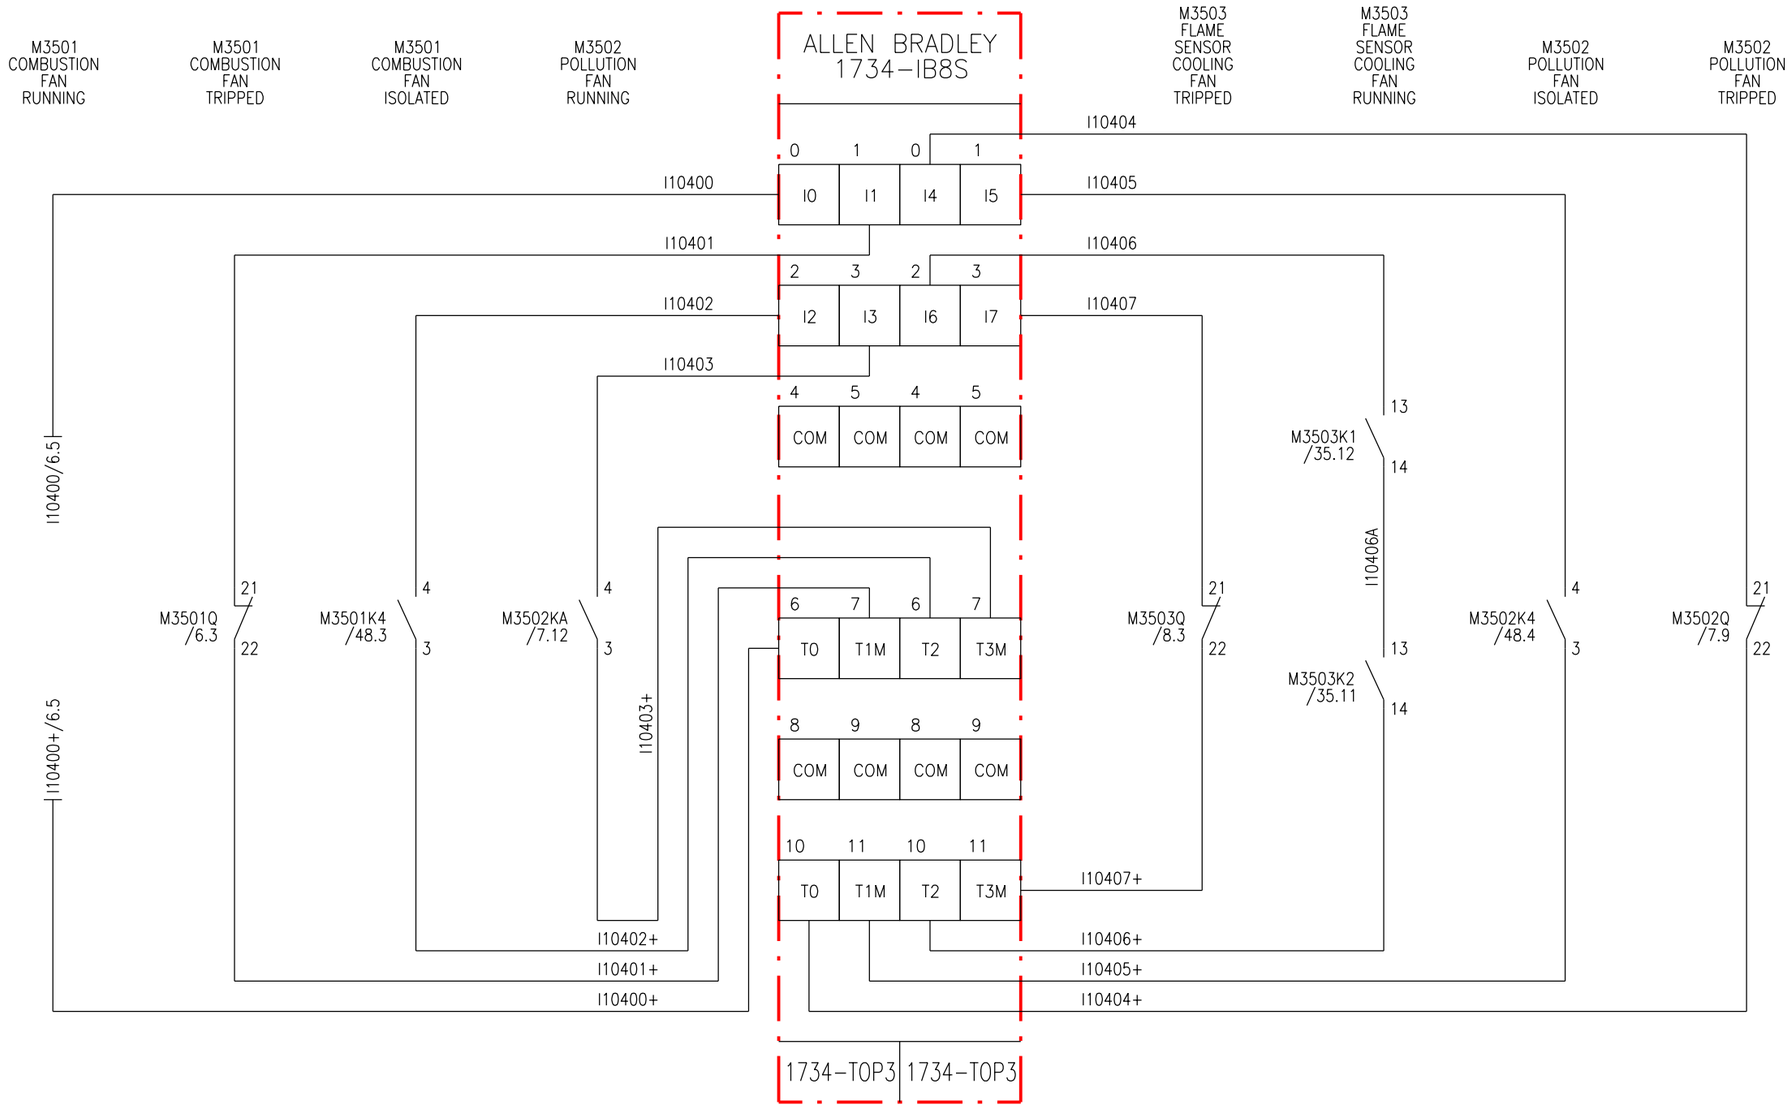

REV	DATE	MODIFICATION	DWN	CHK
1	19/05/14	FOR APPROVAL	MS	DG

ELTEK SYSTEMS LTD
ELTEK HOUSE,
NENE VALLEY BUSINESS PARK
OUNDLE, PETERBOROUGH.PE8 4HN
TEL 01832 277590 FAX 01832 273941
Email: info@eltek-systems.com

TITLE

G4 HEATER PANEL
PC32 LINE 4
WSF, LEICESTER

CLIENT

FLO-MECH LTD FLO-MECH HOUSE,
PAXTON ROAD, ORTON GOLDHAY
PETERBOROUGH.PE2 5YA, ENGLAND.
TEL +44(0)1733233166
FAX +44(0)1733235200
Email: enquiries@flo-mech.com
Internet: www.flo-mech.com

DATE 19/05/14
DWG NO 5620
SHEET 28 OF 55

SAFETY RACK 1 SLOT 05

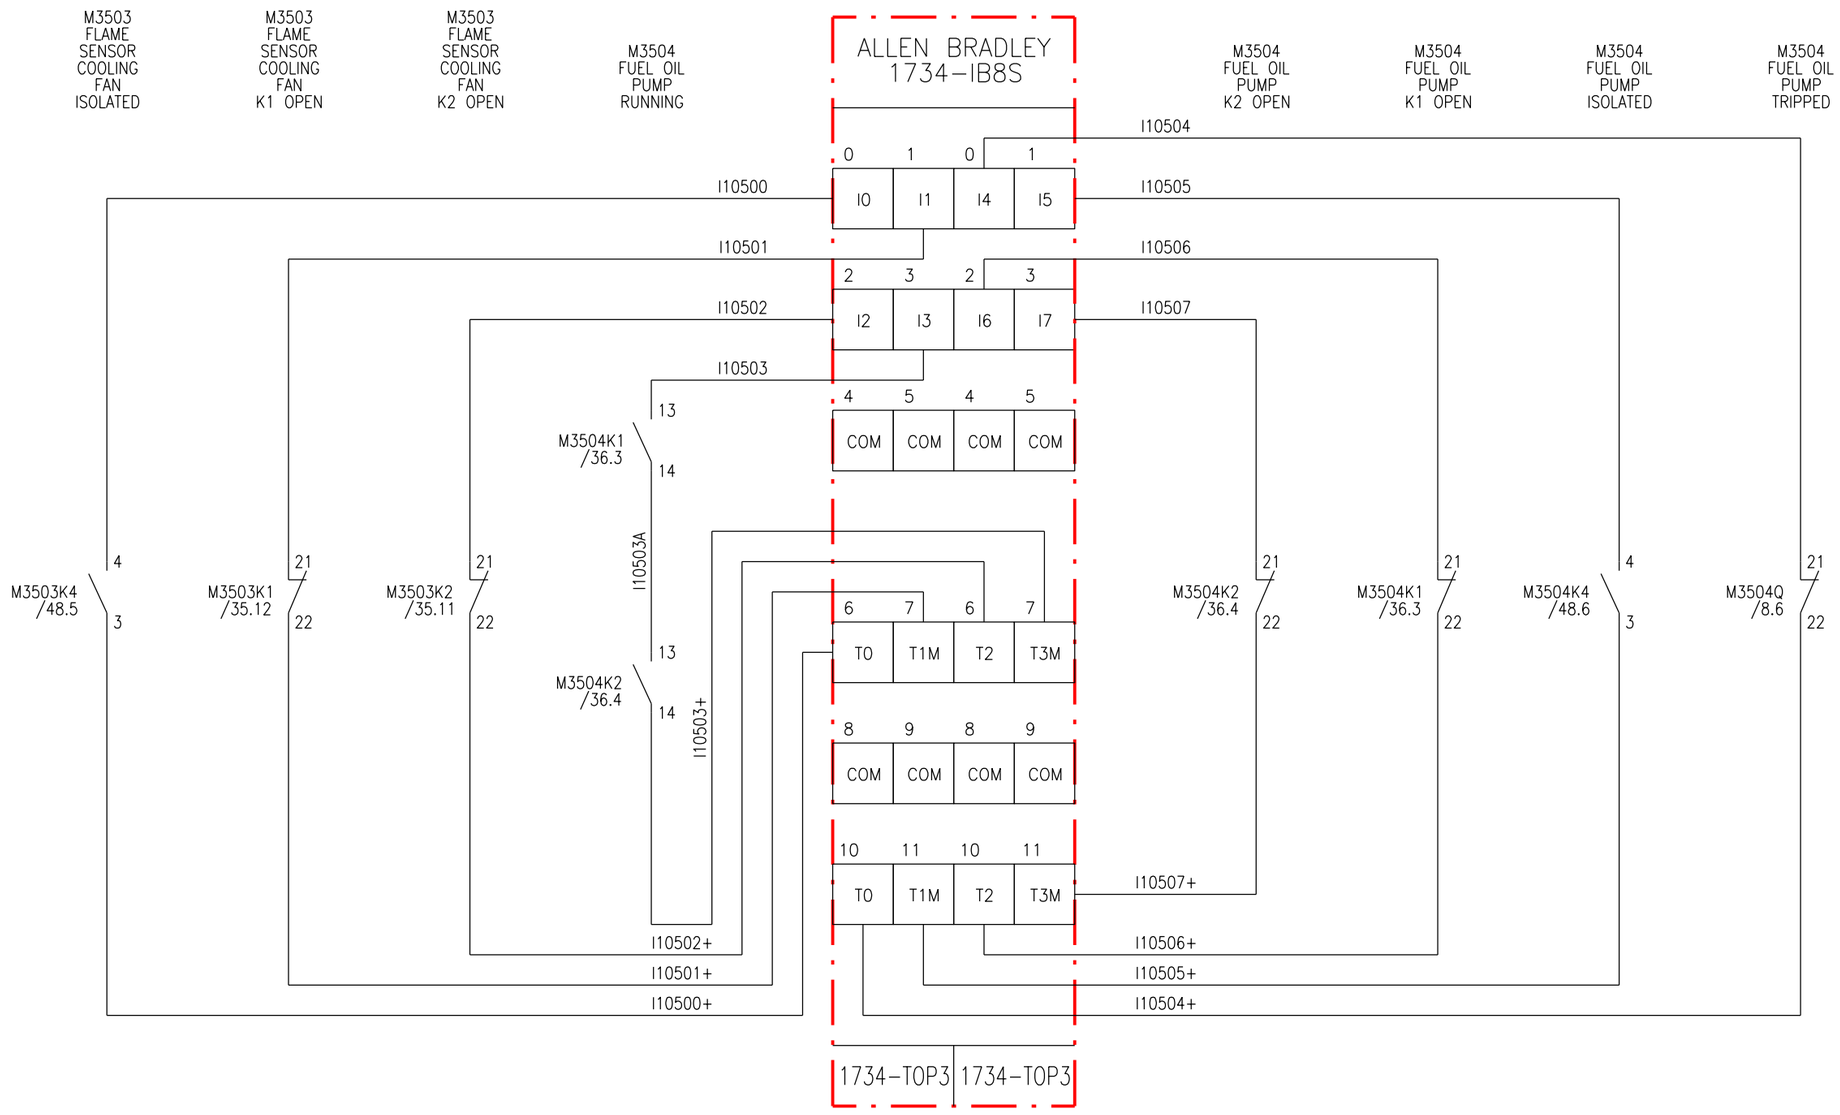

REV	DATE	MODIFICATION	DWN	CHK
1	19/05/14	FOR APPROVAL	MS	DG

ELTEK SYSTEMS LTD
ELTEK HOUSE,
NENE VALLEY BUSINESS PARK
OUNDLE, PETERBOROUGH.PE8 4HN
TEL 01832 277590 FAX 01832 273941
Email: info@eltek-systems.com

TITLE

G4 HEATER PANEL
PC32 LINE 4
WSF, LEICESTER

CLIENT

FLO-MECH LTD FLO-MECH HOUSE,
PAXTON ROAD, ORTON GOLDHAY
PETERBOROUGH.PE2 5YA, ENGLAND.
TEL +44(0)1733233166
FAX +44(0)1733235200
Email: enquiries@flo-mech.com
Internet: www.flo-mech.com

DATE 19/05/14
DWG NO 5620
SHEET 29 OF 55

SAFETY RACK 1 SLOT 06

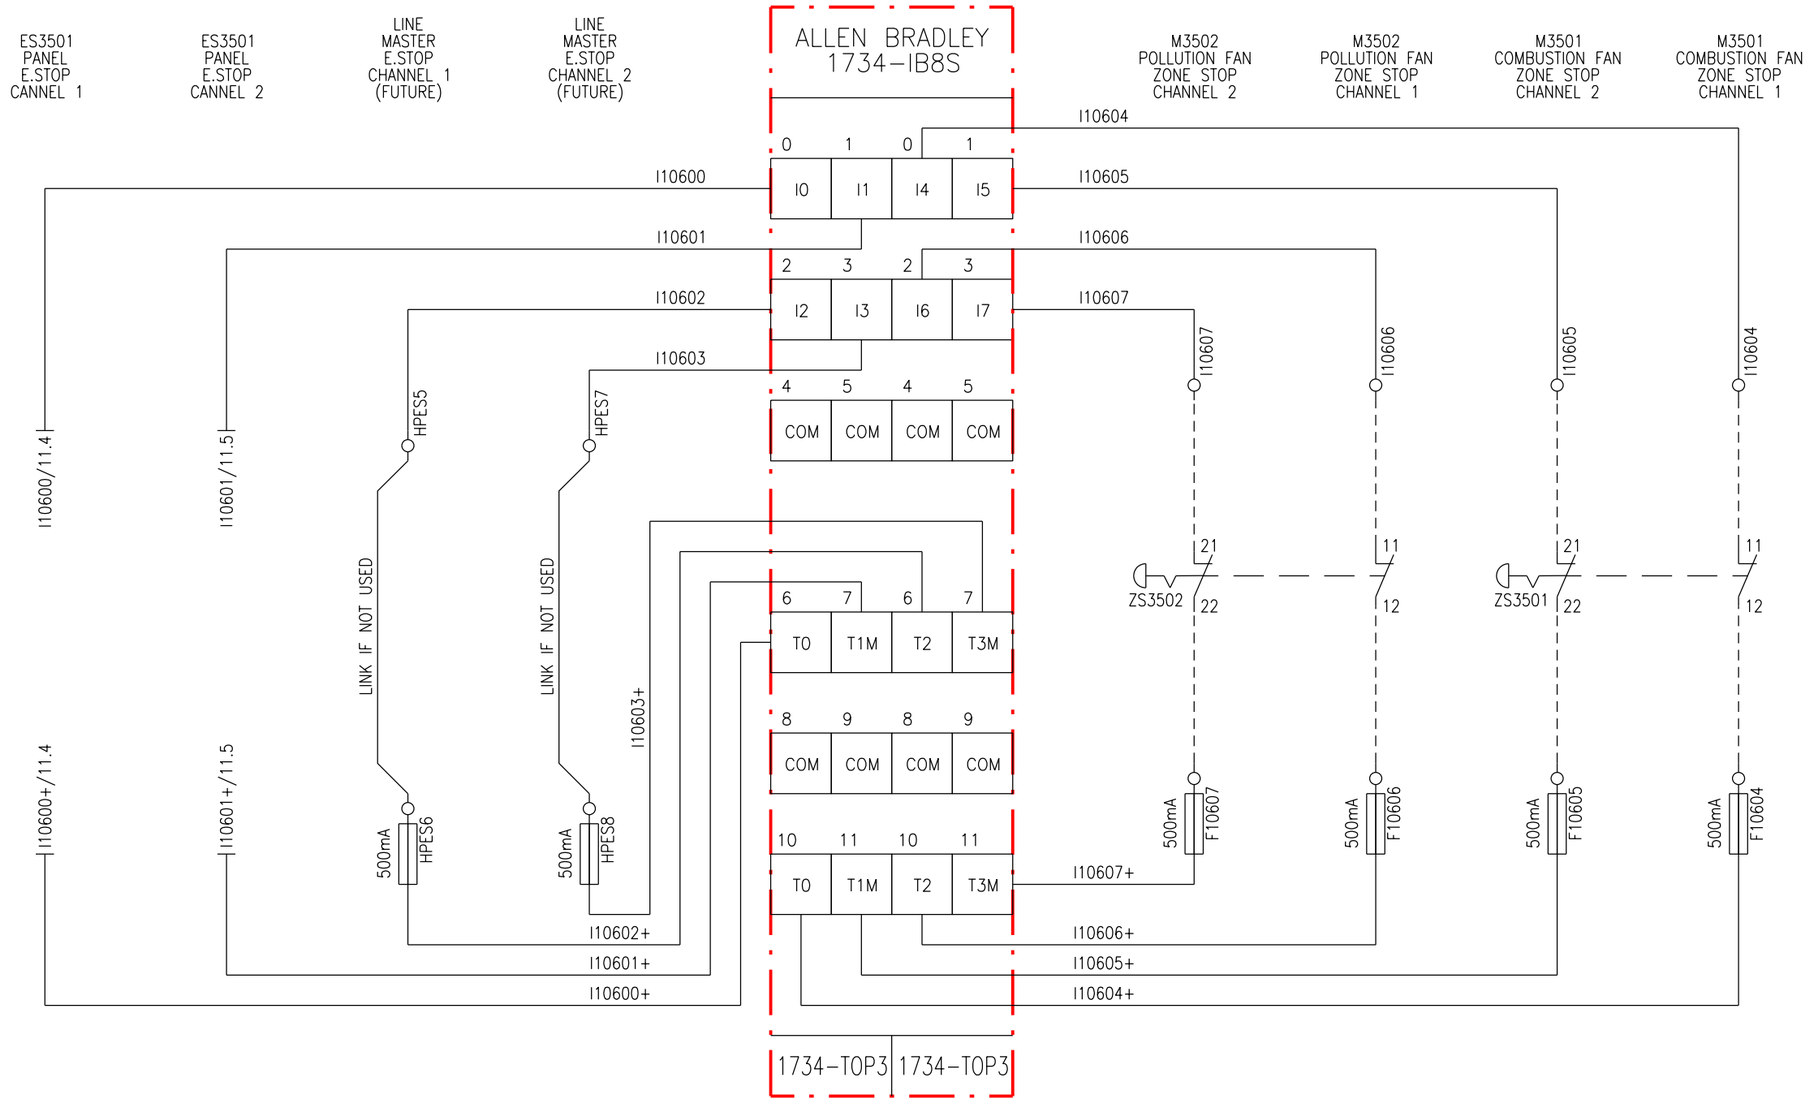

REV	DATE	MODIFICATION	DWN	CHK
1	19/05/14	FOR APPROVAL	MS	DG

ELTEK SYSTEMS LTD
ELTEK HOUSE,
NENE VALLEY BUSINESS PARK
OUNDLE, PETERBOROUGH.PE8 4HN
TEL 01832 277590 FAX 01832 273941
Email: info@eltek-systems.com

TITLE

G4 HEATER PANEL
PC32 LINE 4
WSF, LEICESTER

CLIENT

FLO-MECH LTD FLO-MECH HOUSE,
PAXTON ROAD, ORTON GOLDHAY
PETERBOROUGH.PE2 5YA, ENGLAND.
TEL +44(0)1733233166
FAX +44(0)1733235200
Email: enquiries@flo-mech.com
Internet: www.flo-mech.com

DATE 19/05/14
DWG NO 5620
SHEET 30 OF 55

SAFETY RACK 1 SLOT 07

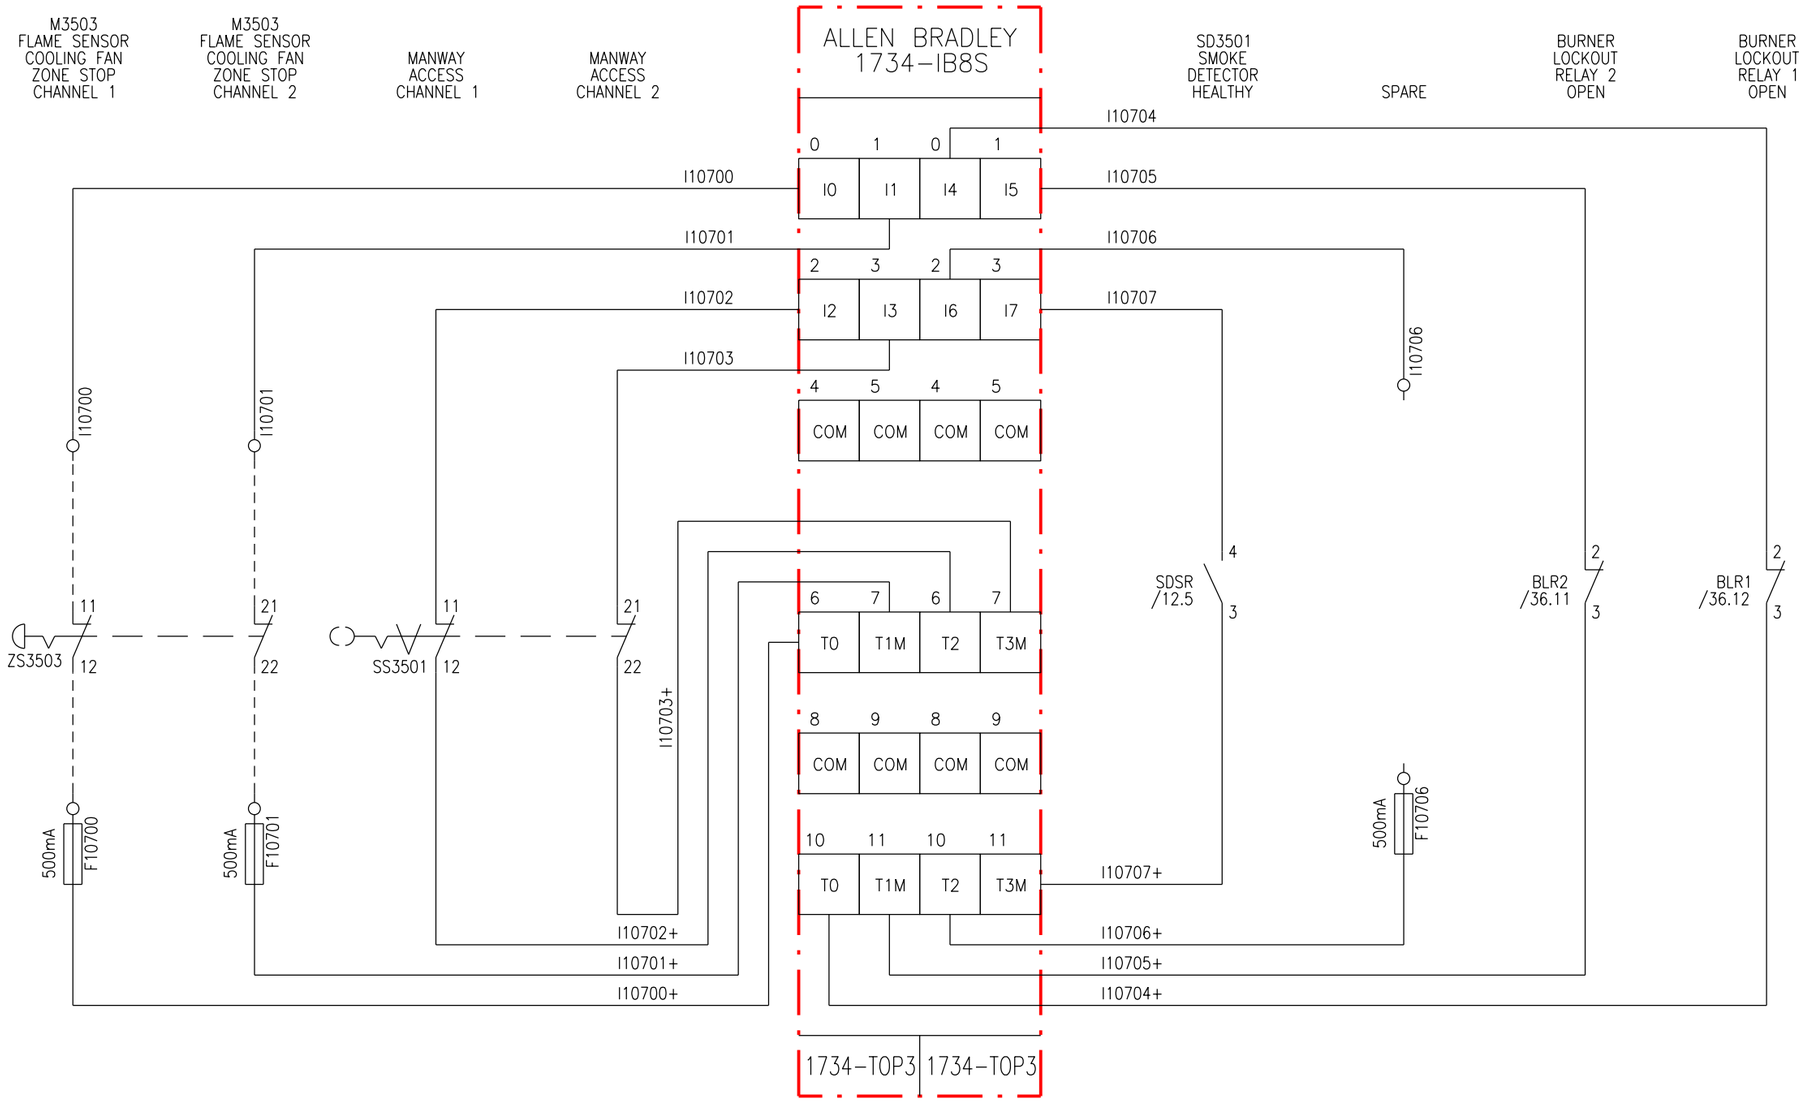

REV	DATE	MODIFICATION	DWN	CHK
1	19/05/14	FOR APPROVAL	MS	DG

ELTEK SYSTEMS LTD
ELTEK HOUSE,
NENE VALLEY BUSINESS PARK
OUNDLE, PETERBOROUGH.PE8 4HN
TEL 01832 277590 FAX 01832 273941
Email: info@eltek-systems.com

TITLE

G4 HEATER PANEL
PC32 LINE 4
WSF, LEICESTER

CLIENT

FLO-MECH LTD FLO-MECH HOUSE,
PAXTON ROAD, ORTON GOLDHAY
PETERBOROUGH.PE2 5YA, ENGLAND.
TEL +44(0)1733233166
FAX +44(0)1733235200
Email: enquiries@flo-mech.com
Internet: www.flo-mech.com

DATE 19/05/14
DWG NO 5620
SHEET 31 OF 55

SAFETY RACK 1 SLOT 08

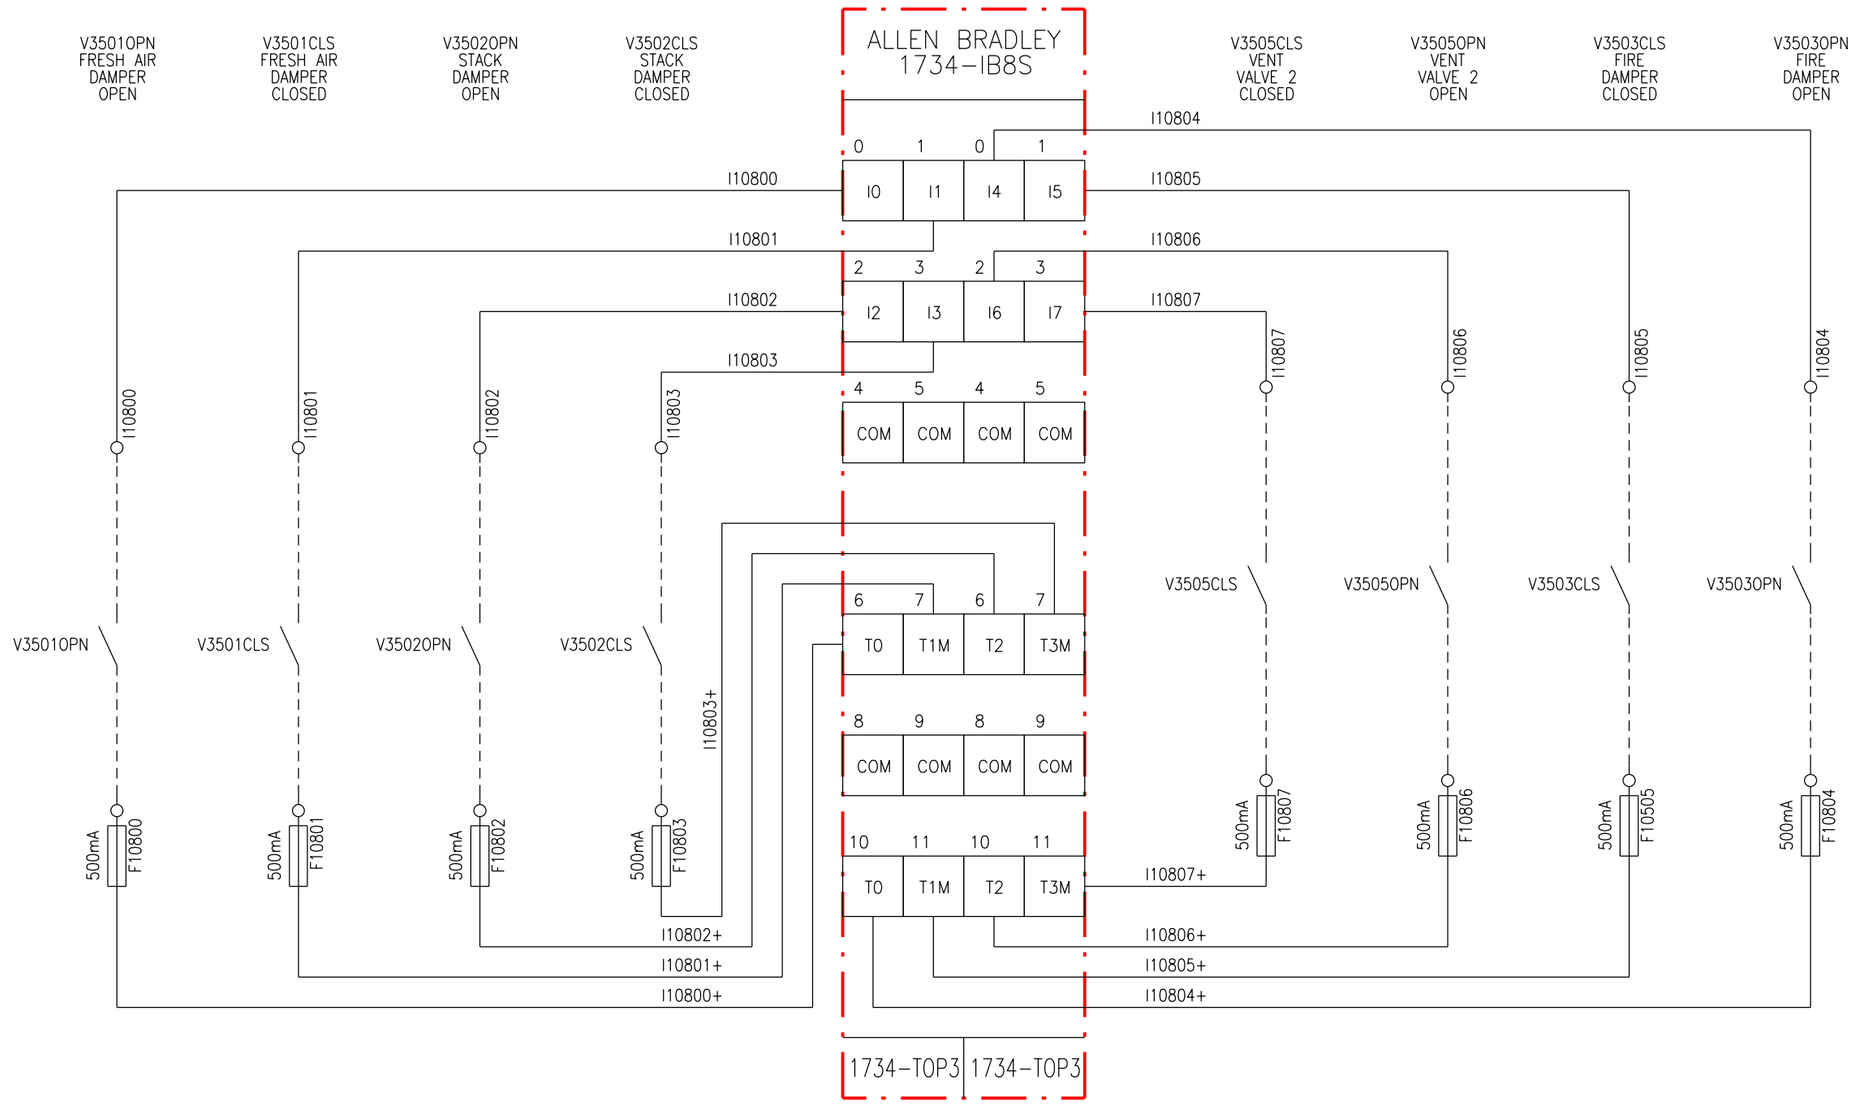

REV	DATE	MODIFICATION	DWN	CHK
1	19/05/14	FOR APPROVAL	MS	DG

ELTEK SYSTEMS Ltd

ELTEK SYSTEMS LTD
ELTEK HOUSE,
NENE VALLEY BUSINESS PARK
OUNDLE, PETERBOROUGH.PE8 4HN
TEL 01832 277590 FAX 01832 273941
Email: info@eltek-systems.com

TITLE

G4 HEATER PANEL
PC32 LINE 4
WSF, LEICESTER

CLIENT

Flo-Mech

FLO-MECH LTD FLO-MECH HOUSE,
PAXTON ROAD, ORTON GOLDHAY
PETERBOROUGH.PE2 5YA, ENGLAND.
TEL +44(0)1733233166
FAX +44(0)1733235200
Email: enquiries@flo-mech.com
Internet: www.flo-mech.com

DATE 19/05/14
DWG NO 5620
SHEET 32 OF 55

SAFETY RACK 1 SLOT 09

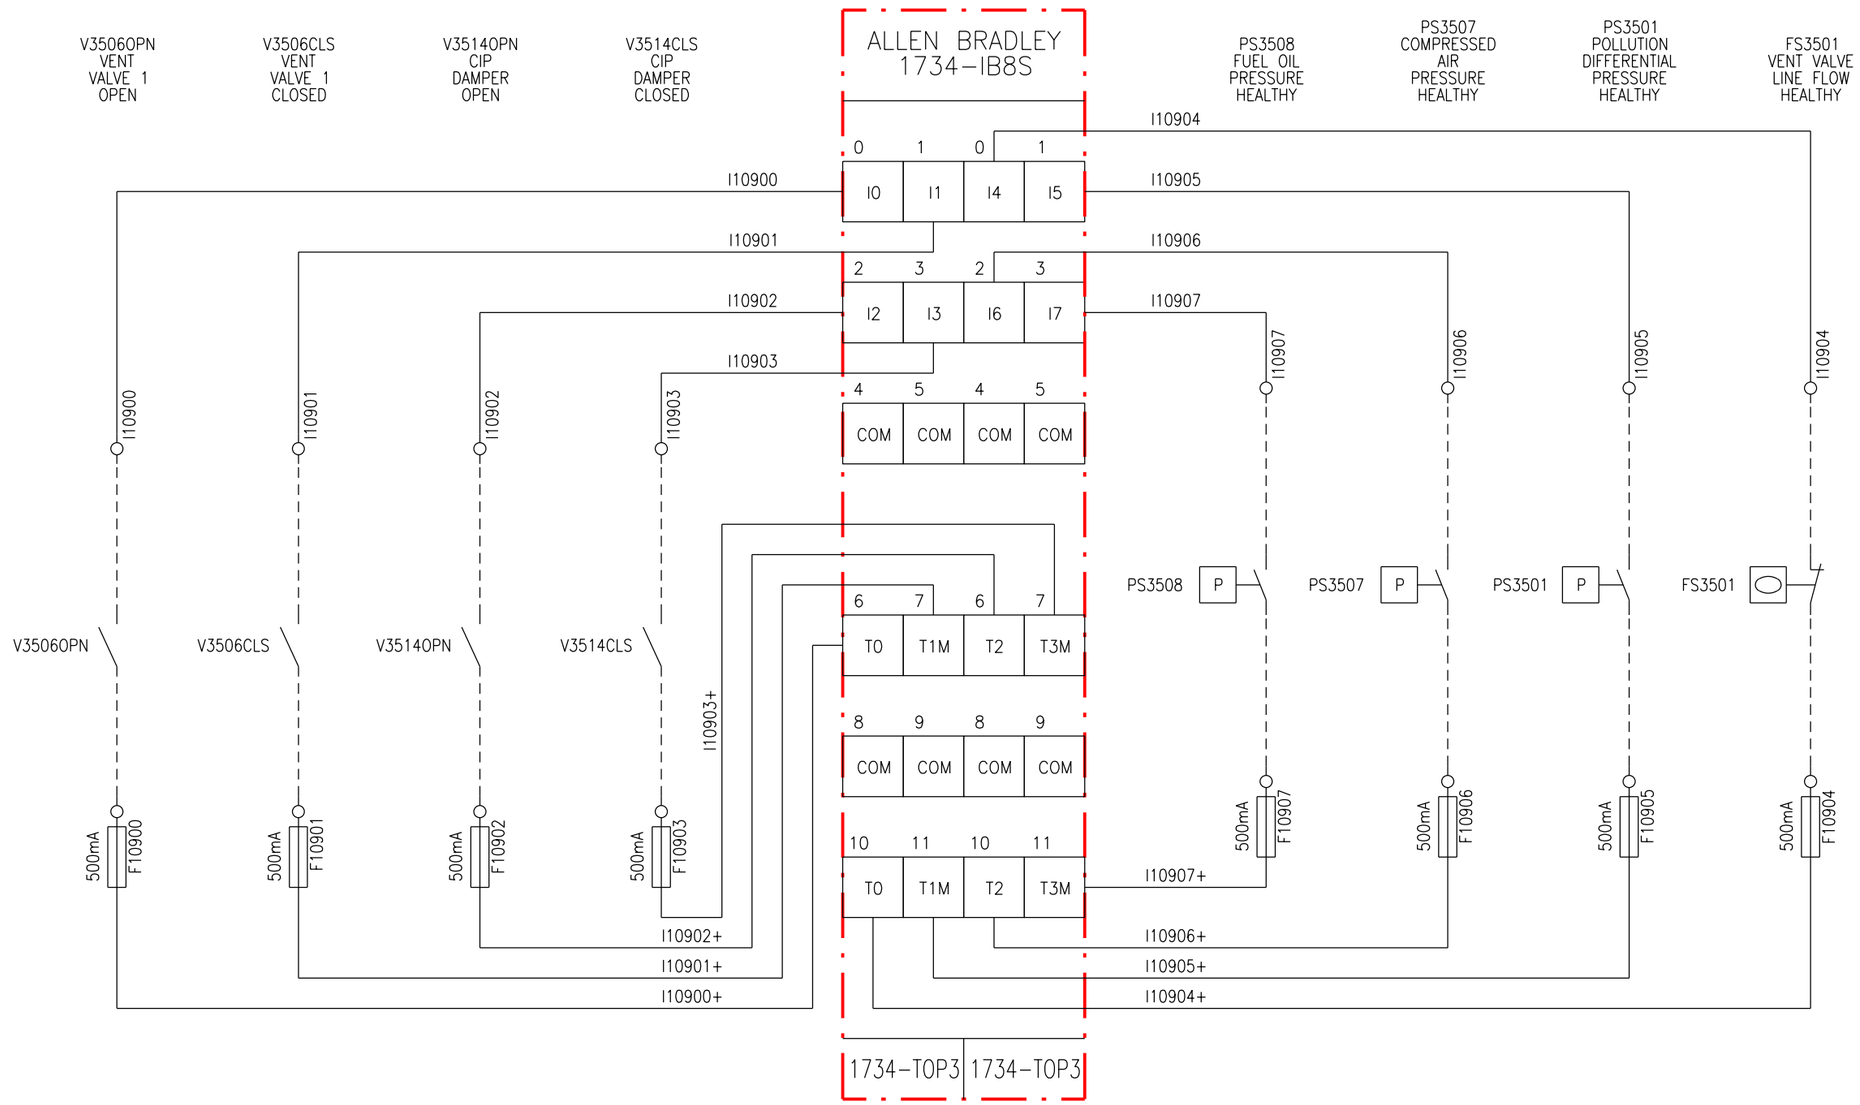

REV	DATE	MODIFICATION	DWN	CHK
1	19/05/14	FOR APPROVAL	MS	DG

ELTEK SYSTEMS Ltd

ELTEK SYSTEMS LTD
ELTEK HOUSE,
NENE VALLEY BUSINESS PARK
OUNDLE, PETERBOROUGH.PE8 4HN
TEL 01832 277590 FAX 01832 273941
Email: info@eltek-systems.com

TITLE

G4 HEATER PANEL
PC32 LINE 4
WSF, LEICESTER

CLIENT

Flo~Mech

FLO-MECH LTD FLO-MECH HOUSE,
PAXTON ROAD, ORTON GOLDHAY
PETERBOROUGH.PE2 5YA, ENGLAND.
TEL +44(0)1733233166
FAX +44(0)1733235200
Email: enquiries@flo-mech.com
Internet: www.flo-mech.com

DATE 19/05/14
DWG NO 5620
SHEET 33 OF 55

SAFETY RACK 1 SLOT 10

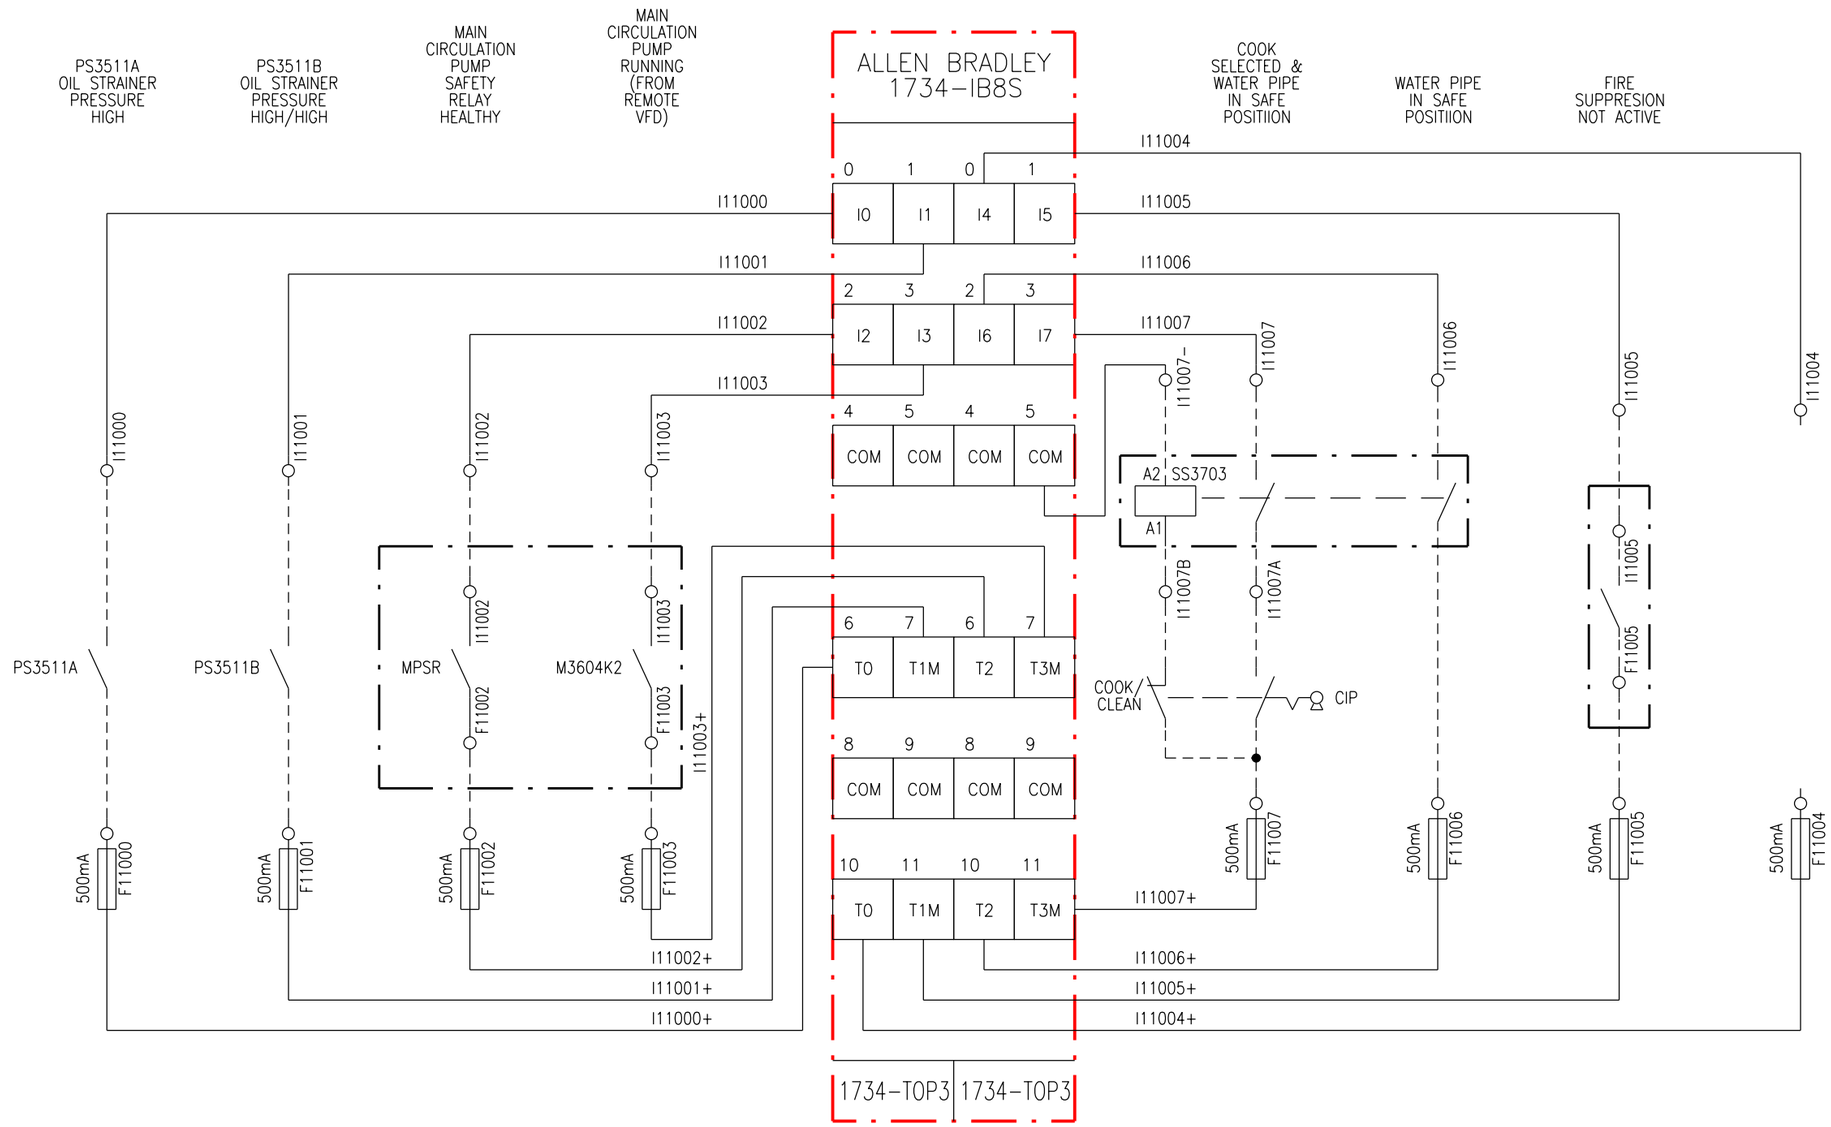

REV	DATE	MODIFICATION	DWN	CHK
1	19/05/14	FOR APPROVAL	MS	DG

ELTEK SYSTEMS Ltd

ELTEK SYSTEMS LTD
ELTEK HOUSE,
NENE VALLEY BUSINESS PARK
OUNDLE, PETERBOROUGH,PE8 4HN
TEL 01832 277590 FAX 01832 273941
Email: info@eltek-systems.com

TITLE

G4 HEATER PANEL
PC32 LINE 4
WSF, LEICESTER

CLIENT

Flo-Mech

FLO-MECH LTD FLO-MECH HOUSE,
PAXTON ROAD, ORTON GOLDHAY
PETERBOROUGH.PE2 5YA, ENGLAND.
TEL +44(0)1733233166
FAX +44(0)1733235200
Email: enquiries@flo-mech.com
Internet: www.flo-mech.com

DATE 19/05/14
DWG NO 5620
SHEET 34 OF 55

SAFETY RACK 1 SLOT 11

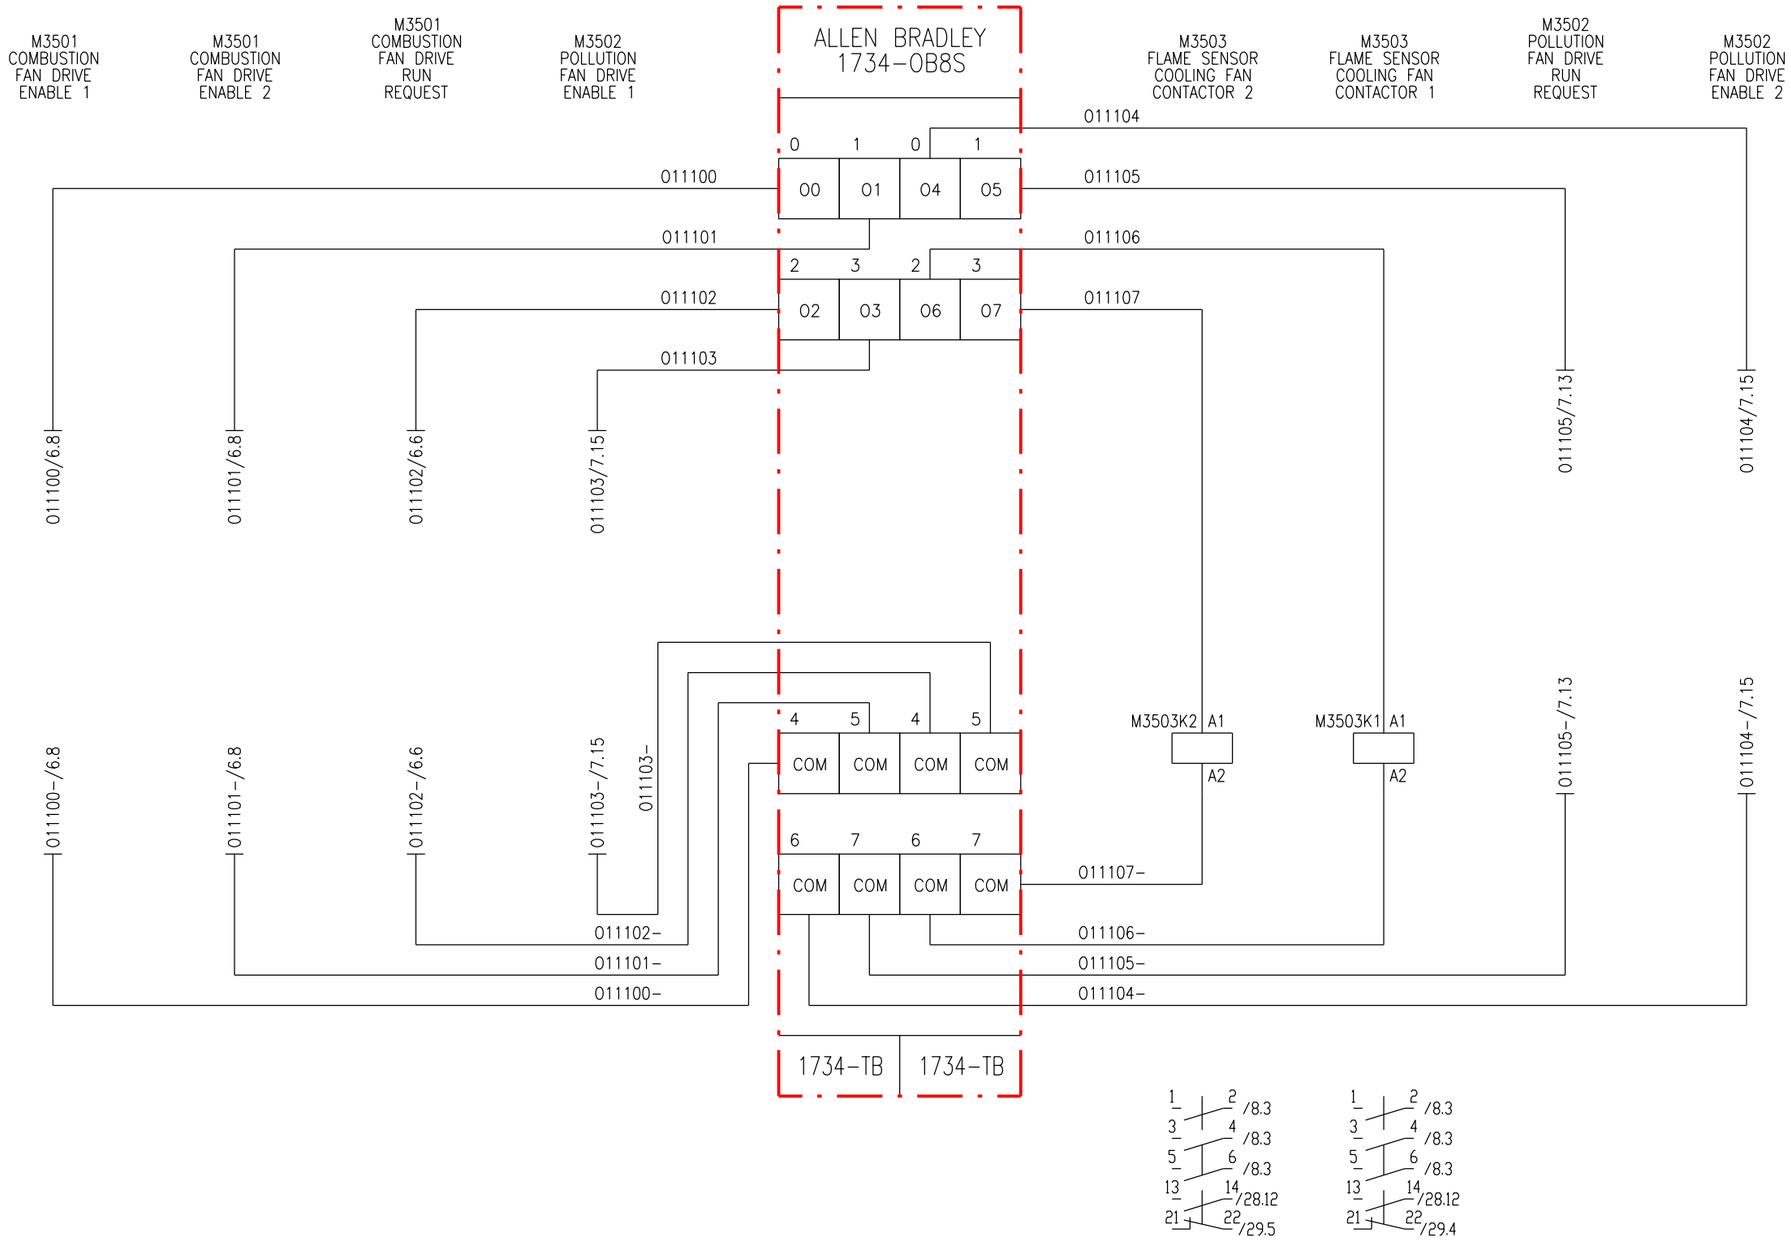

REV	DATE	MODIFICATION	DWN	CHK
1	19/05/14	FOR APPROVAL	MS	DG

ELTEK SYSTEMS LTD
ELTEK HOUSE,
NENE VALLEY BUSINESS PARK
OUNDLE, PETERBOROUGH.PE8 4HN
TEL 01832 277590 FAX 01832 273941
Email: info@eltek-systems.com

TITLE

G4 HEATER PANEL
PC32 LINE 4
WSF, LEICESTER

CLIENT

FLO-MECH LTD FLO-MECH HOUSE,
PAXTON ROAD, ORTON GOLDHAY
PETERBOROUGH.PE2 5YA, ENGLAND.
TEL +44(0)1733233166
FAX +44(0)1733235200
Email: enquiries@flo-mech.com
Internet: www.flo-mech.com

DATE 19/05/14
DWG NO 5620
SHEET 35 OF 55

SAFETY RACK 1 SLOT 12

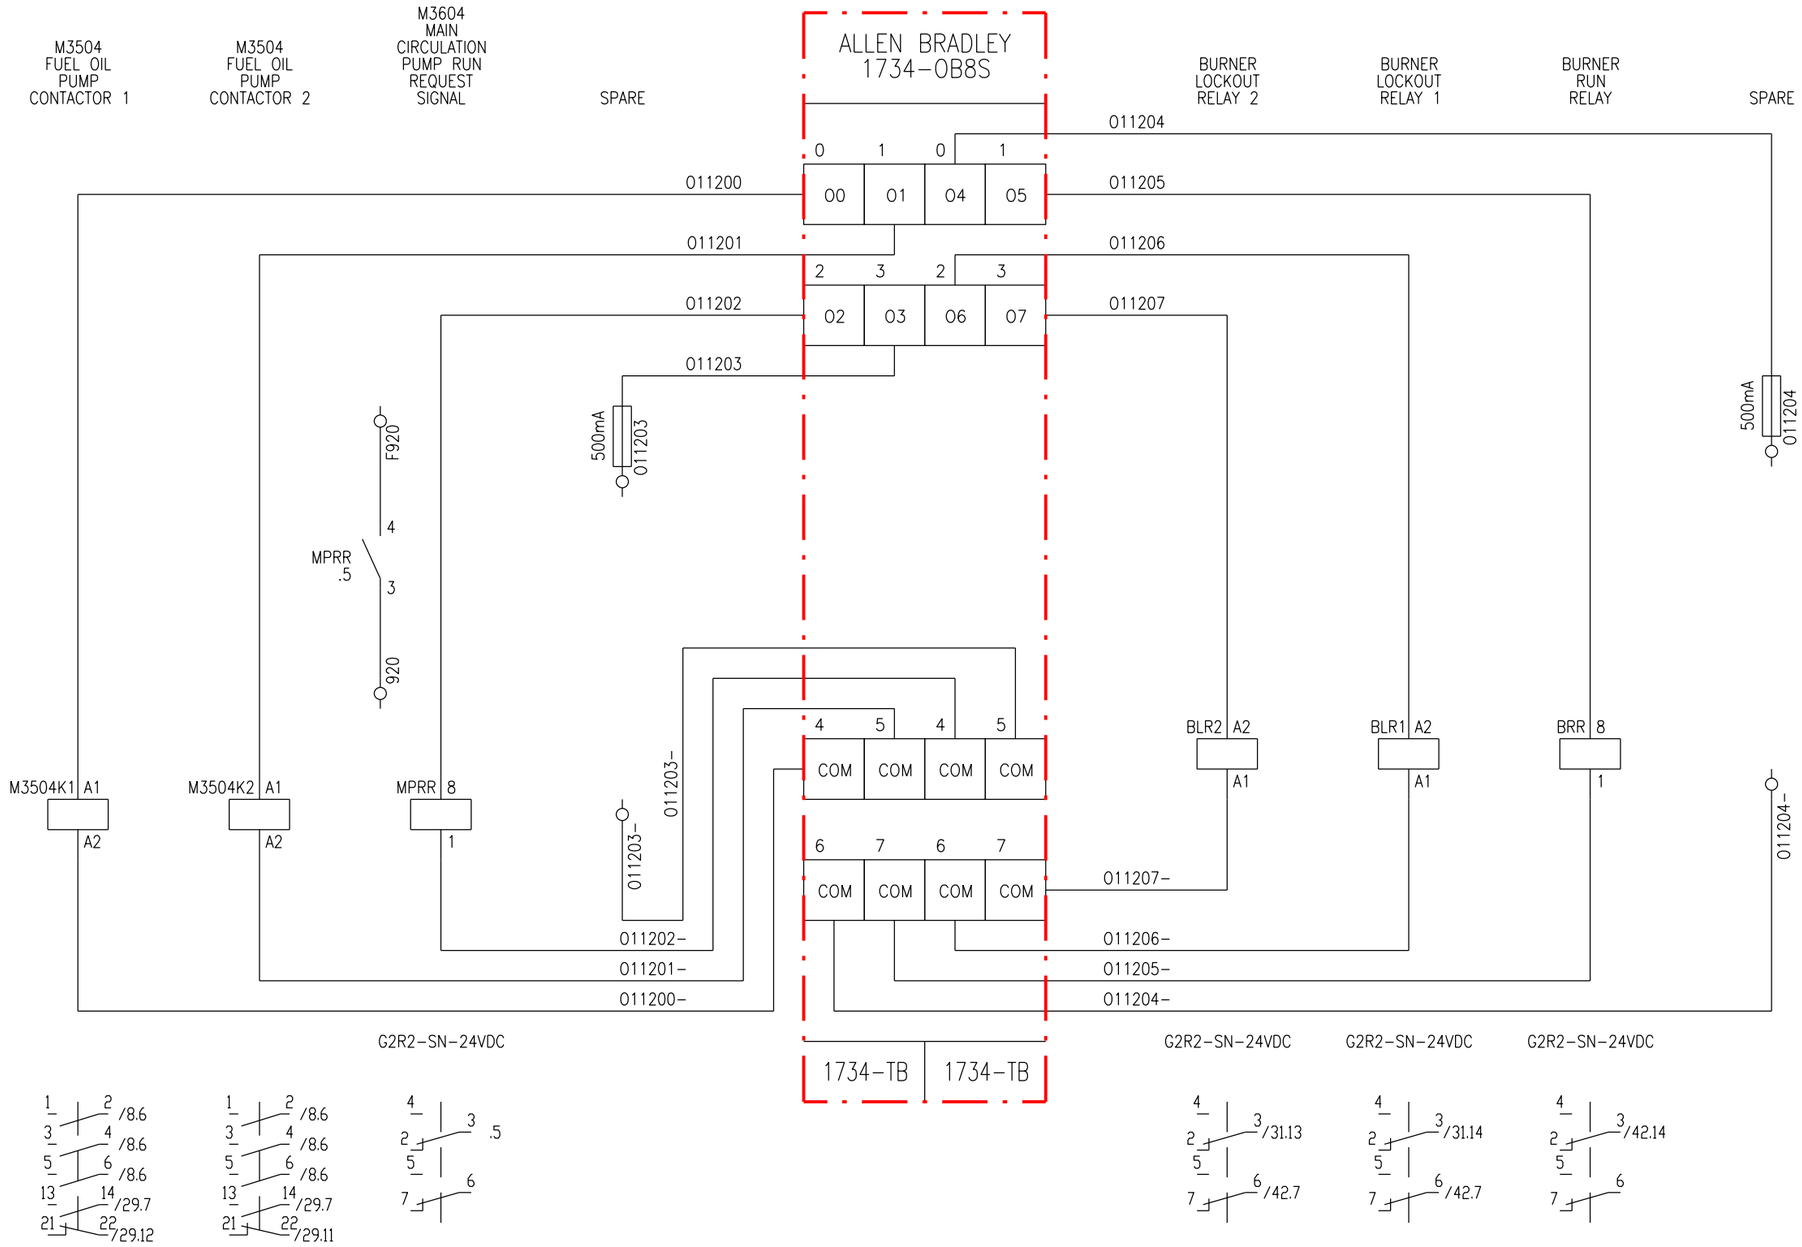

REV	DATE	MODIFICATION	DWN	CHK
1	19/05/14	FOR APPROVAL	MS	DG

ELTEK SYSTEMS Ltd

ELTEK SYSTEMS LTD
ELTEK HOUSE,
NENE VALLEY BUSINESS PARK
OUNDLE, PETERBOROUGH.PE8 4HN
TEL 01832 277590 FAX 01832 273941
Email: info@eltek-systems.com

TITLE

G4 HEATER PANEL
PC32 LINE 4
WSF, LEICESTER

CLIENT

Flo~Mech

FLO-MECH LTD FLO-MECH HOUSE,
PAXTON ROAD, ORTON GOLDHAY
PETERBOROUGH.PE2 5YA, ENGLAND.
TEL +44(0)1733233166
FAX +44(0)1733235200
Email: enquiries@flo-mech.com
Internet: www.flo-mech.com

DATE 19/05/14
DWG NO 5620
SHEET 36 OF 55

SAFETY RACK 1 SLOT 13

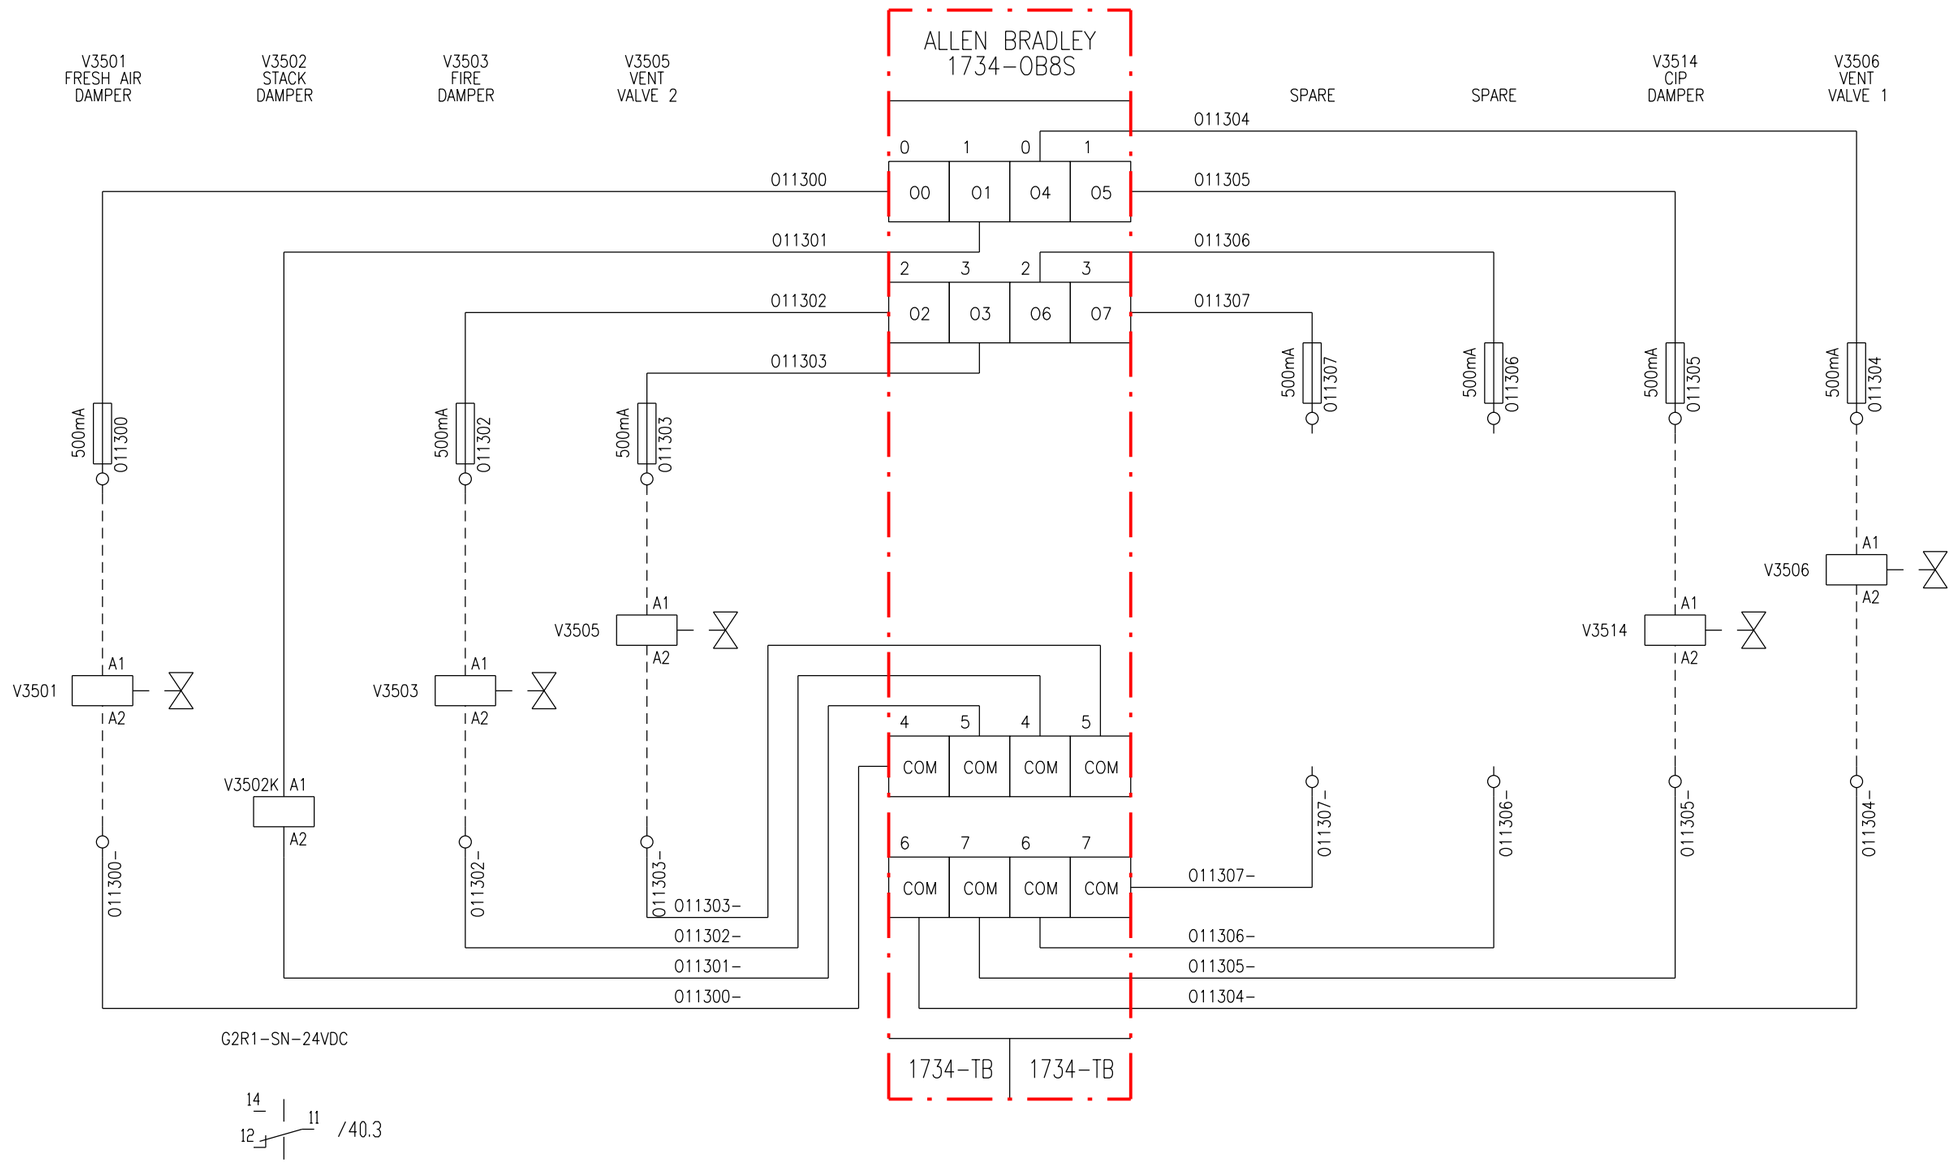

REV	DATE	MODIFICATION	DWN	CHK
1	19/05/14	FOR APPROVAL	MS	DG

ELTEK SYSTEMS Ltd

ELTEK SYSTEMS LTD
ELTEK HOUSE,
NENE VALLEY BUSINESS PARK
OUNDLE, PETERBOROUGH.PE8 4HN
TEL 01832 277590 FAX 01832 273941
Email: info@eltek-systems.com

TITLE

G4 HEATER PANEL
PC32 LINE 4
WSF, LEICESTER

CLIENT

Flo-Mech

FLO-MECH LTD FLO-MECH HOUSE,
PAXTON ROAD, ORTON GOLDHAY
PETERBOROUGH.PE2 5YA, ENGLAND.
TEL +44(0)1733233166
FAX +44(0)1733235200
Email: enquiries@flo-mech.com
Internet: www.flo-mech.com

DATE 19/05/14
DWG NO 5620
SHEET 37 OF 55

1	2	3	4	5	6	7	8	9	10	11	12	13	14	15	16

THIS SHEET IS LEFT BLANK INTENTIONALLY

REV	DATE	MODIFICATION	DWN	CHK
1	19/05/14	FOR APPROVAL	MS	DG

ELTEK SYSTEMS Ltd

ELTEK SYSTEMS LTD
ELTEK HOUSE,
NENE VALLEY BUSINESS PARK
OUNDLE, PETERBOROUGH.PE8 4HN
TEL 01832 277590 FAX 01832 273941
Email: info@eltek-systems.com

TITLE

G4 HEATER PANEL
PC32 LINE 4
WSF, LEICESTER

CLIENT

Flo~Mech

FLO-MECH LTD FLO-MECH HOUSE,
PAXTON ROAD, ORTON GOLDHAY
PETERBOROUGH.PE2 5YA, ENGLAND.
TEL +44(0)1733233166
FAX +44(0)1733235200
Email: enquiries@flo-mech.com
Internet: www.flo-mech.com

DATE 19/05/14
DWG NO 5620
SHEET 38 OF 55

1	2	3	4	5	6	7	8	9	10	11	12	13	14	15	16

THIS SHEET IS LEFT BLANK INTENTIONALLY

REV	DATE	MODIFICATION	DWN	CHK
1	19/05/14	FOR APPROVAL	MS	DG

ELTEK SYSTEMS Ltd

ELTEK SYSTEMS LTD
ELTEK HOUSE,
NENE VALLEY BUSINESS PARK
OUNDLE, PETERBOROUGH.PE8 4HN
TEL 01832 277590 FAX 01832 273941
Email: info@eltek-systems.com

TITLE

G4 HEATER PANEL
PC32 LINE 4
WSF, LEICESTER

CLIENT

Flo~Mech

FLO-MECH LTD FLO-MECH HOUSE,
PAXTON ROAD, ORTON GOLDHAY
PETERBOROUGH.PE2 5YA, ENGLAND.
TEL +44(0)1733233166
FAX +44(0)1733235200
Email: enquiries@flo-mech.com
Internet: www.flo-mech.com

DATE 19/05/14
DWG NO 5620
SHEET 39 OF 55

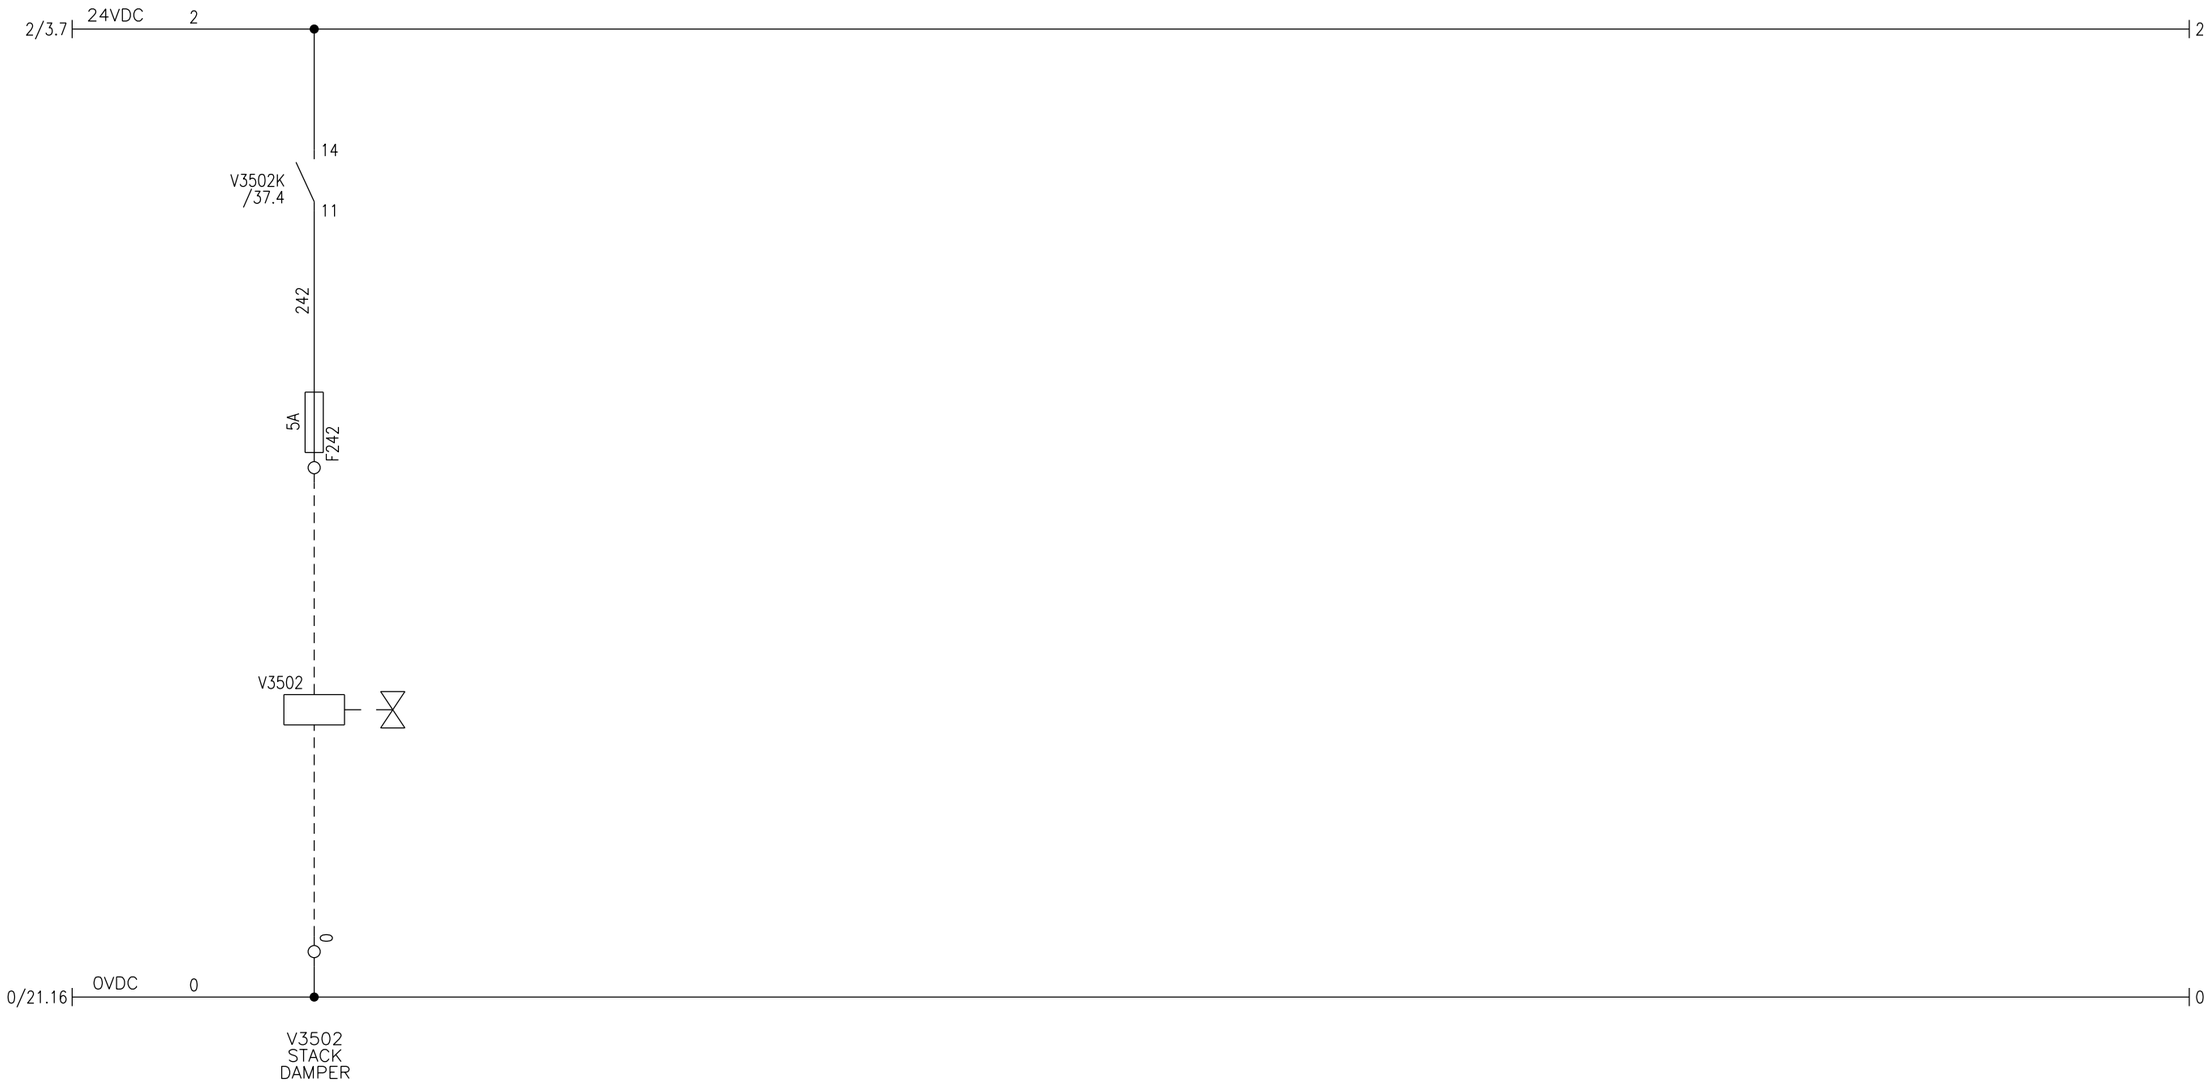

REV	DATE	MODIFICATION	DWN	CHK
1	19/05/14	FOR APPROVAL	MS	DG

ELTEK SYSTEMS Ltd
ELTEK SYSTEMS LTD
ELTEK HOUSE,
NENE VALLEY BUSINESS PARK
OUNDLE, PETERBOROUGH.PE8 4HN
TEL 01832 277590 FAX 01832 273941
Email: info@eltek-systems.com

TITLE

G4 HEATER PANEL
PC32 LINE 4
WSF, LEICESTER

CLIENT

Flo~Mech

FLO-MECH LTD FLO-MECH HOUSE,
PAXTON ROAD, ORTON GOLDHAY
PETERBOROUGH.PE2 5YA, ENGLAND.
TEL +44(0)1733233166
FAX +44(0)1733235200
Email: enquiries@flo-mech.com
Internet: www.flo-mech.com

DATE 19/05/14
DWG NO 5620
SHEET 40 OF 55

1	2	3	4	5	6	7	8	9	10	11	12	13	14	15	16

THIS SHEET IS LEFT BLANK INTENTIONALLY

REV	DATE	MODIFICATION	DWN	CHK
1	19/05/14	FOR APPROVAL	MS	DG

ELTEK SYSTEMS Ltd

ELTEK SYSTEMS LTD
ELTEK HOUSE,
NENE VALLEY BUSINESS PARK
OUNDLE, PETERBOROUGH.PE8 4HN
TEL 01832 277590 FAX 01832 273941
Email: info@eltek-systems.com

TITLE

G4 HEATER PANEL
PC32 LINE 4
WSF, LEICESTER

CLIENT

Flo~Mech

FLO-MECH LTD FLO-MECH HOUSE,
PAXTON ROAD, ORTON GOLDHAY
PETERBOROUGH.PE2 5YA, ENGLAND.
TEL +44(0)1733233166
FAX +44(0)1733235200
Email: enquiries@flo-mech.com
Internet: www.flo-mech.com

DATE 19/05/14
DWG NO 5620
SHEET 41 OF 55

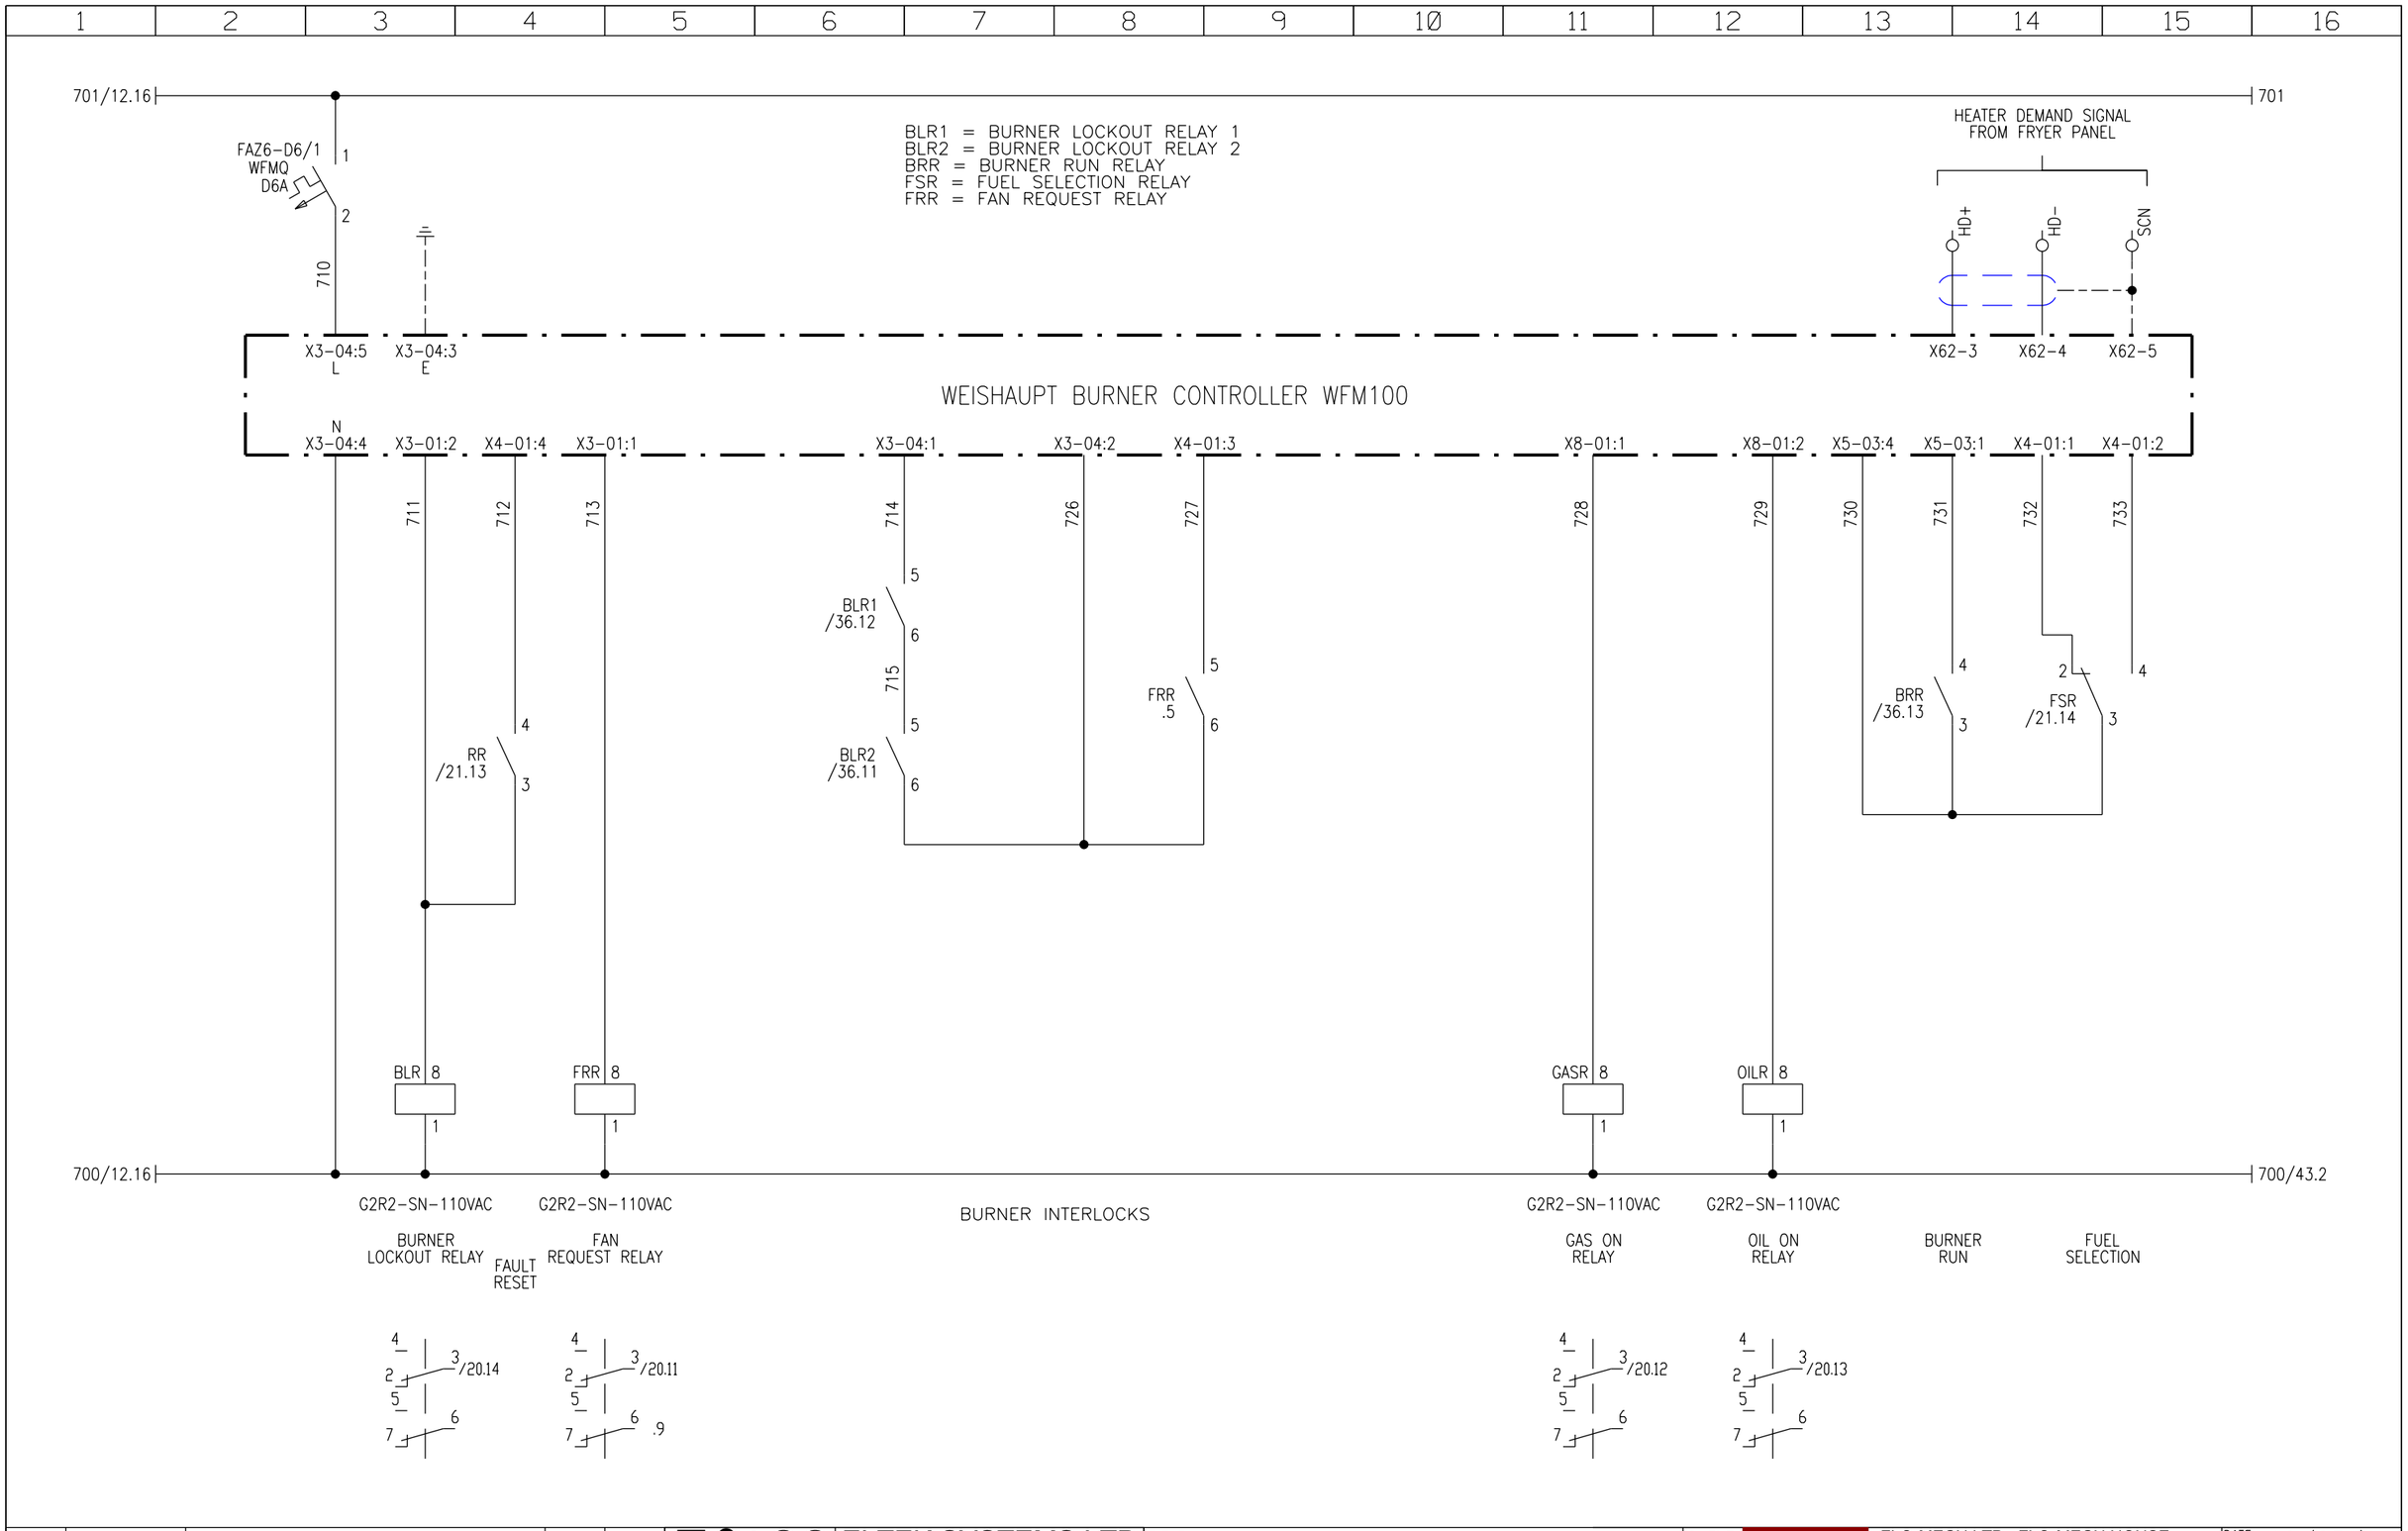

REV	DATE	MODIFICATION	DWN	CHK
1	19/05/14	FOR APPROVAL	MS	DG

ELTEK SYSTEMS Ltd

ELTEK SYSTEMS LTD
ELTEK HOUSE,
NENE VALLEY BUSINESS PARK
OUNDLE, PETERBOROUGH.PE8 4HN
TEL 01832 277590 FAX 01832 273941
Email: info@eltek-systems.com

TITLE

G4 HEATER PANEL
PC32 LINE 4
WSF, LEICESTER

CLIENT

Flo~Mech

FLO-MECH LTD FLO-MECH HOUSE,
PAXTON ROAD, ORTON GOLDHAY
PETERBOROUGH.PE2 5YA, ENGLAND.
TEL +44(0)1733233166
FAX +44(0)1733235200
Email: enquiries@flo-mech.com
Internet: www.flo-mech.com

DATE 19/05/14

DWG NO 5620

SHEET 42 OF 55

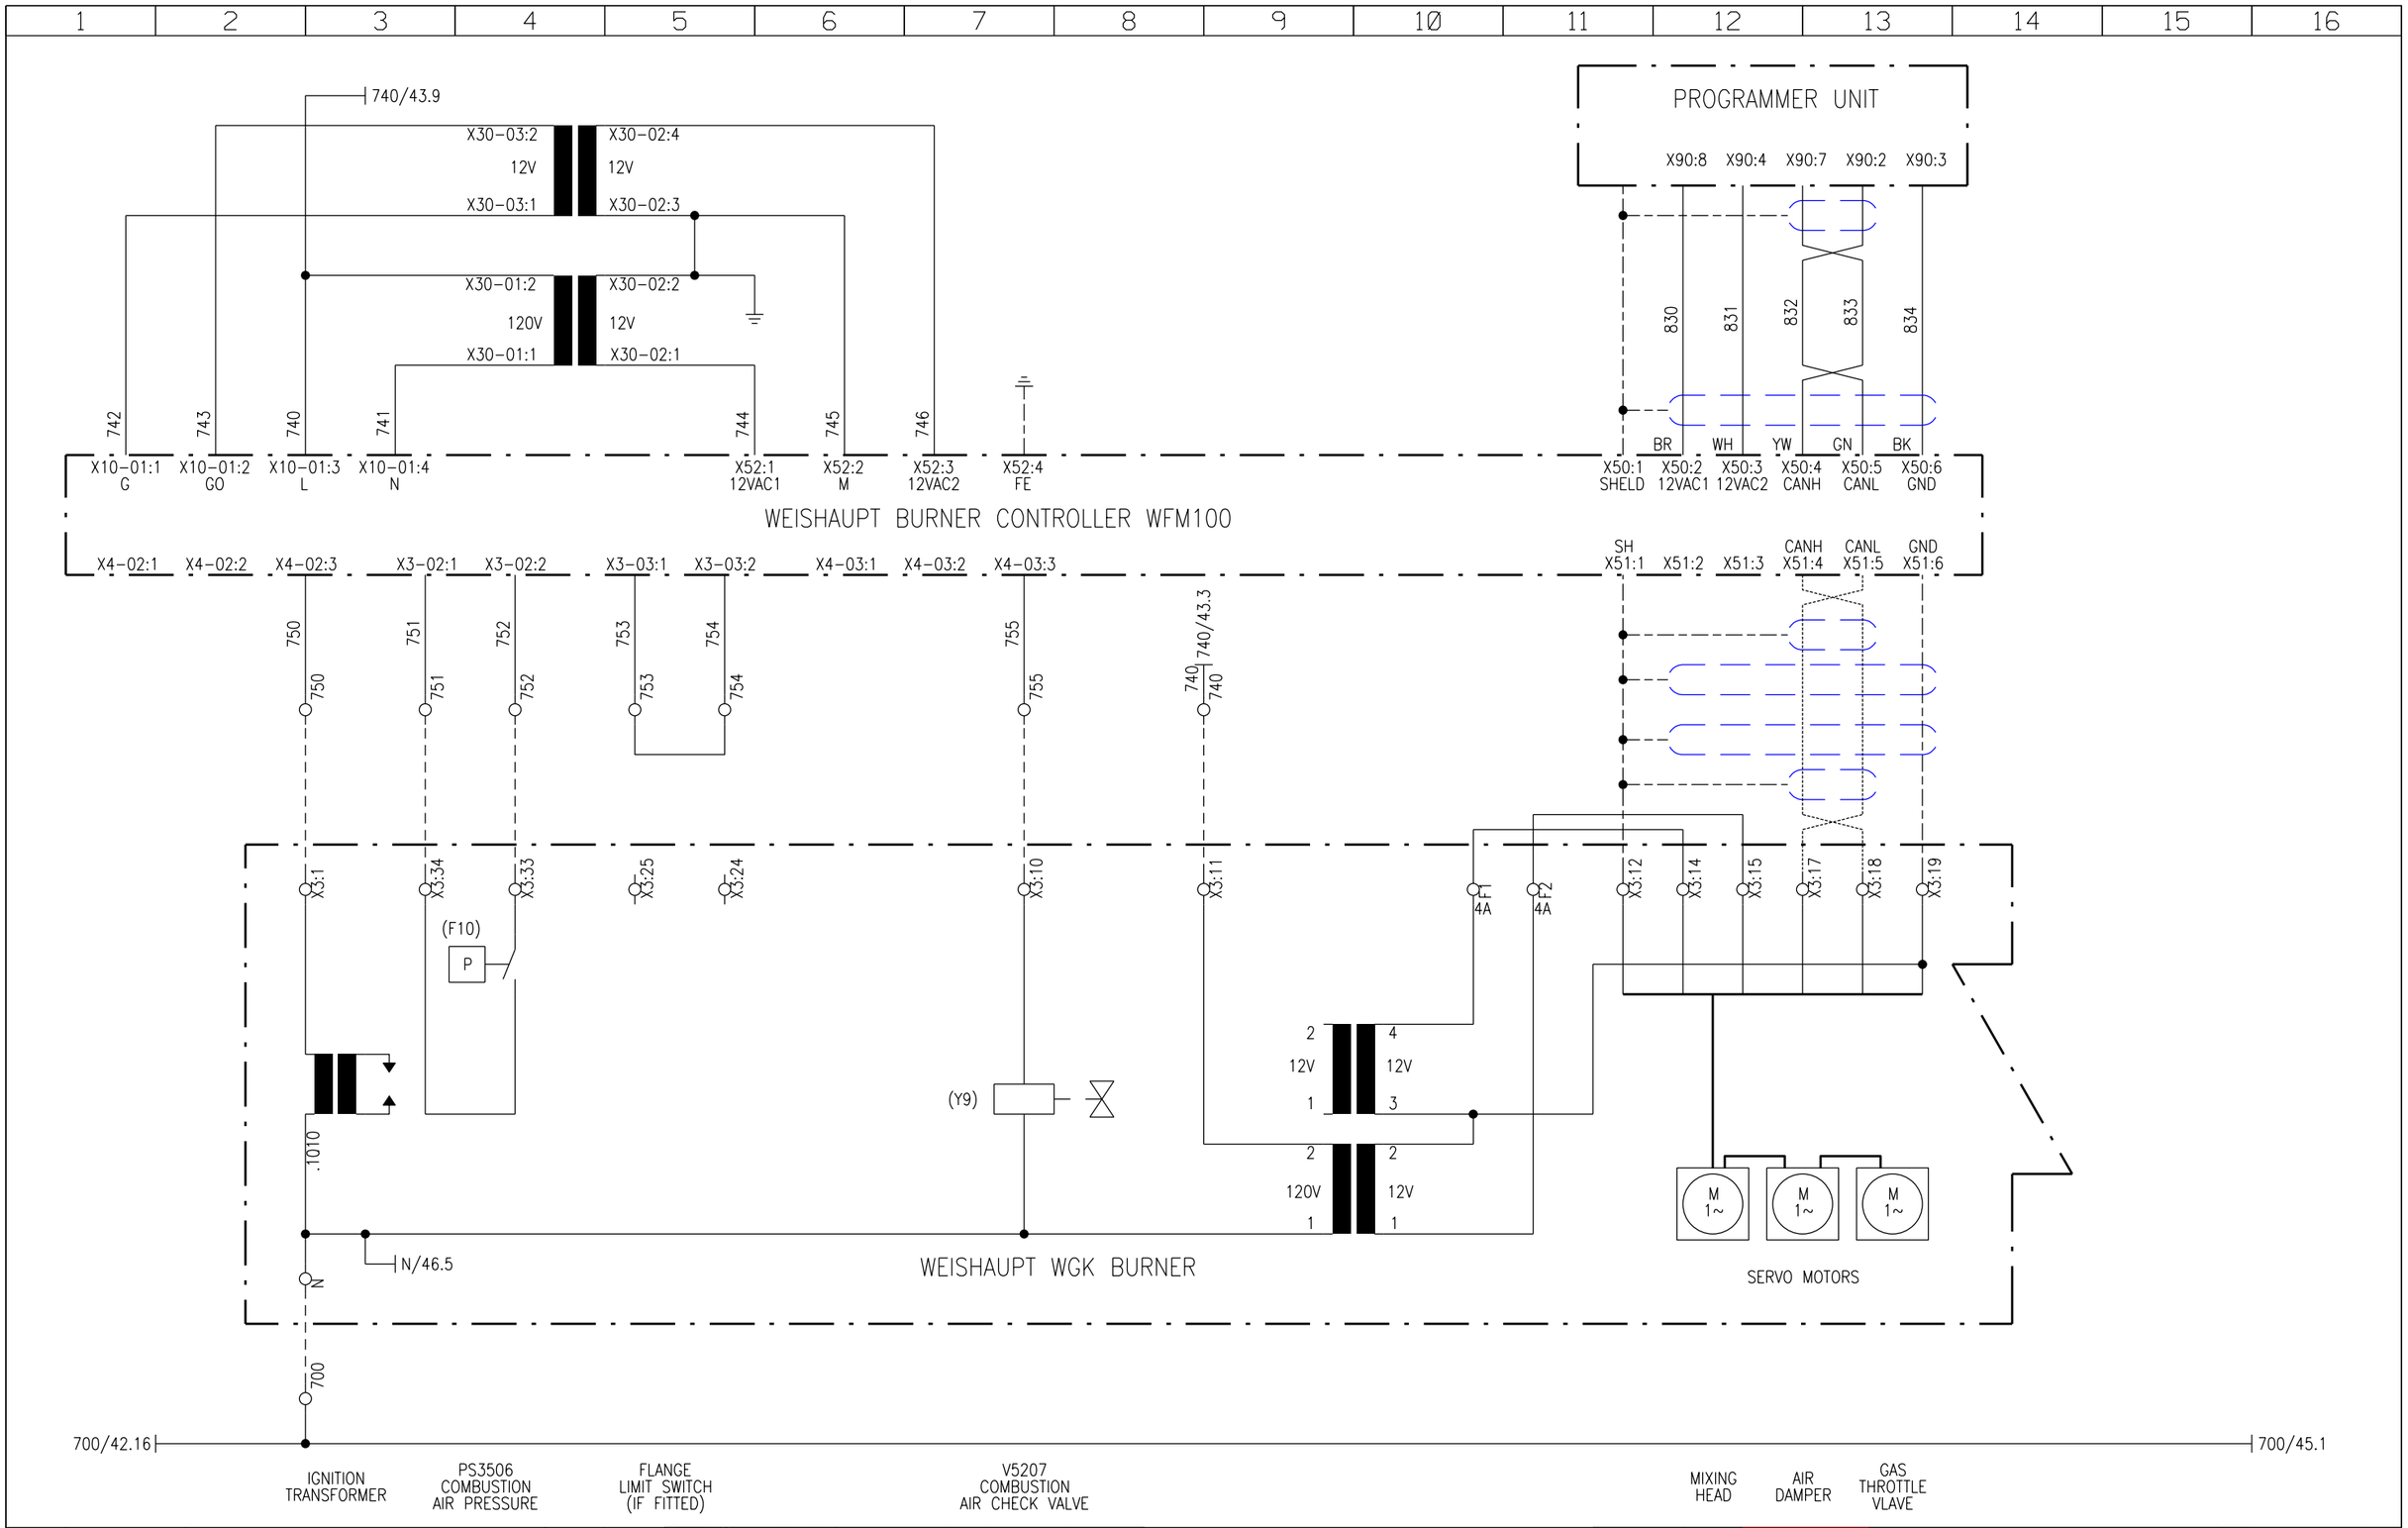

REV	DATE	MODIFICATION	DWN	CHK
1	19/05/14	FOR APPROVAL	MS	DG

ELTEK SYSTEMS Ltd

ELTEK SYSTEMS LTD
ELTEK HOUSE,
NENE VALLEY BUSINESS PARK
OUNDLE, PETERBOROUGH.PE8 4HN
TEL 01832 277590 FAX 01832 273941
Email: info@eltek-systems.com

TITLE

G4 HEATER PANEL
PC32 LINE 4
WSF, LEICESTER

CLIENT

Flo~Mech

FLO-MECH LTD FLO-MECH HOUSE,
PAXTON ROAD, ORTON GOLDHAY
PETERBOROUGH.PE2 5YA, ENGLAND.
TEL +44(0)1733233166
FAX +44(0)1733235200
Email: enquiries@flo-mech.com
Internet: www.flo-mech.com

DATE 19/05/14
DWG NO 5620
SHEET 43 OF 55

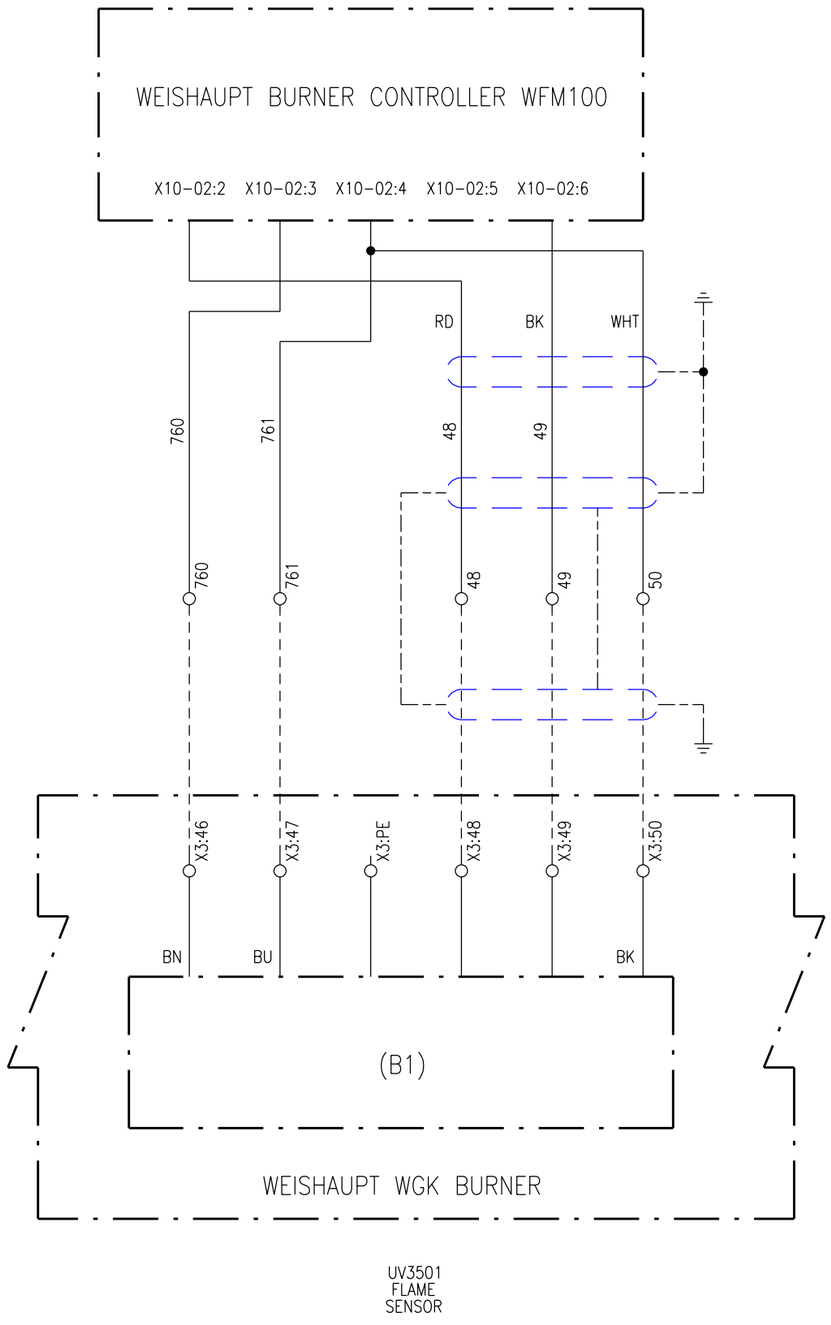

REV	DATE	MODIFICATION	DWN	CHK
1	19/05/14	FOR APPROVAL	MS	DG

ELTEK SYSTEMS Ltd
ELTEK SYSTEMS LTD
ELTEK HOUSE,
NENE VALLEY BUSINESS PARK
OUNDLE, PETERBOROUGH,PE8 4HN
TEL 01832 277590 FAX 01832 273941
Email: info@eltek-systems.com

TITLE

G4 HEATER PANEL
PC32 LINE 4
WSF, LEICESTER

CLIENT

Flo~Mech

FLO-MECH LTD FLO-MECH HOUSE,
PAXTON ROAD, ORTON GOLDHAY
PETERBOROUGH.PE2 5YA, ENGLAND.
TEL +44(0)1733233166
FAX +44(0)1733235200
Email: enquiries@flo-mech.com
Internet: www.flo-mech.com

DATE 19/05/14
DWG NO 5620
SHEET 44 OF 55

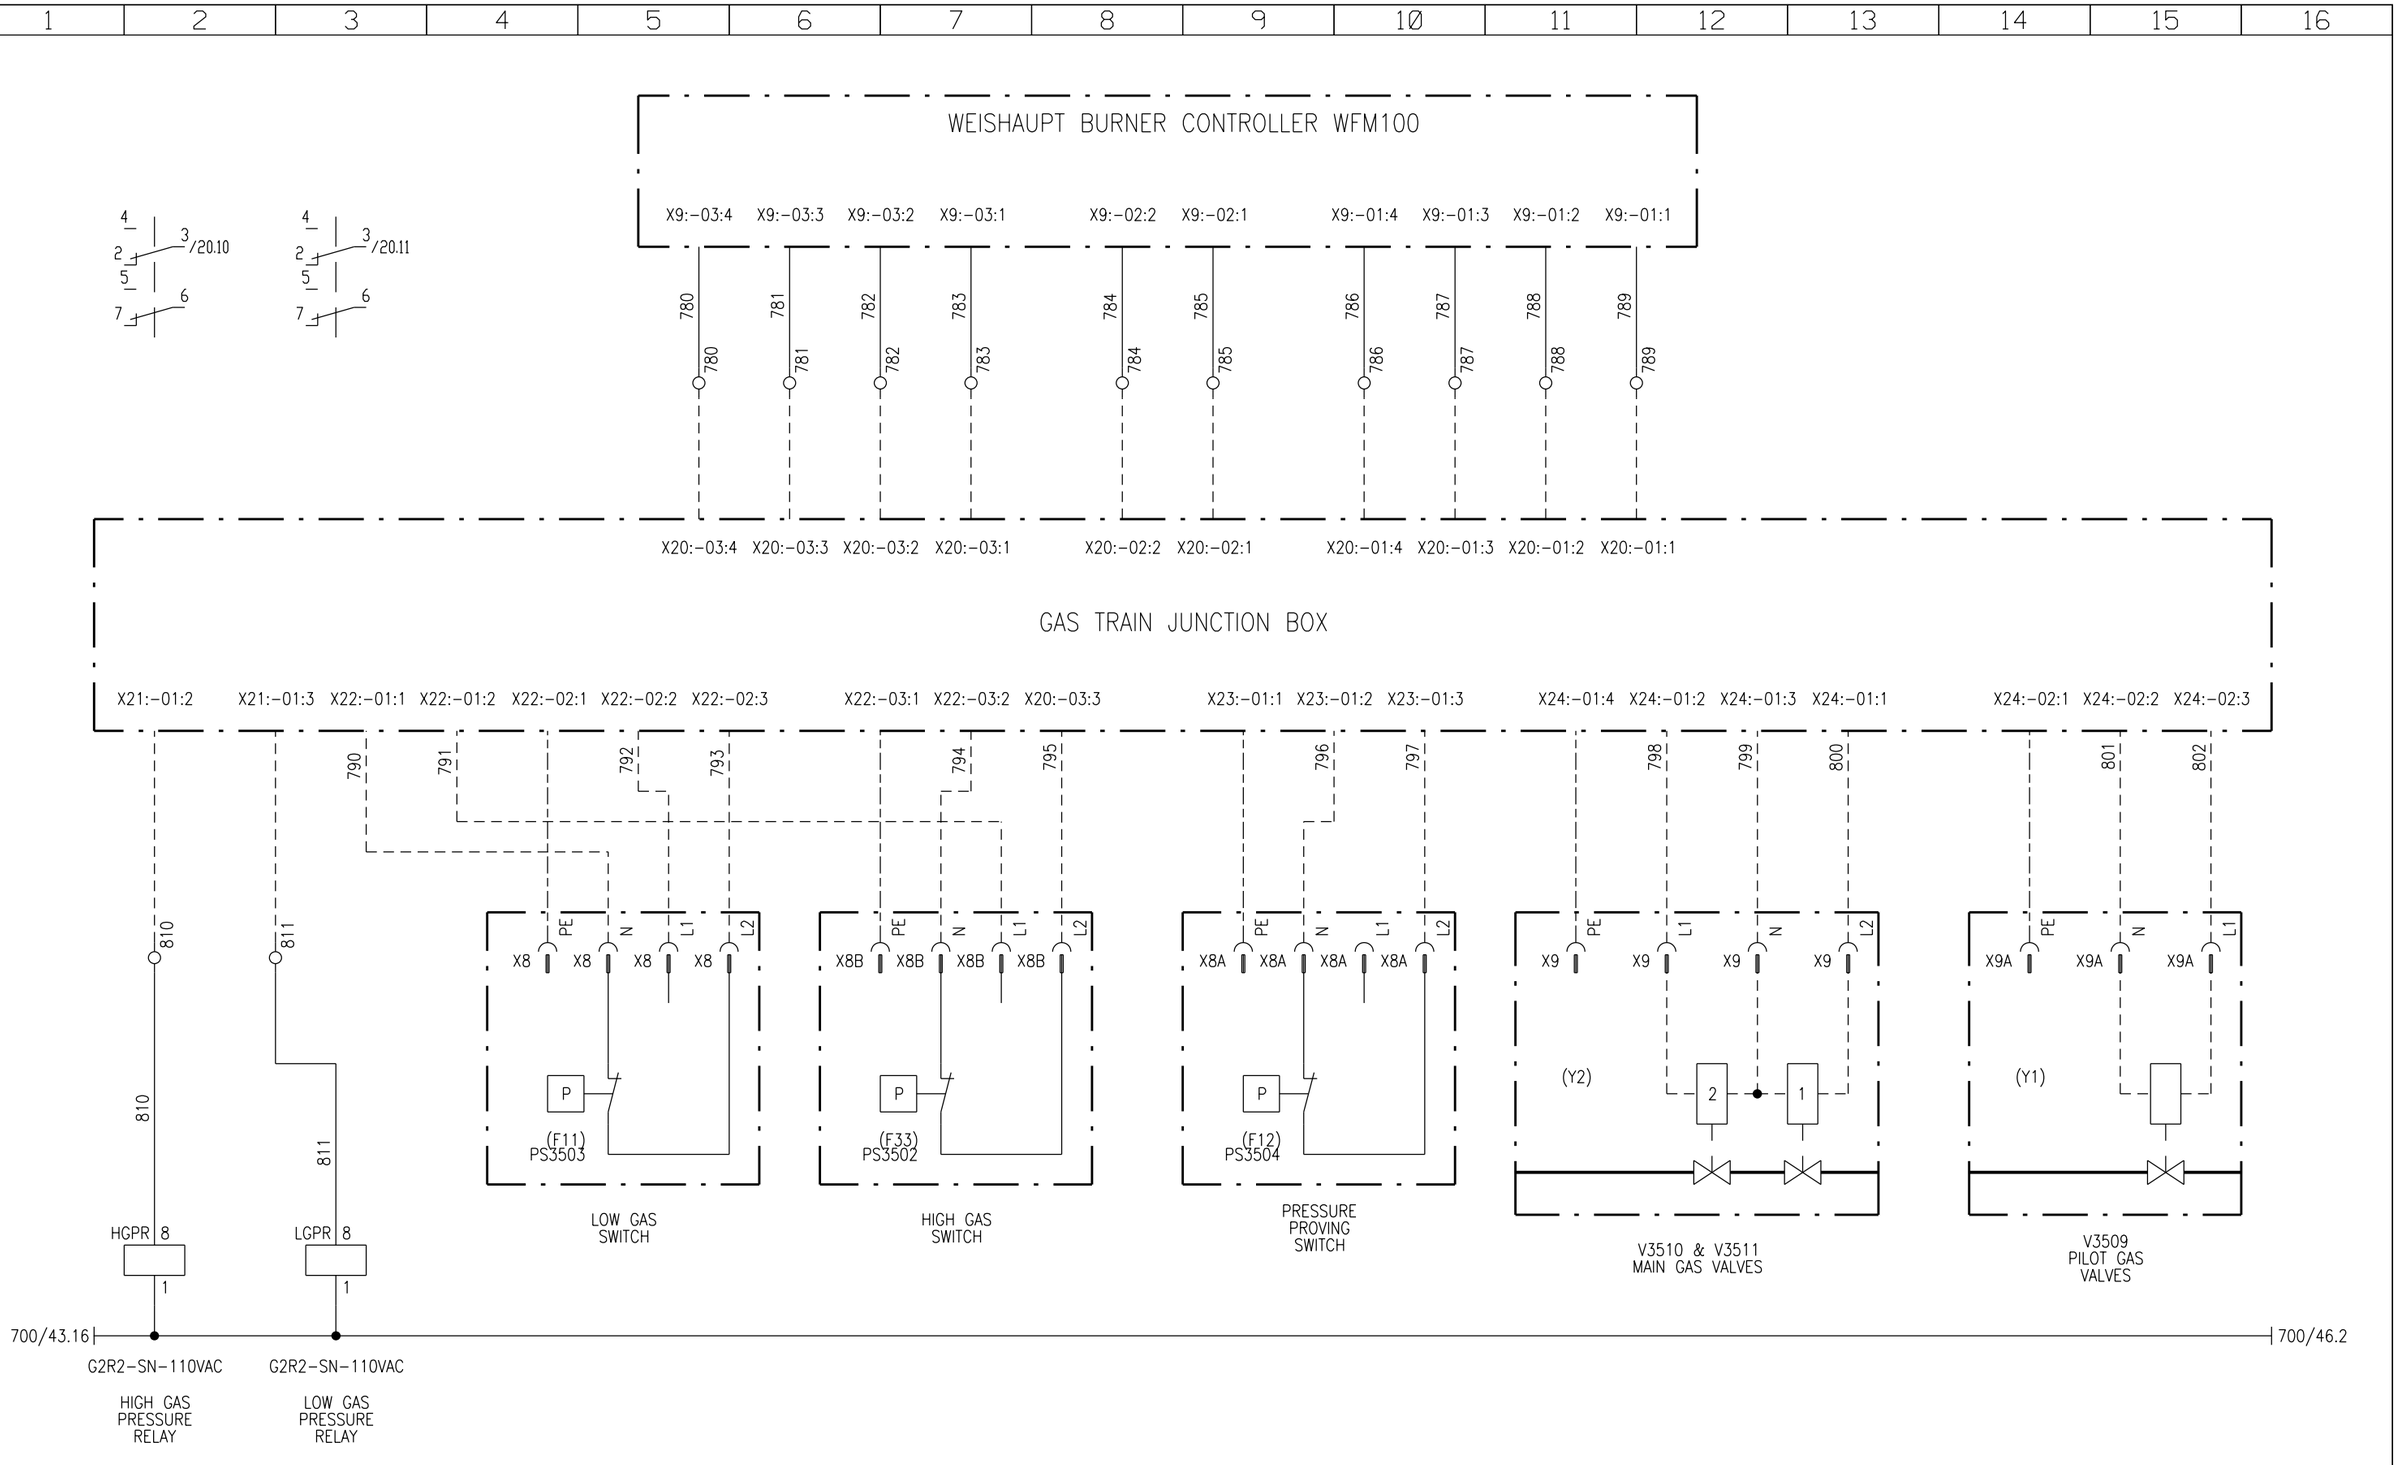

REV	DATE	MODIFICATION	DWN	CHK
1	19/05/14	FOR APPROVAL	MS	DG

ELTEK SYSTEMS Ltd
ELTEK SYSTEMS LTD
ELTEK HOUSE,
NENE VALLEY BUSINESS PARK
OUNDLE, PETERBOROUGH.PE8 4HN
TEL 01832 277590 FAX 01832 273941
Email: info@eltek-systems.com

TITLE

G4 HEATER PANEL
PC32 LINE 4
WSF, LEICESTER

CLIENT

Flo-Mech

FLO-MECH LTD FLO-MECH HOUSE,
PAXTON ROAD, ORTON GOLDHAY
PETERBOROUGH.PE2 5YA, ENGLAND.
TEL +44(0)1733233166
FAX +44(0)1733235200
Email: enquiries@flo-mech.com
Internet: www.flo-mech.com

DATE 19/05/14
DWG NO 5620
SHEET 45 OF 55

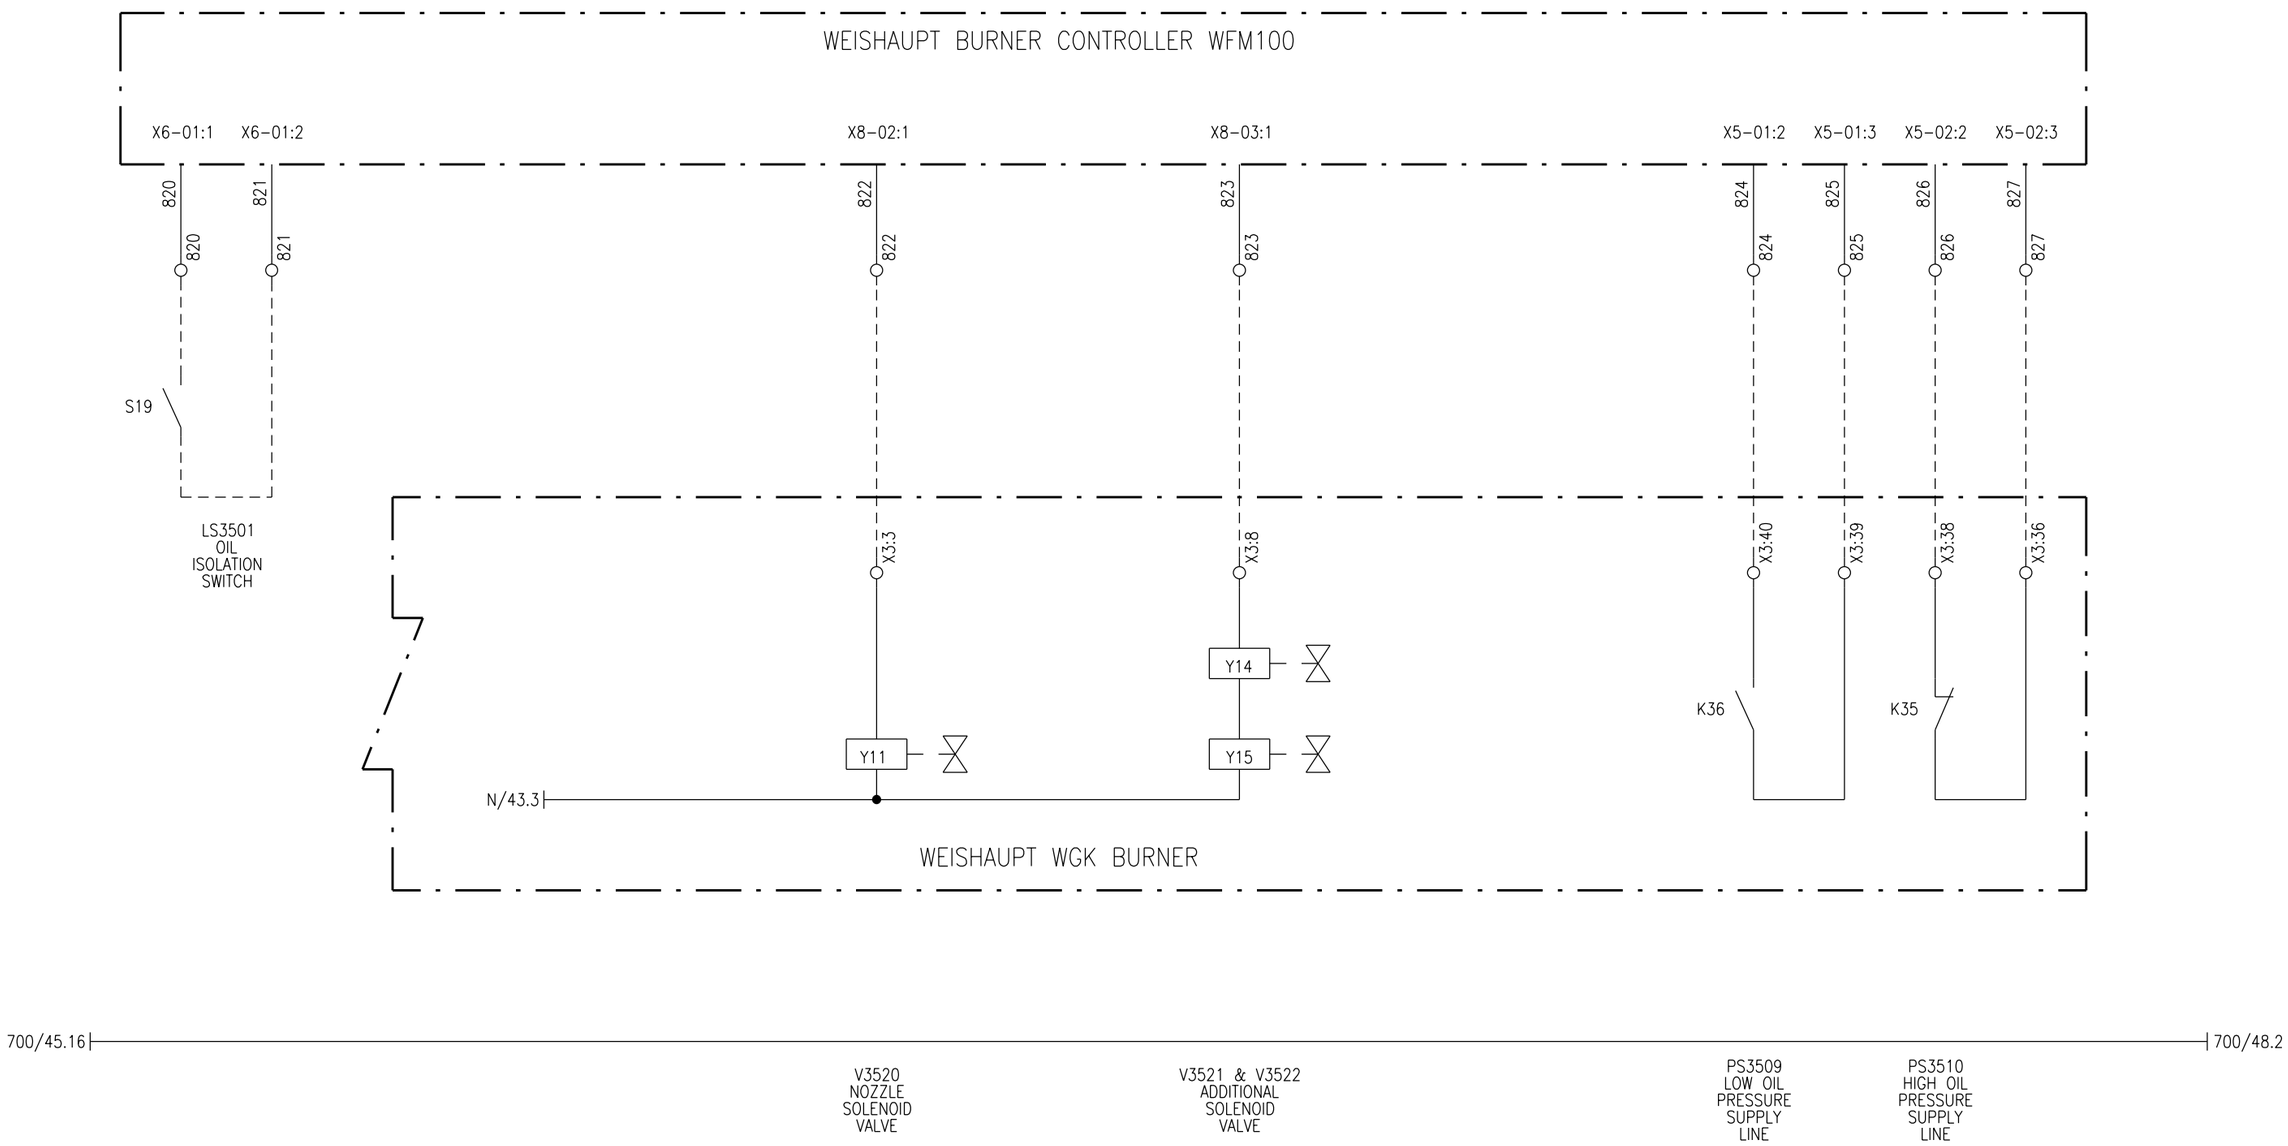

REV	DATE	MODIFICATION	DWN	CHK
1	19/05/14	FOR APPROVAL	MS	DG

ELTEK SYSTEMS Ltd
ELTEK SYSTEMS LTD
ELTEK HOUSE,
NENE VALLEY BUSINESS PARK
OUNDLE, PETERBOROUGH.PE8 4HN
TEL 01832 277590 FAX 01832 273941
Email: info@eltek-systems.com

TITLE

G4 HEATER PANEL
PC32 LINE 4
WSF, LEICESTER

CLIENT

Flo~Mech

FLO-MECH LTD FLO-MECH HOUSE,
PAXTON ROAD, ORTON GOLDHAY
PETERBOROUGH.PE2 5YA, ENGLAND.
TEL +44(0)1733233166
FAX +44(0)1733235200
Email: enquiries@flo-mech.com
Internet: www.flo-mech.com

DATE 19/05/14
DWG NO 5620
SHEET 46 OF 55

1	2	3	4	5	6	7	8	9	10	11	12	13	14	15	16

THIS SHEET IS LEFT BLANK INTENTIONALLY

REV	DATE	MODIFICATION	DWN	CHK
1	19/05/14	FOR APPROVAL	MS	DG

ELTEK SYSTEMS Ltd

ELTEK SYSTEMS LTD
ELTEK HOUSE,
NENE VALLEY BUSINESS PARK
OUNDLE, PETERBOROUGH.PE8 4HN
TEL 01832 277590 FAX 01832 273941
Email: info@eltek-systems.com

TITLE

G4 HEATER PANEL
PC32 LINE 4
WSF, LEICESTER

CLIENT

Flo~Mech

FLO-MECH LTD FLO-MECH HOUSE,
PAXTON ROAD, ORTON GOLDHAY
PETERBOROUGH.PE2 5YA, ENGLAND.
TEL +44(0)1733233166
FAX +44(0)1733235200
Email: enquiries@flo-mech.com
Internet: www.flo-mech.com

DATE 19/05/14
DWG NO 5620
SHEET 47 OF 55

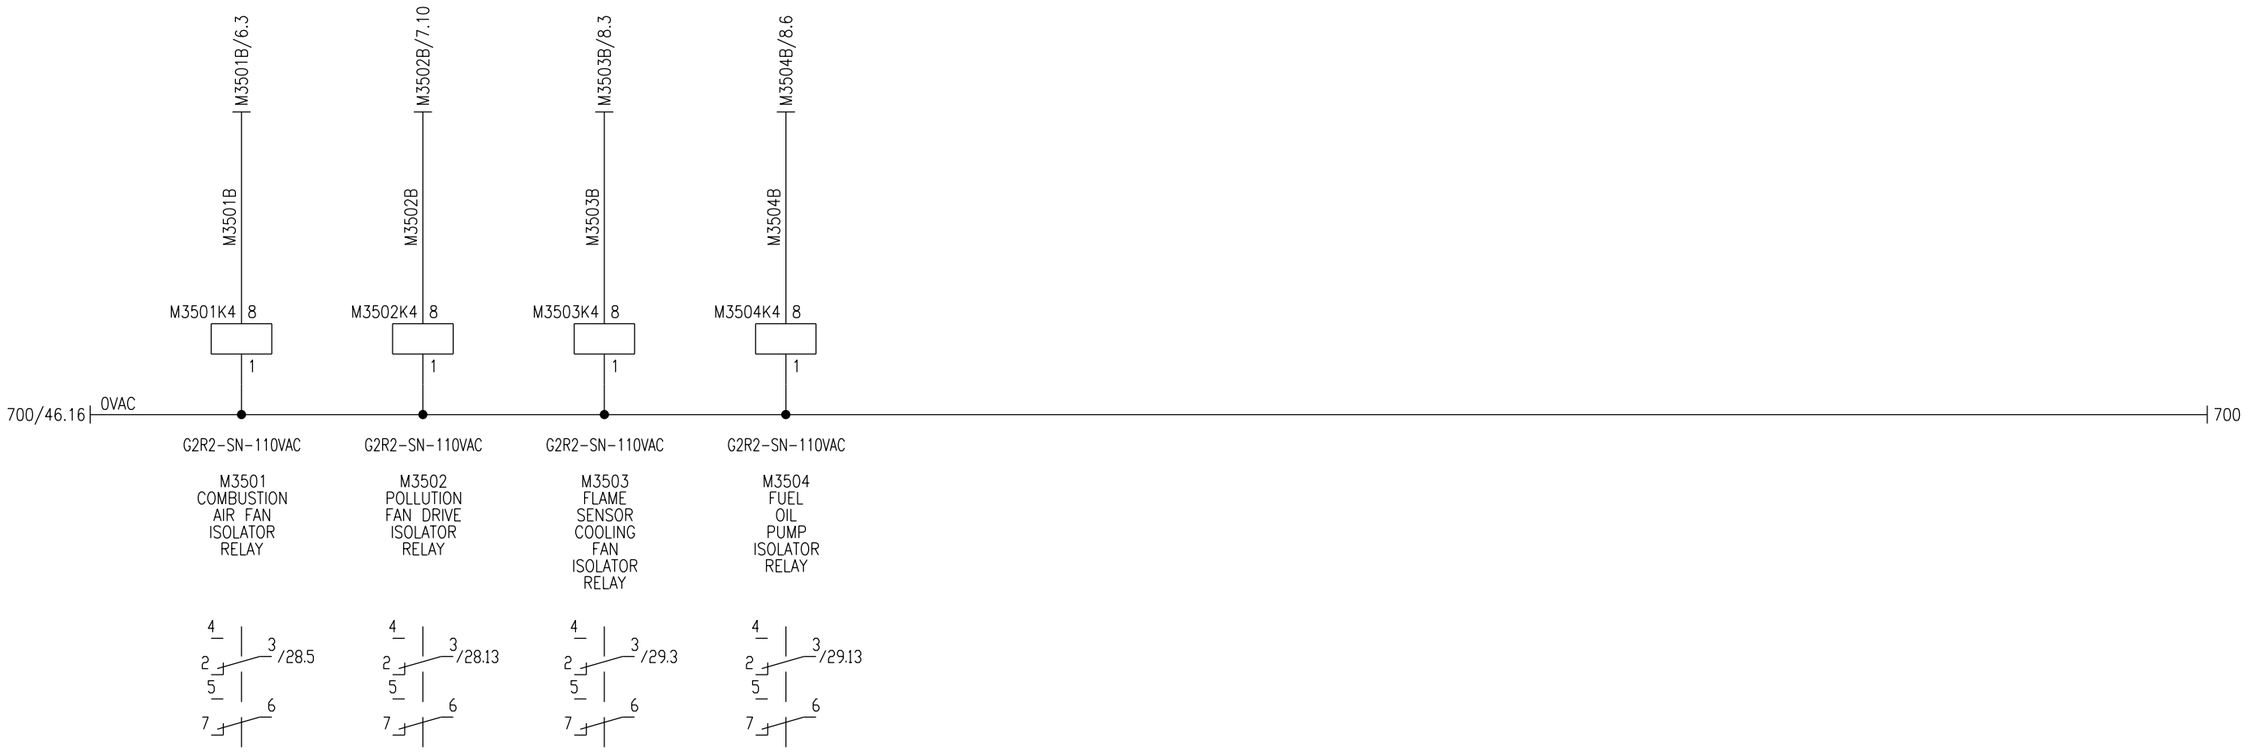

REV	DATE	MODIFICATION	DWN	CHK
1	19/05/14	FOR APPROVAL	MS	DG

ELTEK SYSTEMS Ltd
ELTEK SYSTEMS LTD
ELTEK HOUSE,
NENE VALLEY BUSINESS PARK
OUNDLE, PETERBOROUGH.PE8 4HN
TEL 01832 277590 FAX 01832 273941
Email: info@eltek-systems.com

TITLE

G4 HEATER PANEL
PC32 LINE 4
WSF, LEICESTER

CLIENT

Flo~Mech

FLO-MECH LTD FLO-MECH HOUSE,
PAXTON ROAD, ORTON GOLDHAY
PETERBOROUGH.PE2 5YA, ENGLAND.
TEL +44(0)1733233166
FAX +44(0)1733235200
Email: enquiries@flo-mech.com
Internet: www.flo-mech.com

DATE 19/05/14
DWG NO 5620
SHEET 48 OF 55

1	2	3	4	5	6	7	8	9	10	11	12	13	14	15	16

THIS SHEET IS LEFT BLANK INTENTIONALLY

REV	DATE	MODIFICATION	DWN	CHK
1	19/05/14	FOR APPROVAL	MS	DG

ELTEK SYSTEMS Ltd

ELTEK SYSTEMS LTD
ELTEK HOUSE,
NENE VALLEY BUSINESS PARK
OUNDLE, PETERBOROUGH.PE8 4HN
TEL 01832 277590 FAX 01832 273941
Email: info@eltek-systems.com

TITLE

G4 HEATER PANEL
PC32 LINE 4
WSF, LEICESTER

CLIENT

Flo~Mech

FLO-MECH LTD FLO-MECH HOUSE,
PAXTON ROAD, ORTON GOLDHAY
PETERBOROUGH.PE2 5YA, ENGLAND.
TEL +44(0)1733233166
FAX +44(0)1733235200
Email: enquiries@flo-mech.com
Internet: www.flo-mech.com

DATE 19/05/14
DWG NO 5620
SHEET 49 OF 55

1	2	3	4	5	6	7	8	9	10	11	12	13	14	15	16

HEATER PANEL

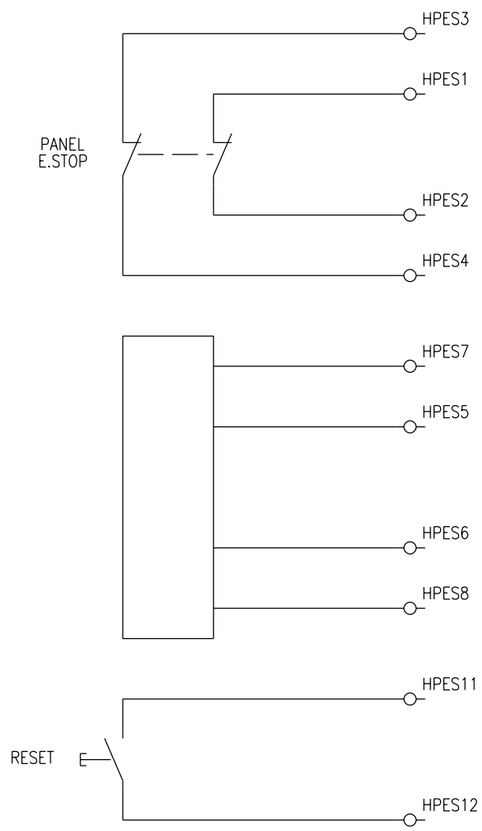

INTERCONNECTIONS TO / FROM CLIENT PANELS

LINE MASTER E-STOP PANEL (IF FITTED)

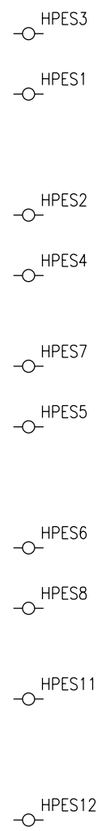

REV	DATE	MODIFICATION	DWN	CHK
1	19/05/14	FOR APPROVAL	MS	DG

ELTEK SYSTEMS Ltd

ELTEK SYSTEMS LTD
ELTEK HOUSE,
NENE VALLEY BUSINESS PARK
OUNDLE, PETERBOROUGH.PE8 4HN
TEL 01832 277590 FAX 01832 273941
Email: info@eltek-systems.com

TITLE

G4 HEATER PANEL
PC32 FLO-THERM
BURSOM L4 WSF, LEICESTER

CLIENT

Flo~Mech

FLO-MECH LTD FLO-MECH HOUSE,
PAXTON ROAD, ORTON GOLDHAY
PETERBOROUGH.PE2 5YA, ENGLAND.
TEL +44(0)1733233166
FAX +44(0)1733235200
Email: enquiries@flo-mech.com
Internet: www.flo-mech.com

DATE 19/05/14

DWG NO 5620

SHEET 50 OF 55

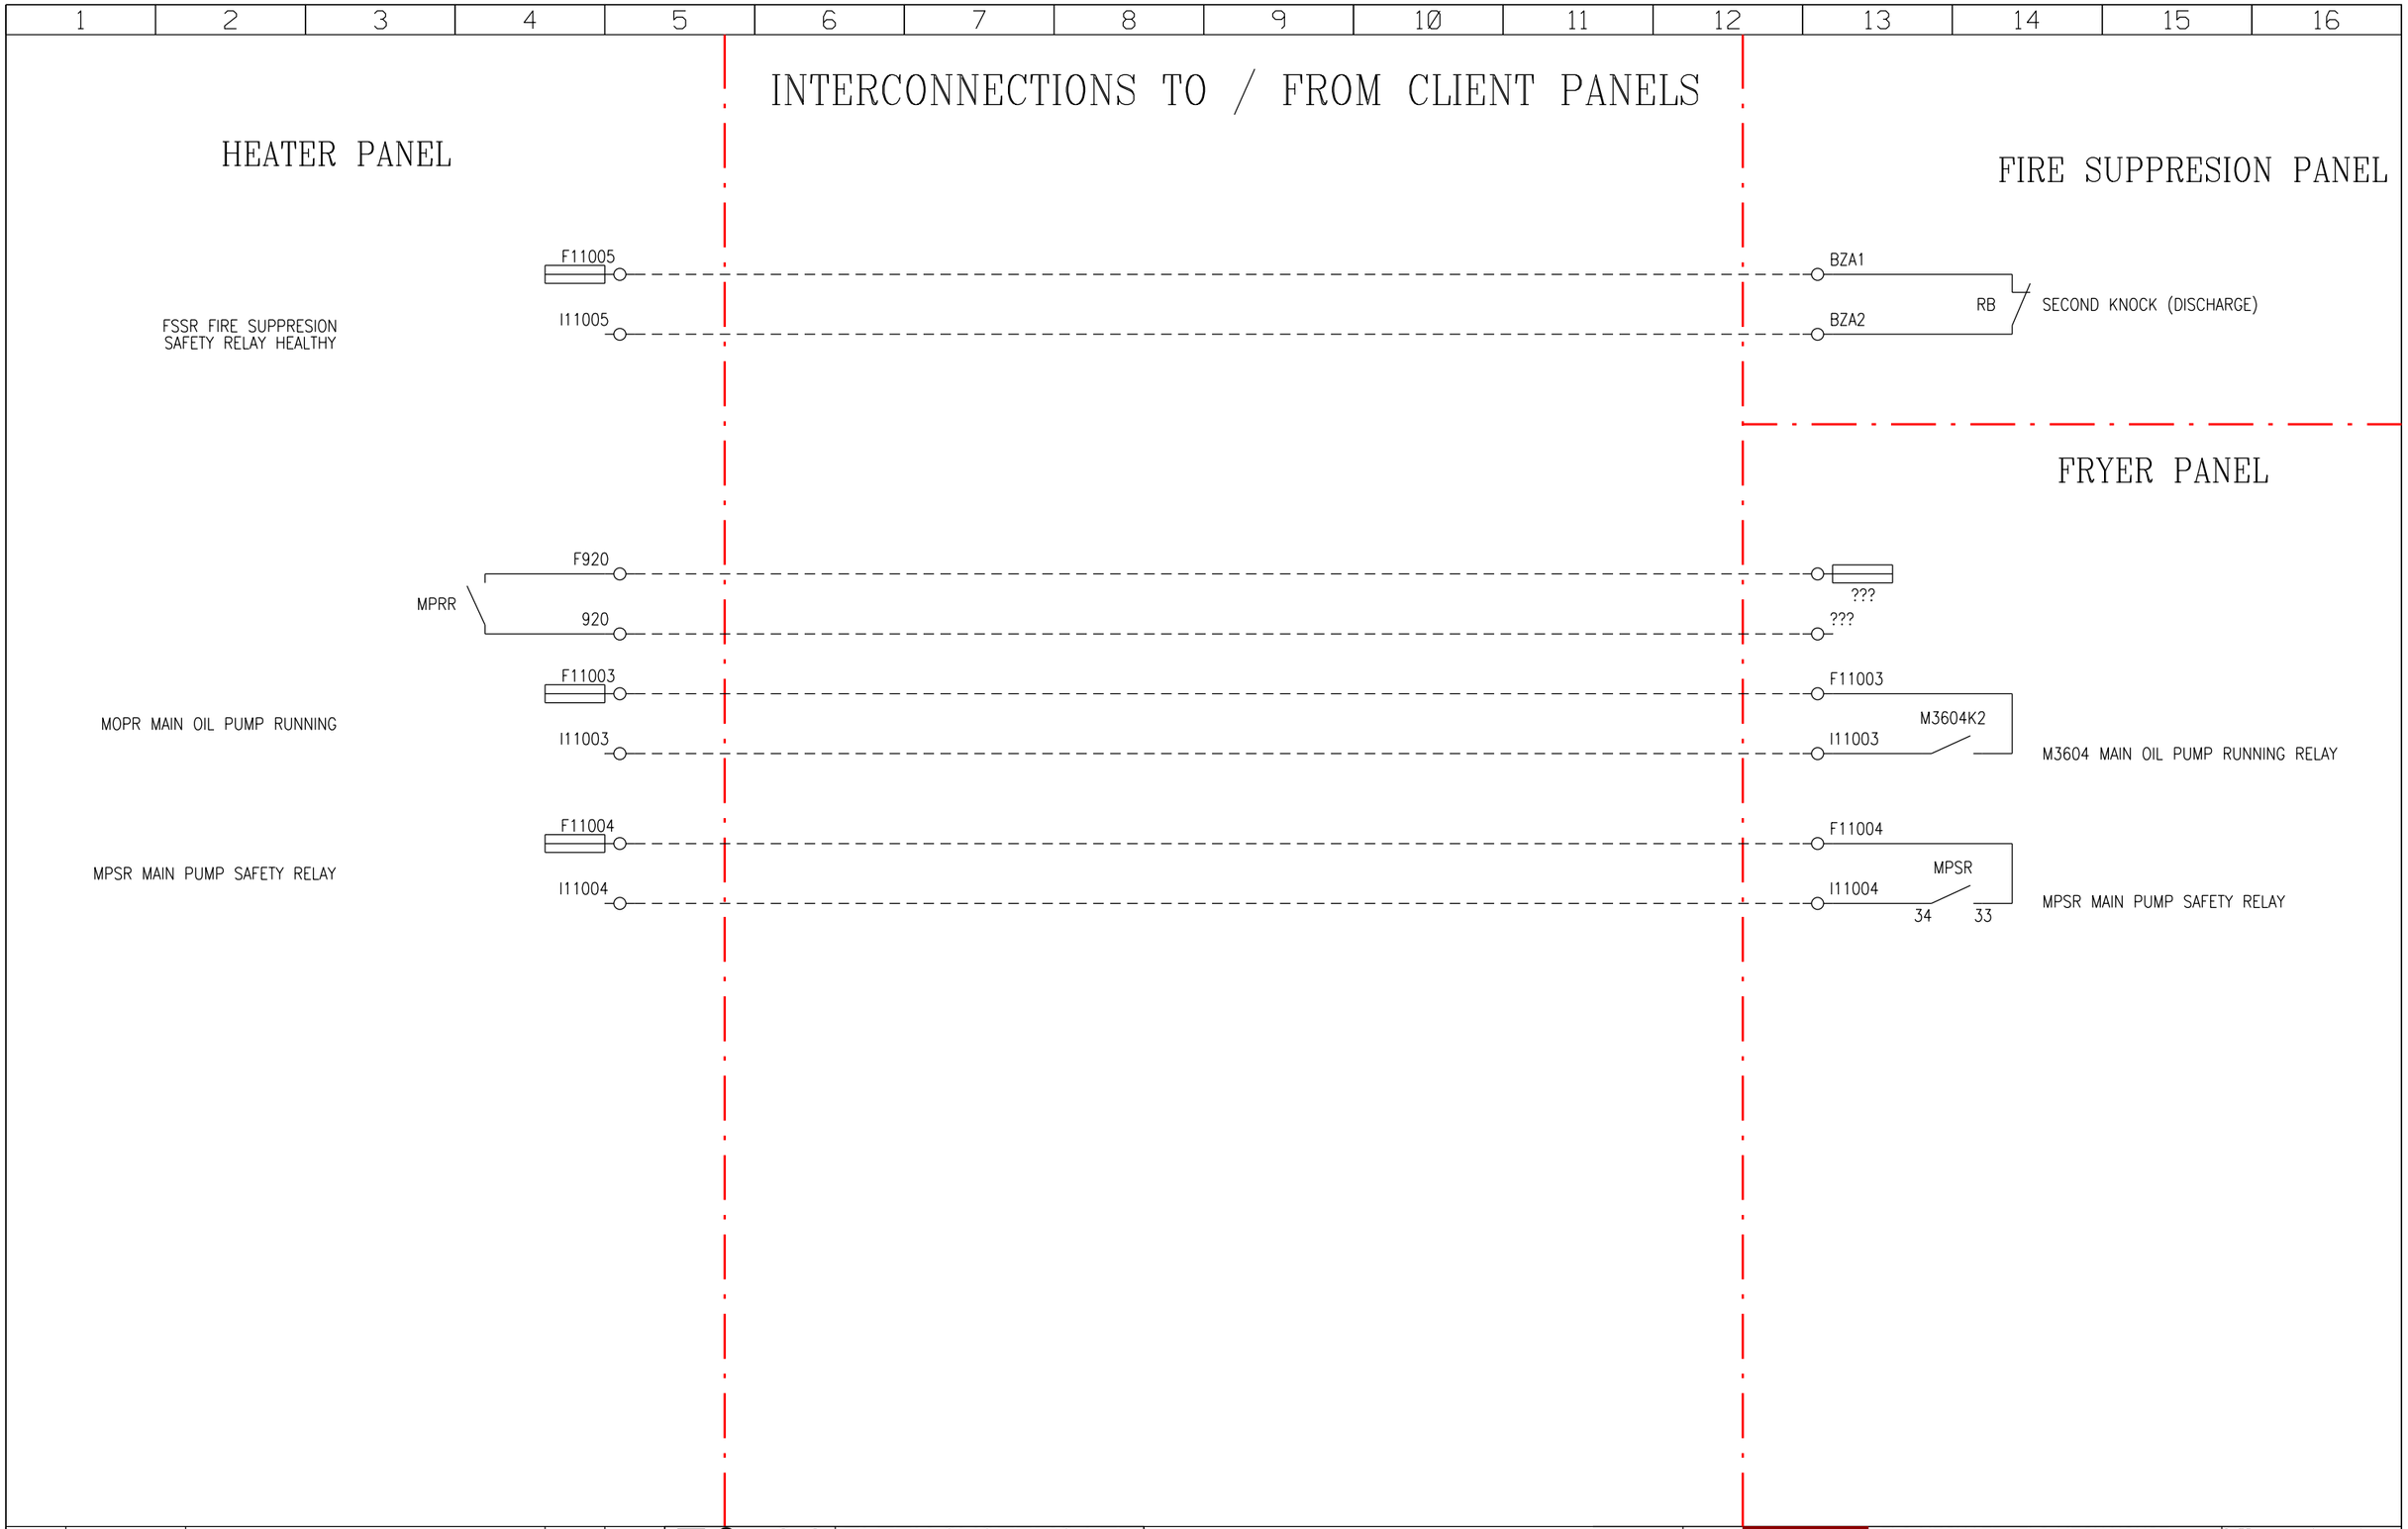

REV	DATE	MODIFICATION	DWN	CHK
1	19/05/14	FOR APPROVAL	MS	DG

ELTEK SYSTEMS Ltd
ELTEK SYSTEMS LTD
ELTEK HOUSE,
NENE VALLEY BUSINESS PARK
OUNDLE, PETERBOROUGH.PE8 4HN
TEL 01832 277590 FAX 01832 273941
Email: info@eltek-systems.com

TITLE

G4 HEATER PANEL
PC32 FLO-THERM
BURSOM L4 WSF, LEICESTER

CLIENT

Flo~Mech

FLO-MECH LTD FLO-MECH HOUSE,
PAXTON ROAD, ORTON GOLDHAY
PETERBOROUGH.PE2 5YA, ENGLAND.
TEL +44(0)1733233166
FAX +44(0)1733235200
Email: enquiries@flo-mech.com
Internet: www.flo-mech.com

DATE 19/05/14
DWG NO 5620
SHEET 51 OF 55

1	2	3	4	5	6	7	8	9	10	11	12	13	14	15	16

THIS SHEET IS LEFT BLANK INTENTIONALLY

REV	DATE	MODIFICATION	DWN	CHK
1	19/05/14	FOR APPROVAL	MS	DG

ELTEK SYSTEMS Ltd

ELTEK SYSTEMS LTD
ELTEK HOUSE,
NENE VALLEY BUSINESS PARK
OUNDLE, PETERBOROUGH.PE8 4HN
TEL 01832 277590 FAX 01832 273941
Email: info@eltek-systems.com

TITLE

G4 HEATER PANEL
PC32 FLO-THERM
BURSOM L4 WSF, LEICESTER

CLIENT

Flo~Mech

FLO-MECH LTD FLO-MECH HOUSE,
PAXTON ROAD, ORTON GOLDHAY
PETERBOROUGH.PE2 5YA, ENGLAND.
TEL +44(0)1733233166
FAX +44(0)1733235200
Email: enquiries@flo-mech.com
Internet: www.flo-mech.com

DATE 19/05/14
DWG NO 5620
SHEET 52 OF 55

1	2	3	4	5	6	7	8	9	10	11	12	13	14	15	16

THIS SHEET IS LEFT BLANK INTENTIONALLY

REV	DATE	MODIFICATION	DWN	CHK
1	19/05/14	FOR APPROVAL	MS	DG

ELTEK SYSTEMS Ltd

ELTEK SYSTEMS LTD
ELTEK HOUSE,
NENE VALLEY BUSINESS PARK
OUNDLE, PETERBOROUGH.PE8 4HN
TEL 01832 277590 FAX 01832 273941
Email: info@eltek-systems.com

TITLE

G4 HEATER PANEL
PC32 FLO-THERM
BURSOM L4 WSF, LEICESTER

CLIENT

Flo~Mech

FLO-MECH LTD FLO-MECH HOUSE,
PAXTON ROAD, ORTON GOLDHAY
PETERBOROUGH.PE2 5YA, ENGLAND.
TEL +44(0)1733233166
FAX +44(0)1733235200
Email: enquiries@flo-mech.com
Internet: www.flo-mech.com

DATE 19/05/14
DWG NO 5620
SHEET 53 OF 55

INTERNAL PANEL LAYOUT

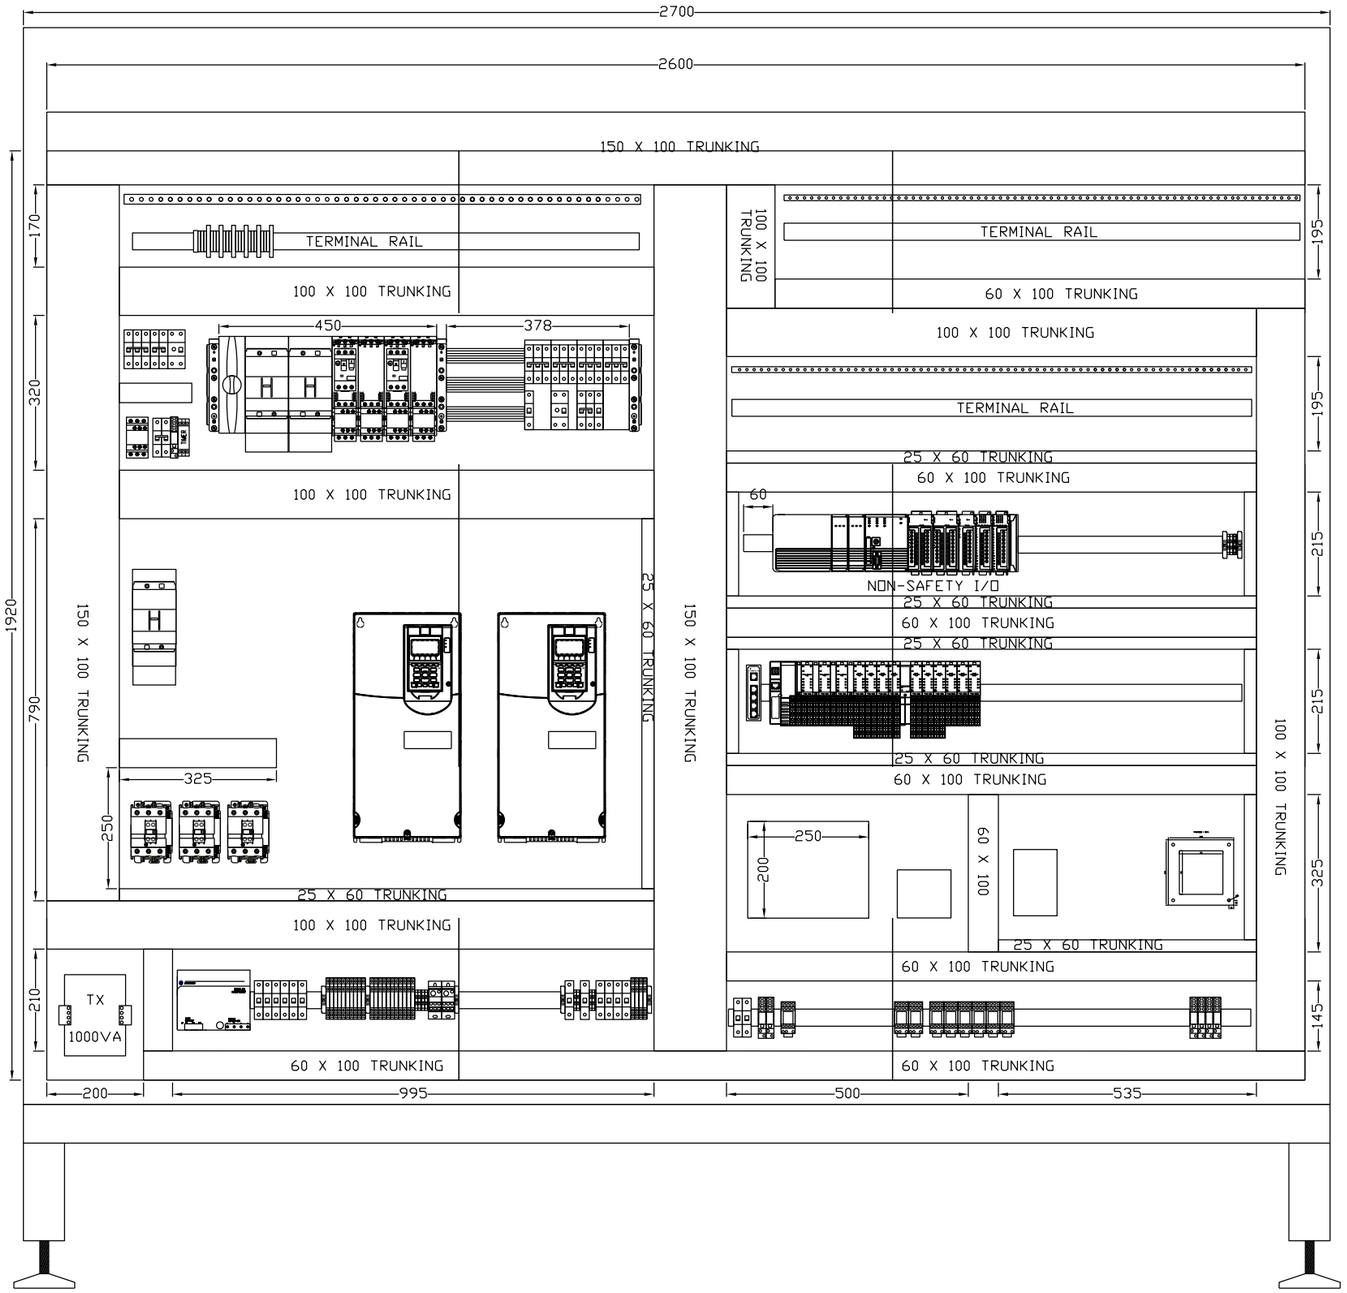

REV	DATE	MODIFICATION	DWN	CHK
1	19/05/14	FOR APPROVAL	MS	DG

ELTEK SYSTEMS LTD
ELTEK HOUSE,
NENE VALLEY BUSINESS PARK
OUNDLE, PETERBOROUGH.PE8 4HN
TEL 01832 277590 FAX 01832 273941
Email: info@eltek-systems.com

TITLE

G4 HEATER PANEL
PC32 FLO-THERM
BURSOM L4 WSF, LEICESTER

CLIENT

FLO-MECH LTD FLO-MECH HOUSE,
PAXTON ROAD, ORTON GOLDHAY
PETERBOROUGH.PE2 5YA, ENGLAND.
TEL +44(0)1733233166
FAX +44(0)1733235200
Email: enquiries@flo-mech.com
Internet: www.flo-mech.com

DATE 19/05/14
DWG NO 5620
SHEET 54 OF 55

EXTERNAL PANEL LAYOUT

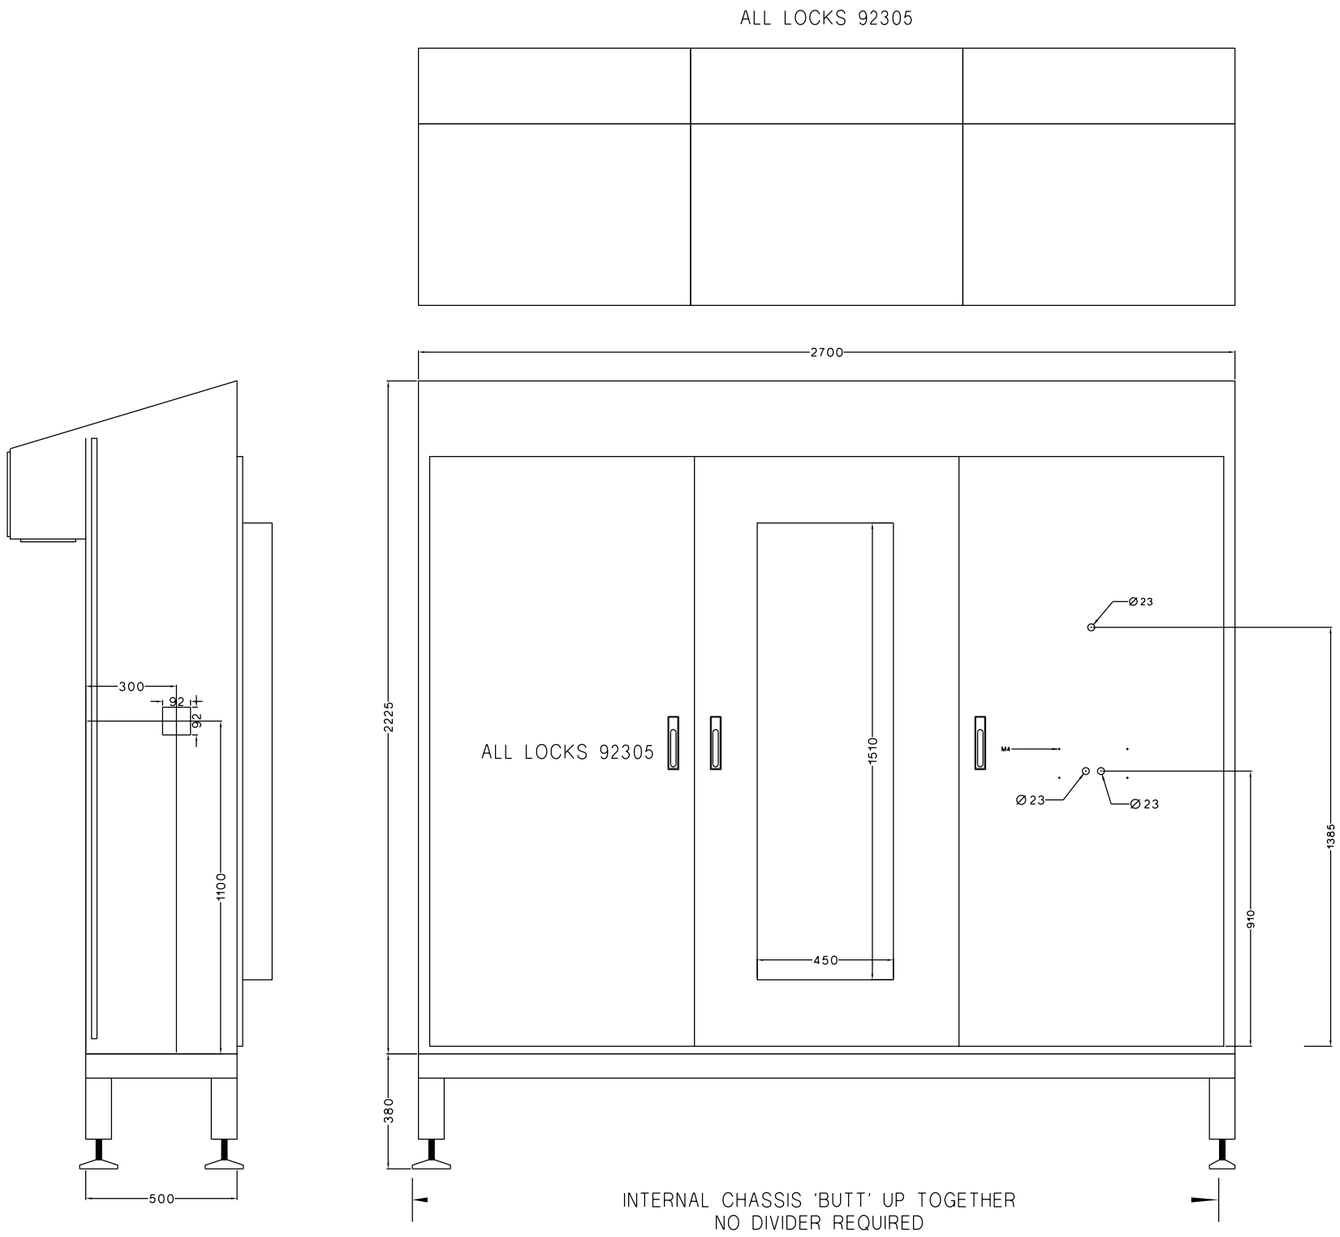

REV	DATE	MODIFICATION	DWN	CHK
1	19/05/14	FOR APPROVAL	MS	DG

ELTEK SYSTEMS Ltd

ELTEK SYSTEMS LTD
ELTEK HOUSE,
NENE VALLEY BUSINESS PARK
OUNDLE, PETERBOROUGH.PE8 4HN
TEL 01832 277590 FAX 01832 273941
Email: info@eltek-systems.com

TITLE

G4 HEATER PANEL
PC32 FLO-THERM
BURSOM L4 WSF, LEICESTER

CLIENT

Flo~Mech

FLO-MECH LTD FLO-MECH HOUSE,
PAXTON ROAD, ORTON GOLDHAY
PETERBOROUGH.PE2 5YA, ENGLAND.
TEL +44(0)1733233166
FAX +44(0)1733235200
Email: enquiries@flo-mech.com
Internet: www.flo-mech.com

DATE 19/05/14
DWG NO 5620
SHEET 55 OF 55